

בית כורכר



BEIT KURKAR

שם הפרויקט:

וילת בוטיק בקיסריה

מיקום הפרויקט:

קיסריה, רובע 13 (מגרש לימודי)

מנהל:

שריקי

שם הבניין:

תכנית פיתוח שטח

חסי' גריליון:

05

ק"מ

1:100

רשימת ניליונות:

01 שער

02 קונסטרוקציה ומחיצה

03 ניתוח אזור וסביבה

04 תכנית העמדה וסלול שטחים

05 תכנית פיתוח שטח

06 תכנית מרחק וקרקע

07 תכנית קומה א' וגג

08 חיתוכים

09 סכומים סטטיסטיים

10 תכנית קומה קרקע

11 תכנית קומה א'

12 חיתוכים

13 חתך A-A

14 חתך B-B

15 גיליון מדרגות

16 סרטי בניין

17 רשימת אלומיניום וגזרות

18 עיצוב קנים - חלל המגורים

19 עיצוב ריהוט - אי המטבח

20 דרימות חוץ

21 דרימות פנים

22 חלל

23

מנהל:



הנדסאים - אדריכלות ועיצוב פנים

שם המעשה/ת.ת.:

תאריך:

10.2026

N

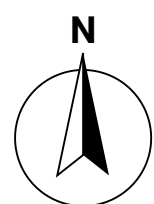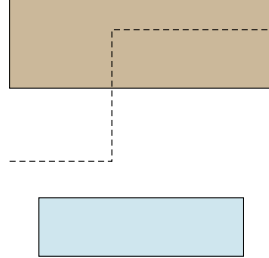

מקרא חומרים:


חומרים - דשא סינטטי/טבעי/סלעי	
ערוגות צמחייה ים-תיכוניות (לבוש, רחמי, דגניים)	
דק עץ טיק / IPE על קירות אלומיניום	
ריצוף אבן גיר בריכה/90 - חספוס R11	
בריכה - ספיסס זכוכית בגוון חול	
גדר בניה בריחסי אבן כווכר 1.80/1.50	
גדר משרבית - קיד נמוך 0.60 + זכוכית לוקי הגוף	

מקרא צמחייה:

עץ זית עתיק (העתיק)	
חורב מצוי	
קטניות פורחות	
חשבוניות חסות	
זית בריחסי	

הערות פיתוח:

- ניקוד עילי בשטח 1.5% רחוק מהמבנה, אל ערוגות מלחול
- השקיה בטפטוף ממוחשבת, צמחייה חסכונית במים.
- תאורת ניה LED נמוכה (Dark-Sky), נופי שקיפה במדרגות.
- גדר בטוחות לבריכה לפי הנחיות משרד הבריאות.
- גדר דרומית/צפונית 1.80 לאורך הבריכה, 1.50 ביחיד.

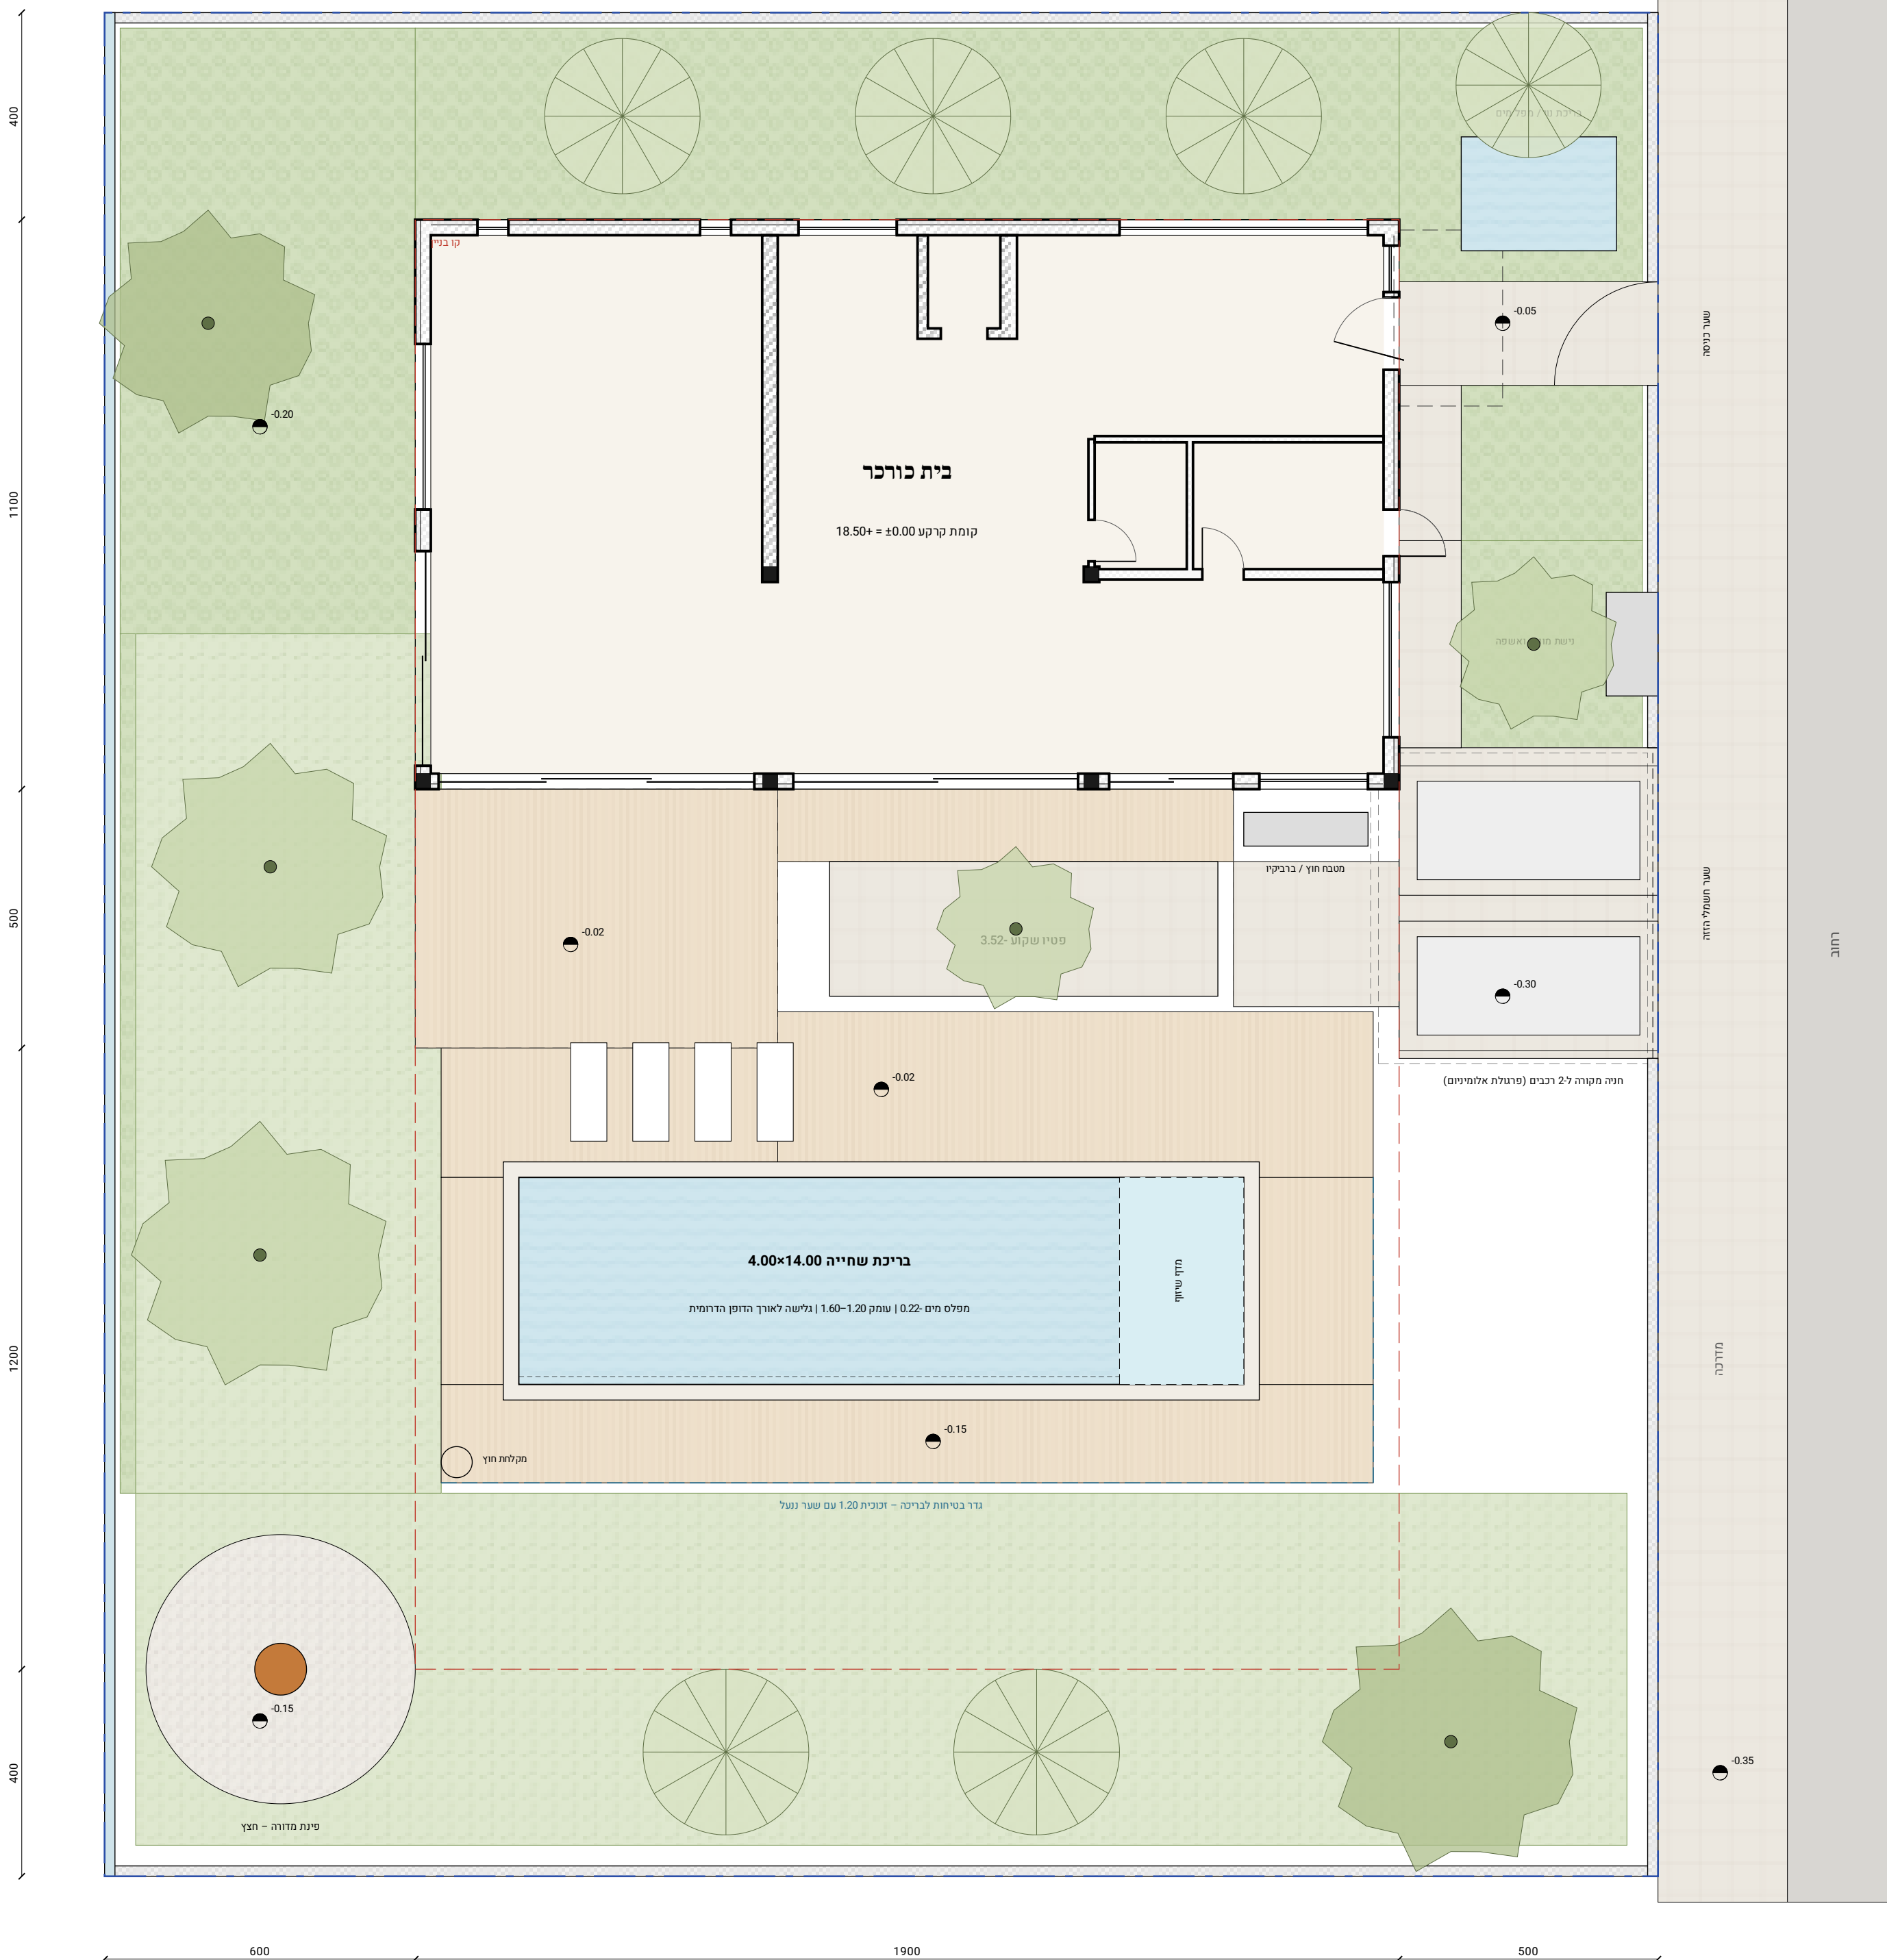

תכנית פיתוח שטח

ק"מ 1:100