

## בית כורכר

BEIT KURKAR

שם הפרויקט:  
יולת בוטיק בקיסריה

מיקום הפרויקט:  
קיסריה, רובע 13 (מגרש לימודי)

מנהל:  
שרית שריקי

שם הבניין:  
תכנית מרתף וקרקע

תאריך:  
06

ק"מ:  
1:100

תאריך:  
06

רשימת ניליונות:




- שער
- קונסט ומחבר
- ניחוח אוויר וסביבה
- תכנית העבודה וסלול שטחים
- תכנית פיתוח שטח
- תכנית מרתף וקרקע**
- תכנית קומה א נגד
- חיתות
- חלונות
- סמכות טכניות
- תכנית קומה קרקע
- תכנית קומה א
- חיתות
- חוק A-A
- חוק B-B
- ניליון מדרגות
- פרטי בניין
- רשימת אלומיניום וגזרות
- ציבוי קומות – חלל המגורים
- ציבוי קומות – אי המטבח
- רשימת חזן
- רשימת פנים
- חזית

מנהל:  
תכנון – אדריכלות ועיצוב פנים

שם המעשה/ת.ד.:

תאריך:

10.2026

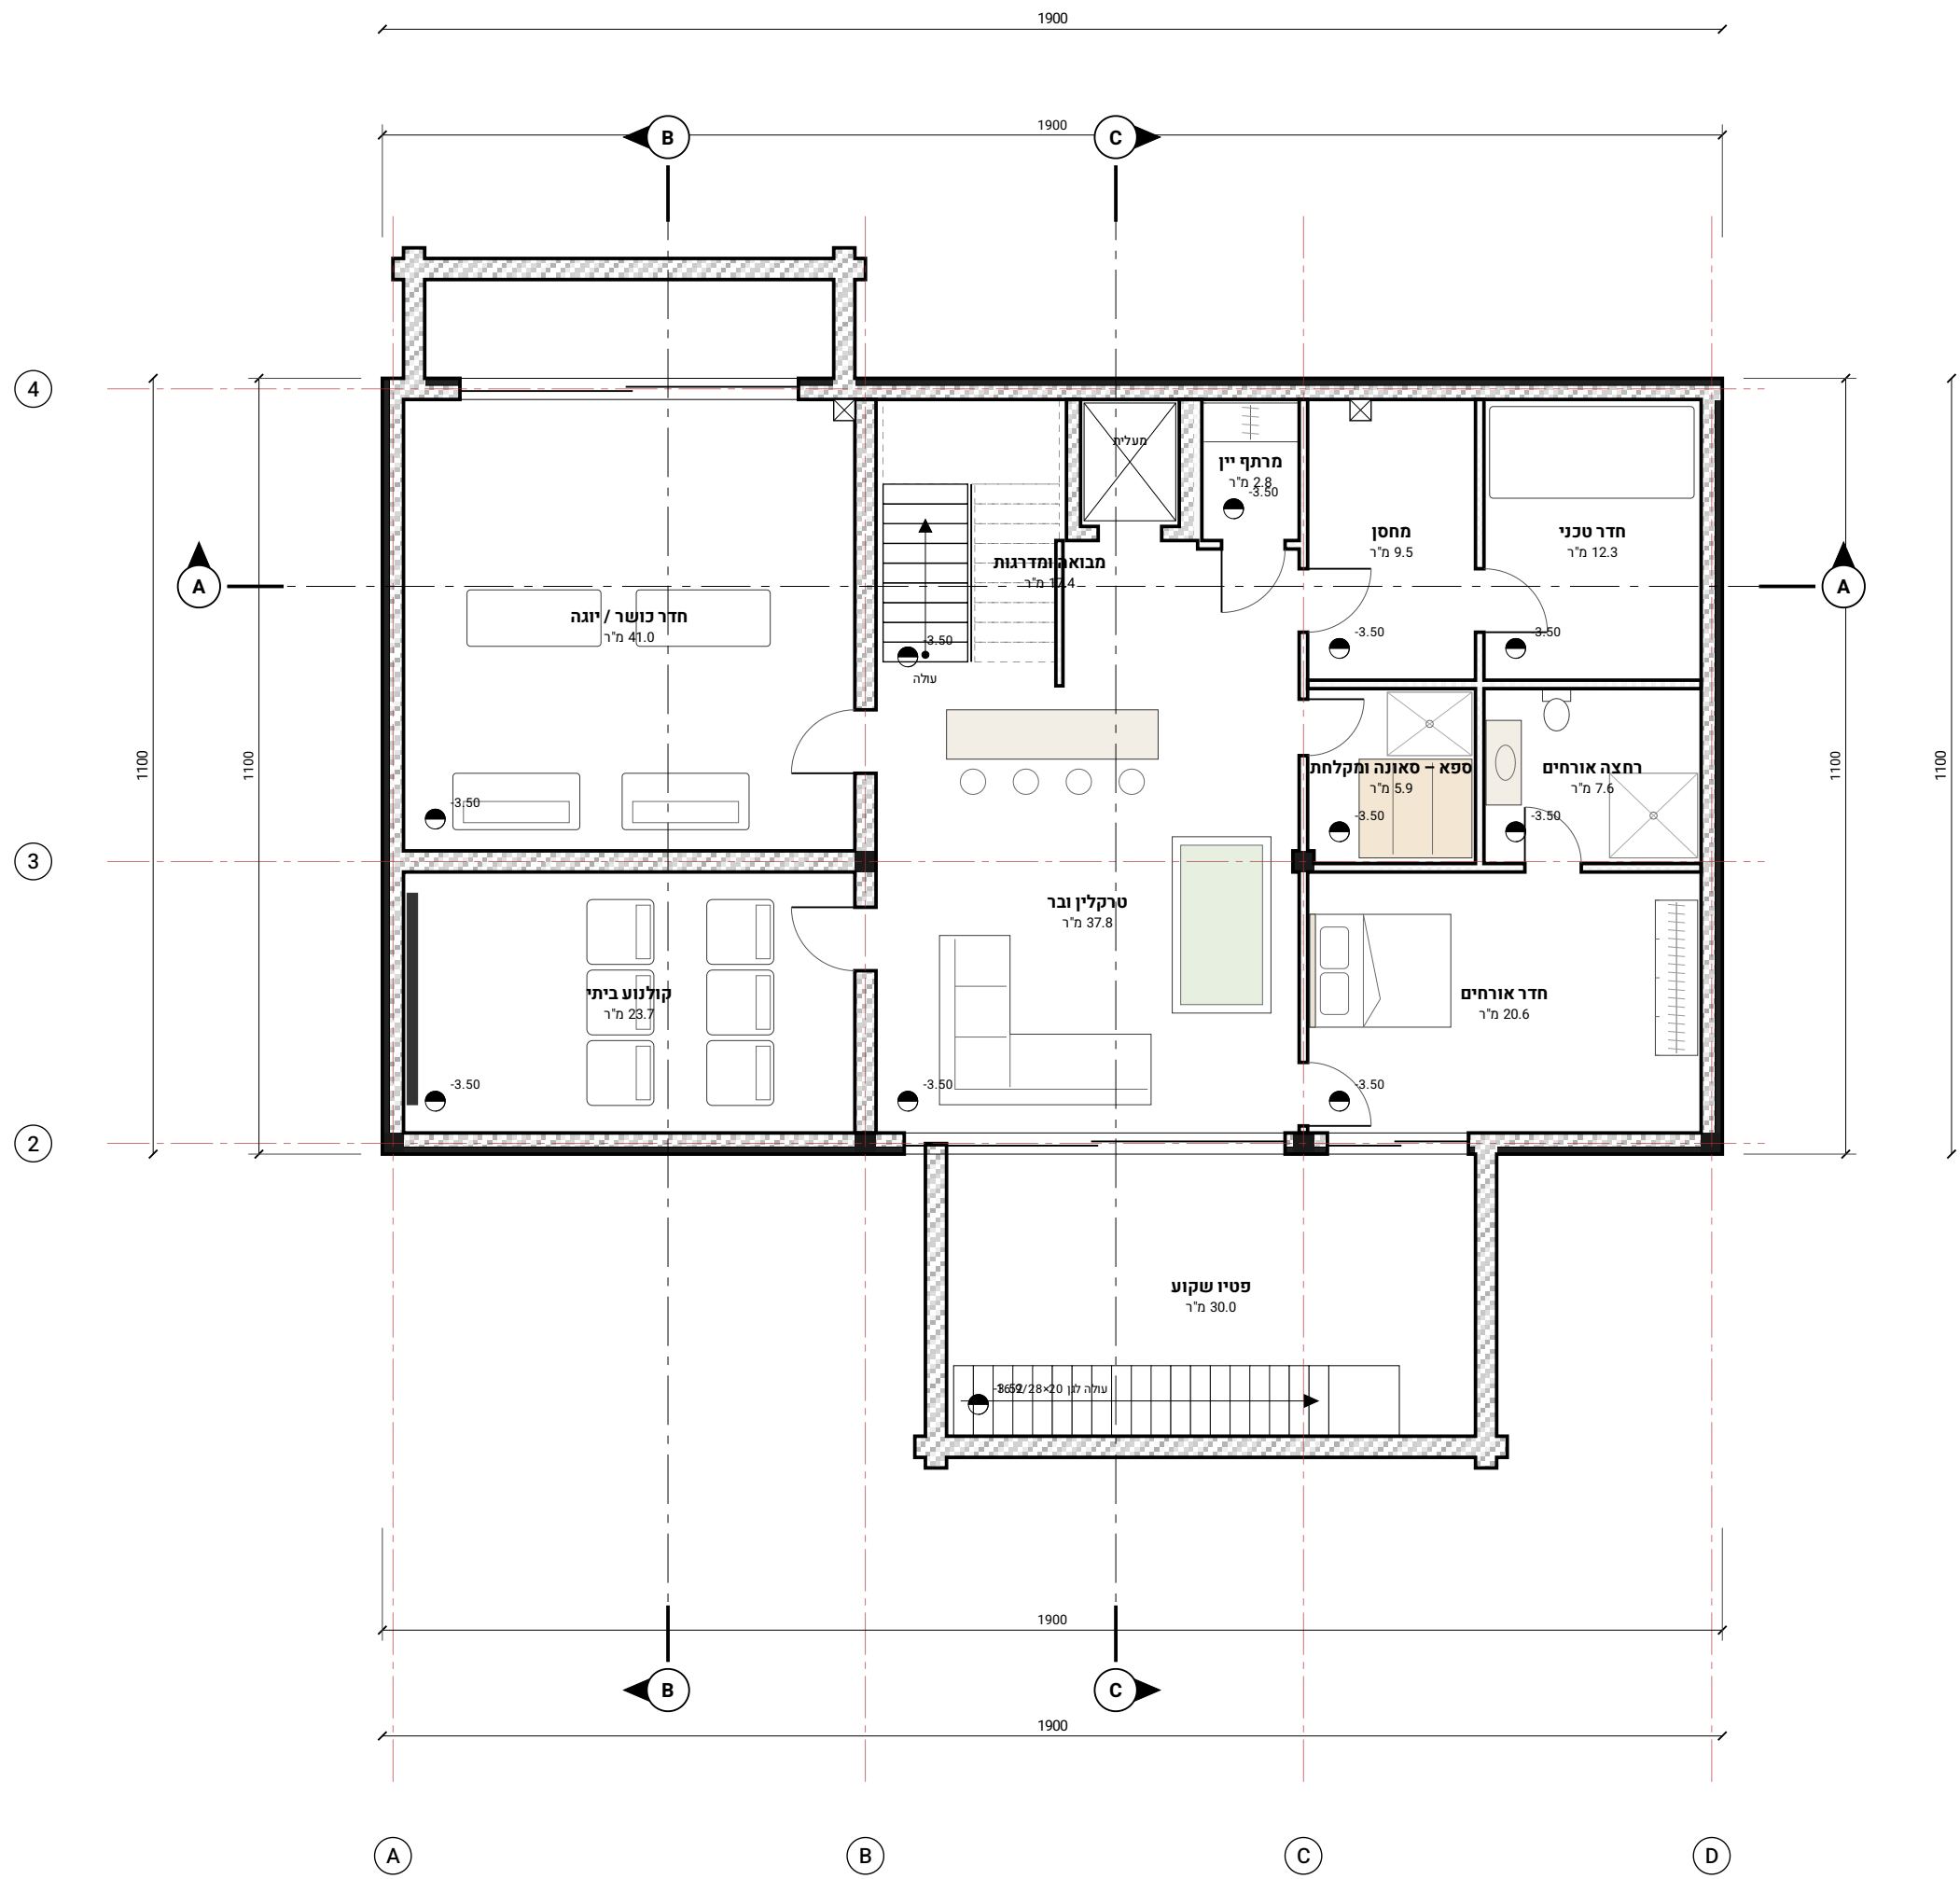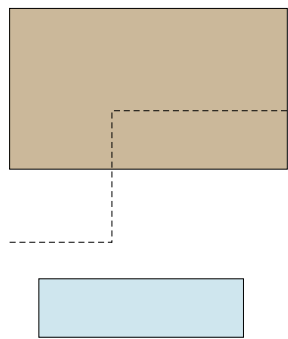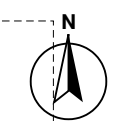


טבלת חללים - קומת מרתף

| מ"ר | חלל                | שטח מ"ר | רצפות          | ג. תקרה |
|-----|--------------------|---------|----------------|---------|
| 81  | קולנוע ביתי        | 23.7    | שטיח אקוסטי    | 2.90    |
| 82  | חדר כושר / יוזה    | 41.0    | פרקט ספורט     | 2.90    |
| 83  | טרקלין ובר         | 37.8    | טורצ'ן 120/120 | 2.90    |
| 84  | חדר אורחים         | 20.6    | פרקט עץ        | 2.90    |
| 85  | רחצה אורחים        | 7.6     | טורצ'ן 60/120  | 2.60    |
| 86  | ספא - סאונה ומקלחת | 5.9     | אבן טבעית      | 2.60    |
| 87  | מחסן               | 9.5     | טורצ'ן 60/60   | 2.60    |
| 88  | חדר טכני           | 12.3    | בטון מוחלק     | 2.90    |
| 89  | מרחץ יין           | 2.8     | אבן טבעית      | 2.60    |
| 810 | מבואה ומדרגות      | 17.4    | טורצ'ן 120/120 | 2.90    |
| 811 | מסדרון             | 30.0    | אבן לריכה      | -       |
|     | סה"כ פנים (טוט)    | 178.6   |                |         |

## תכנית קומת מרתף

ק"מ 1:100

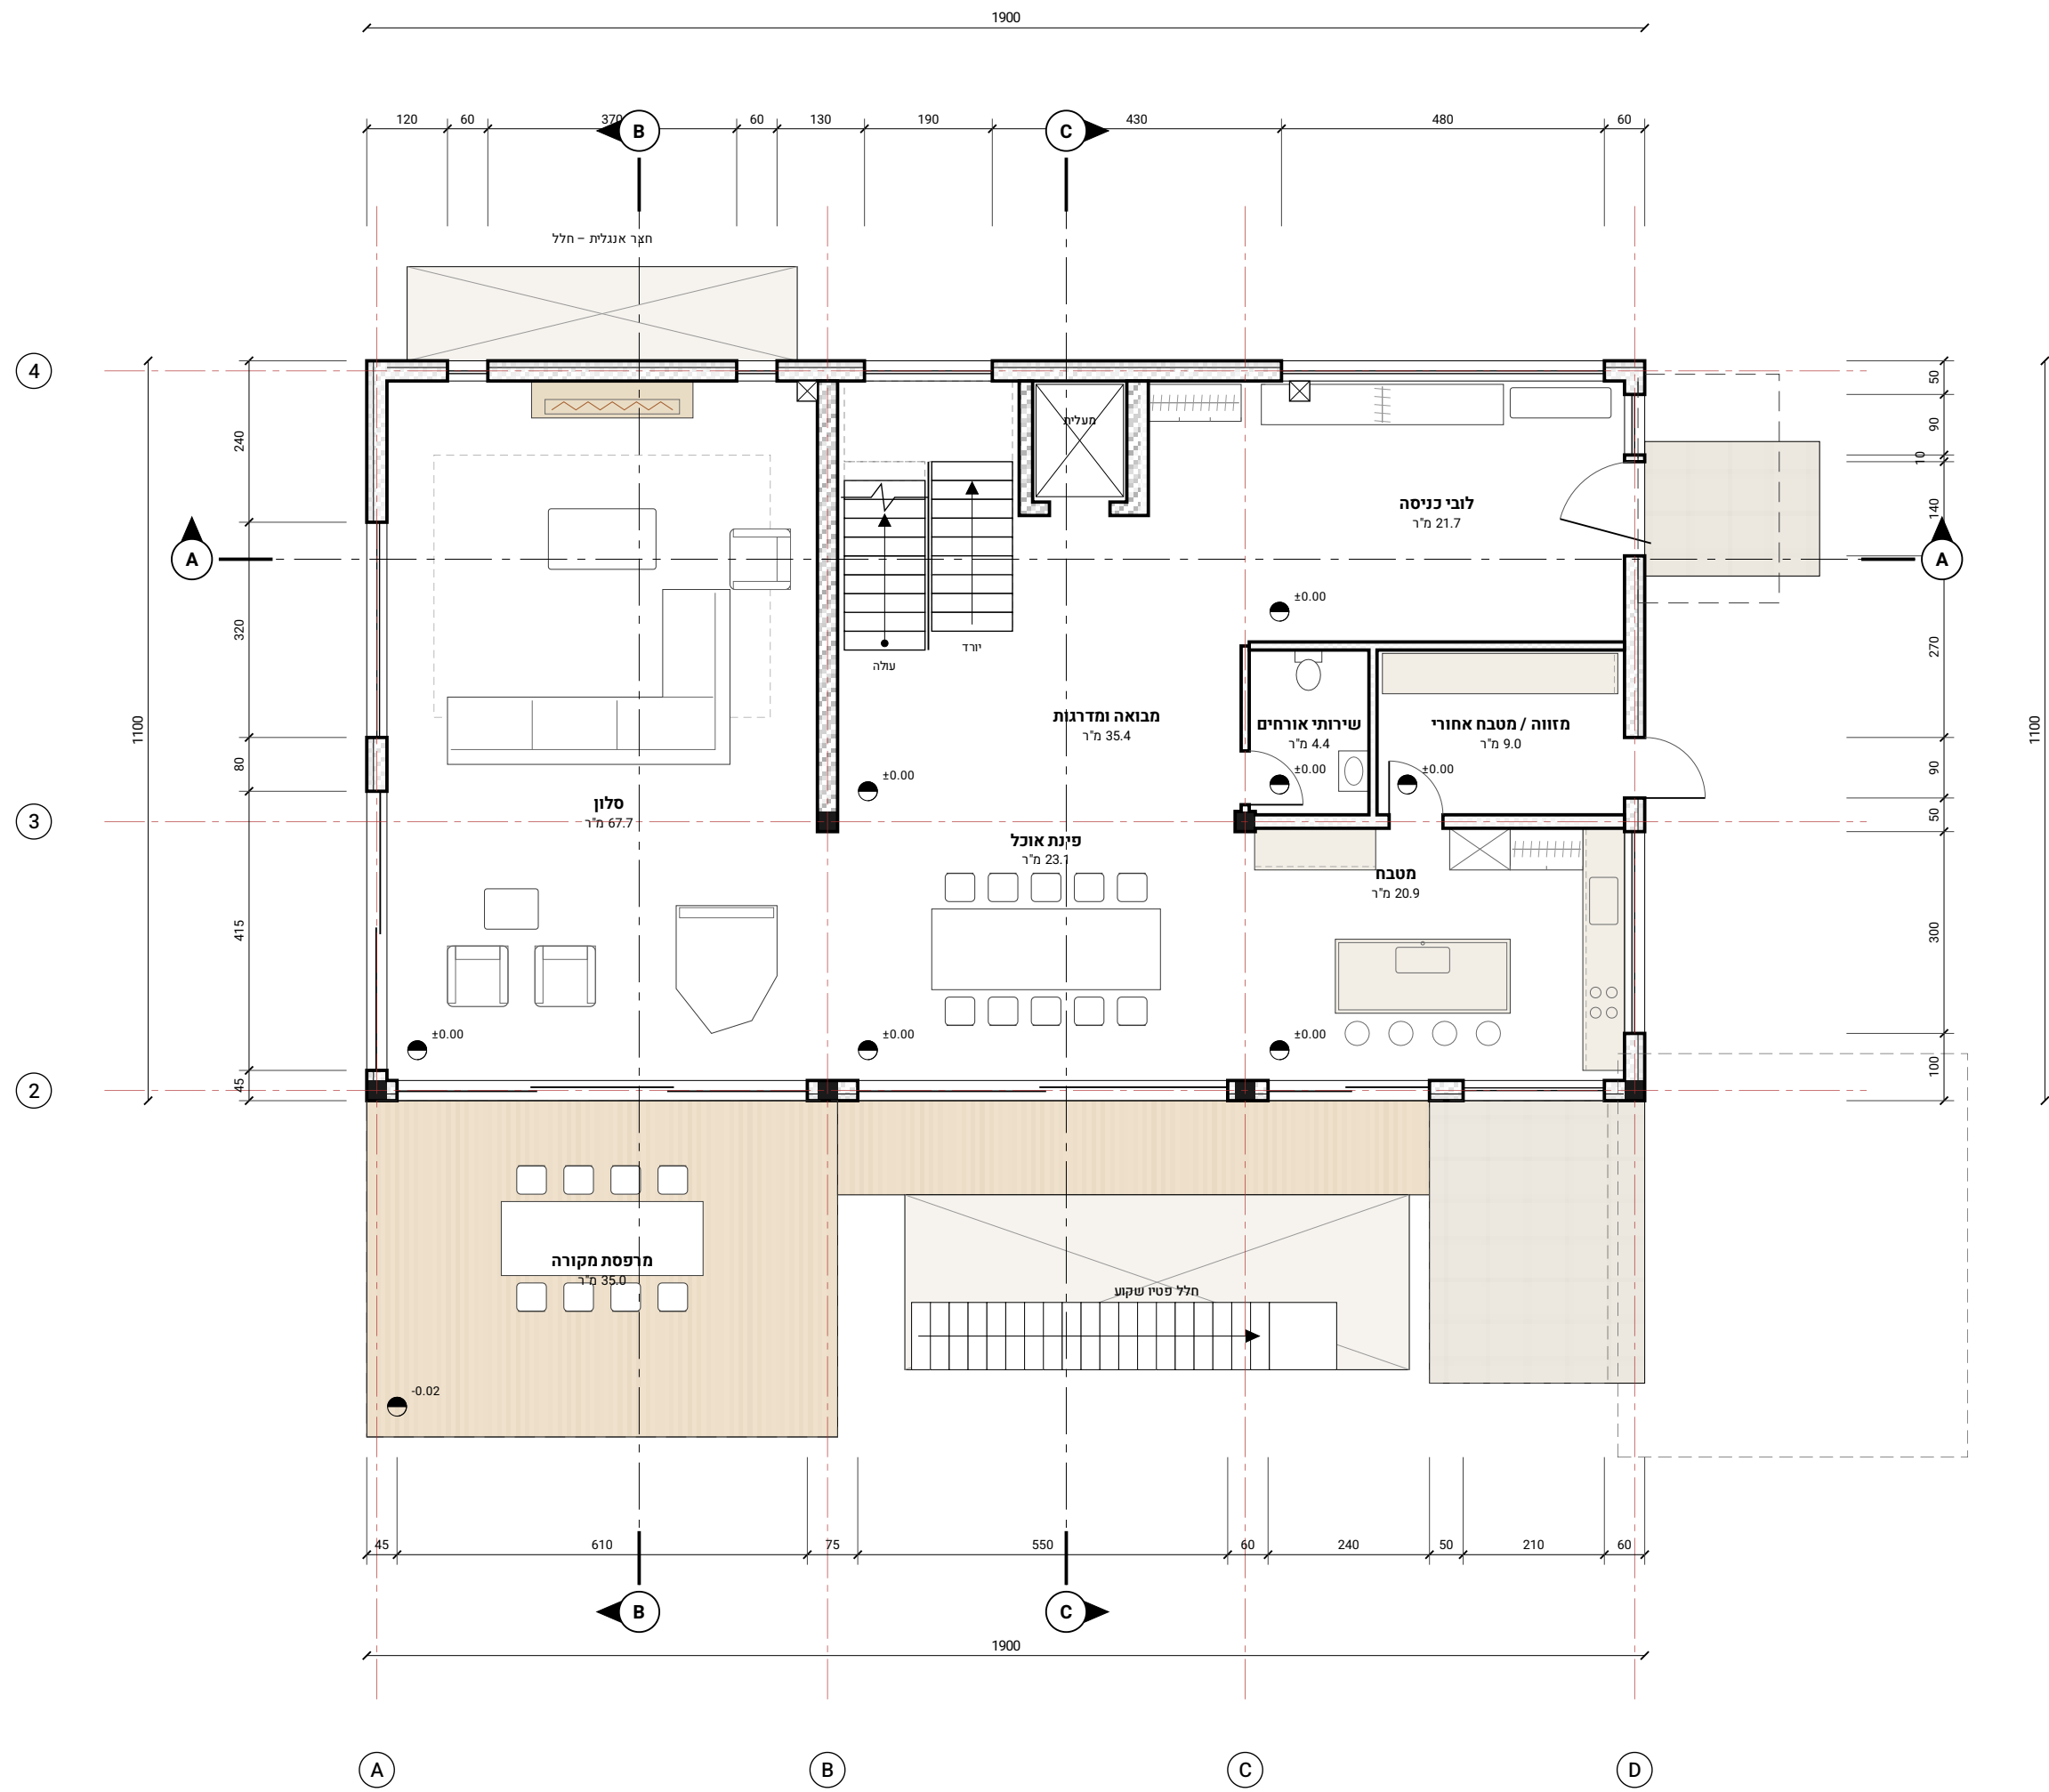

טבלת חללים - קומת קרקע

| מ"ר | חלל                | שטח מ"ר | רצפות          | ג. תקרה |
|-----|--------------------|---------|----------------|---------|
| 01  | סלון               | 67.7    | טורצ'ן 120/120 | 3.10    |
| 02  | פינת אוכל          | 23.1    | טורצ'ן 120/120 | 3.10    |
| 03  | מטבח               | 20.9    | טורצ'ן 120/120 | 3.00    |
| 04  | מבואה ומדרגות      | 35.4    | טורצ'ן 120/120 | 3.10    |
| 05  | שידורי אורחים      | 4.4     | טורצ'ן 60/120  | 2.60    |
| 06  | מזווה / מטבח אחורי | 9.0     | טורצ'ן 60/60   | 2.60    |
| 07  | לובי כניסה         | 21.7    | אבן טבעית      | 3.10    |
| 08  | מחסן חומרים        | 35.0    | דק עץ טיק      | -       |
|     | סה"כ פנים (טוט)    | 182.2   |                |         |

## תכנית קומת קרקע

ק"מ 1:100

