

בית כורכר

BEIT KURKAR

שם הפרויקט:
וילת בוטיק בקיסריה

מיקום הפרויקט:
קיסריה, רובע 13 (מגרש לימודי)

מנהל:
שירן שריקי

שם הבניין:
תכניות קומה א' וגג

מס' בניין:
07




ק"מ:
1:100

רשימת ניליונות:	
01	שער
02	קונסטרוקציה ומחיצה
03	ניחוח אחרי הסביבה
04	תכנית העמדה וסלול שטחים
05	תכנית פיתוח שטח
06	תכנית פרקט וקרקע
07	תכנית קומה א' וגג
08	חיתות
09	חיתות
10	סככות פסטיות
11	תכנית קומה א'
12	תכנית קומה א'
13	חיתות
14	חיתות A-A
15	חיתות B-B
16	נליון מדרגות
17	פרטי בנין
18	רשימת אלמנטים וגזרות
19	עיצוב פנים - חלל המגורים
20	עיצוב ריהוט - אי המטבח
21	דרימות חוץ
22	דרימות פנים
23	תודה

מנהל:
הנדסאים - אדריכלות ועיצוב פנים


שם המעשה/ת.ד.:

תאריך:
10.2026

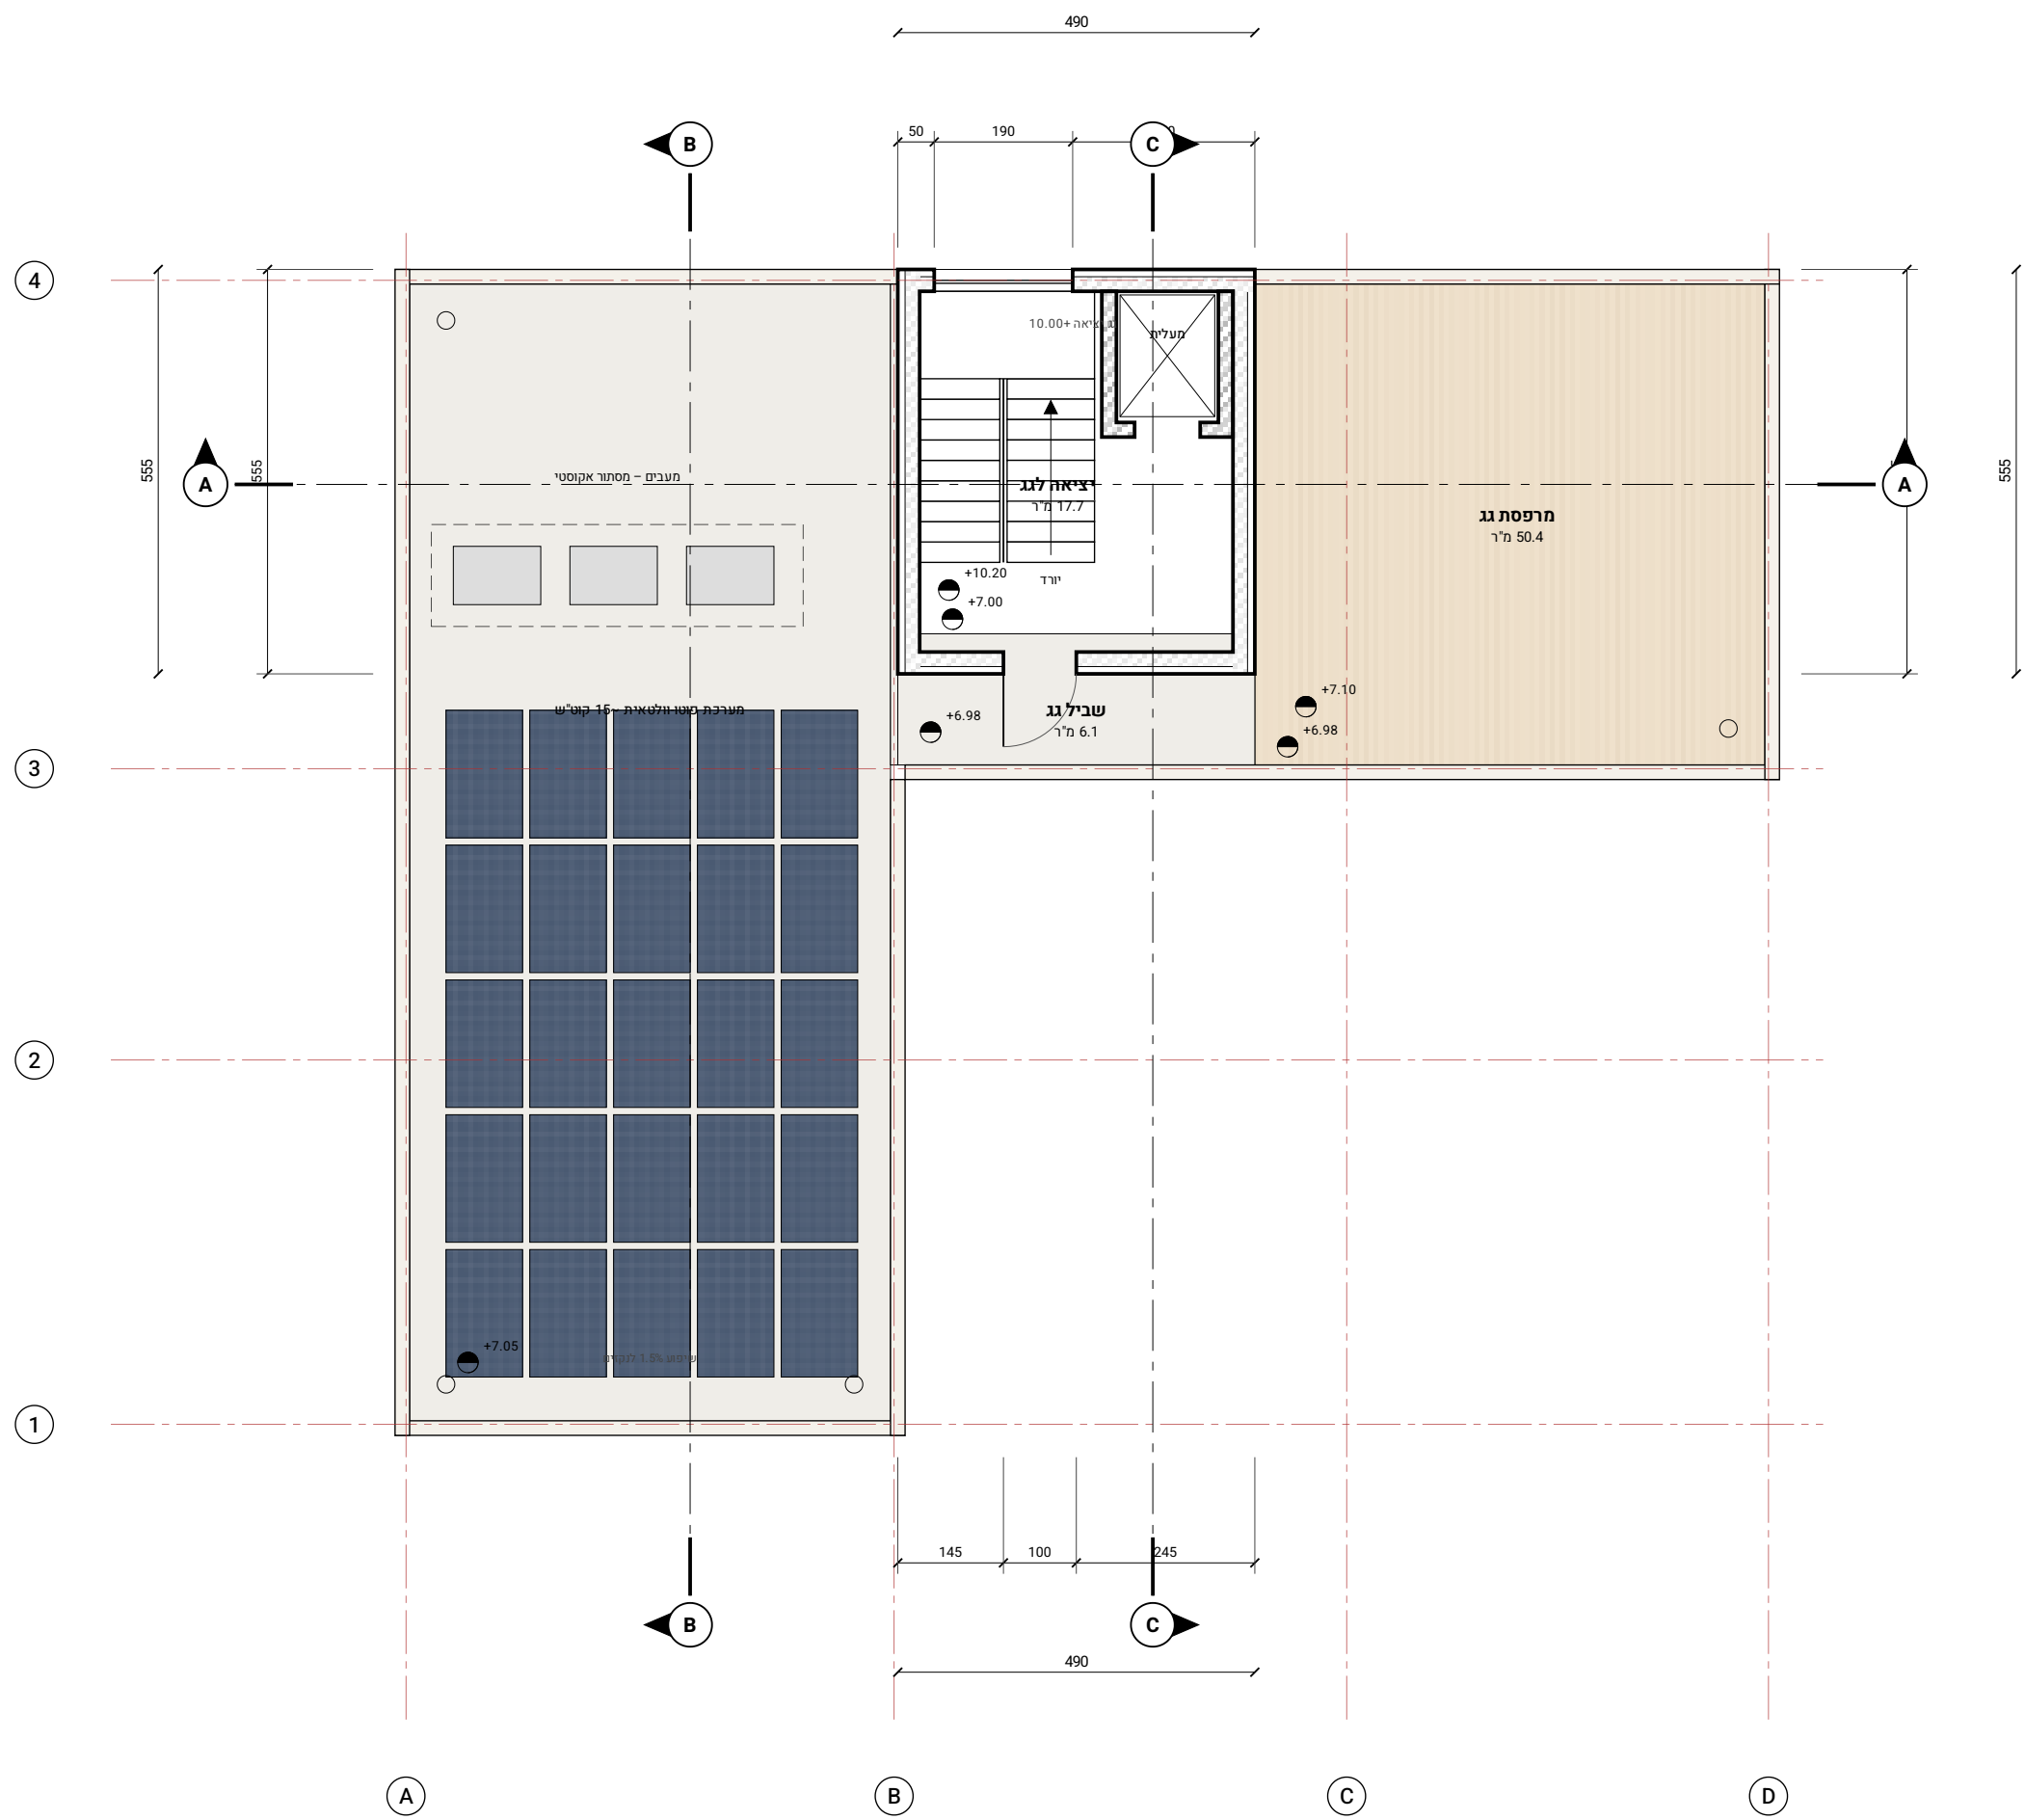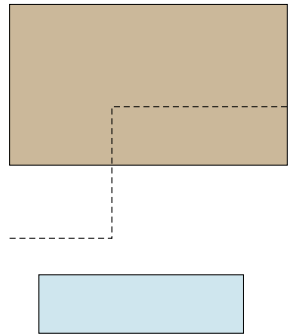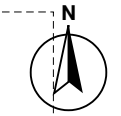

טבלת חללים - תכנית גג

מס'	חלל	שטח מ"ר	ריצוף	ג. תקרה
R1	ציאה לגג	17.7	פויצ'ן	3.00
R2	מחסן גג	50.4	דק עץ	-
R3	שכילוג	6.1	אריזי דק	-
	סה"כ פנים (נטו)	17.7		

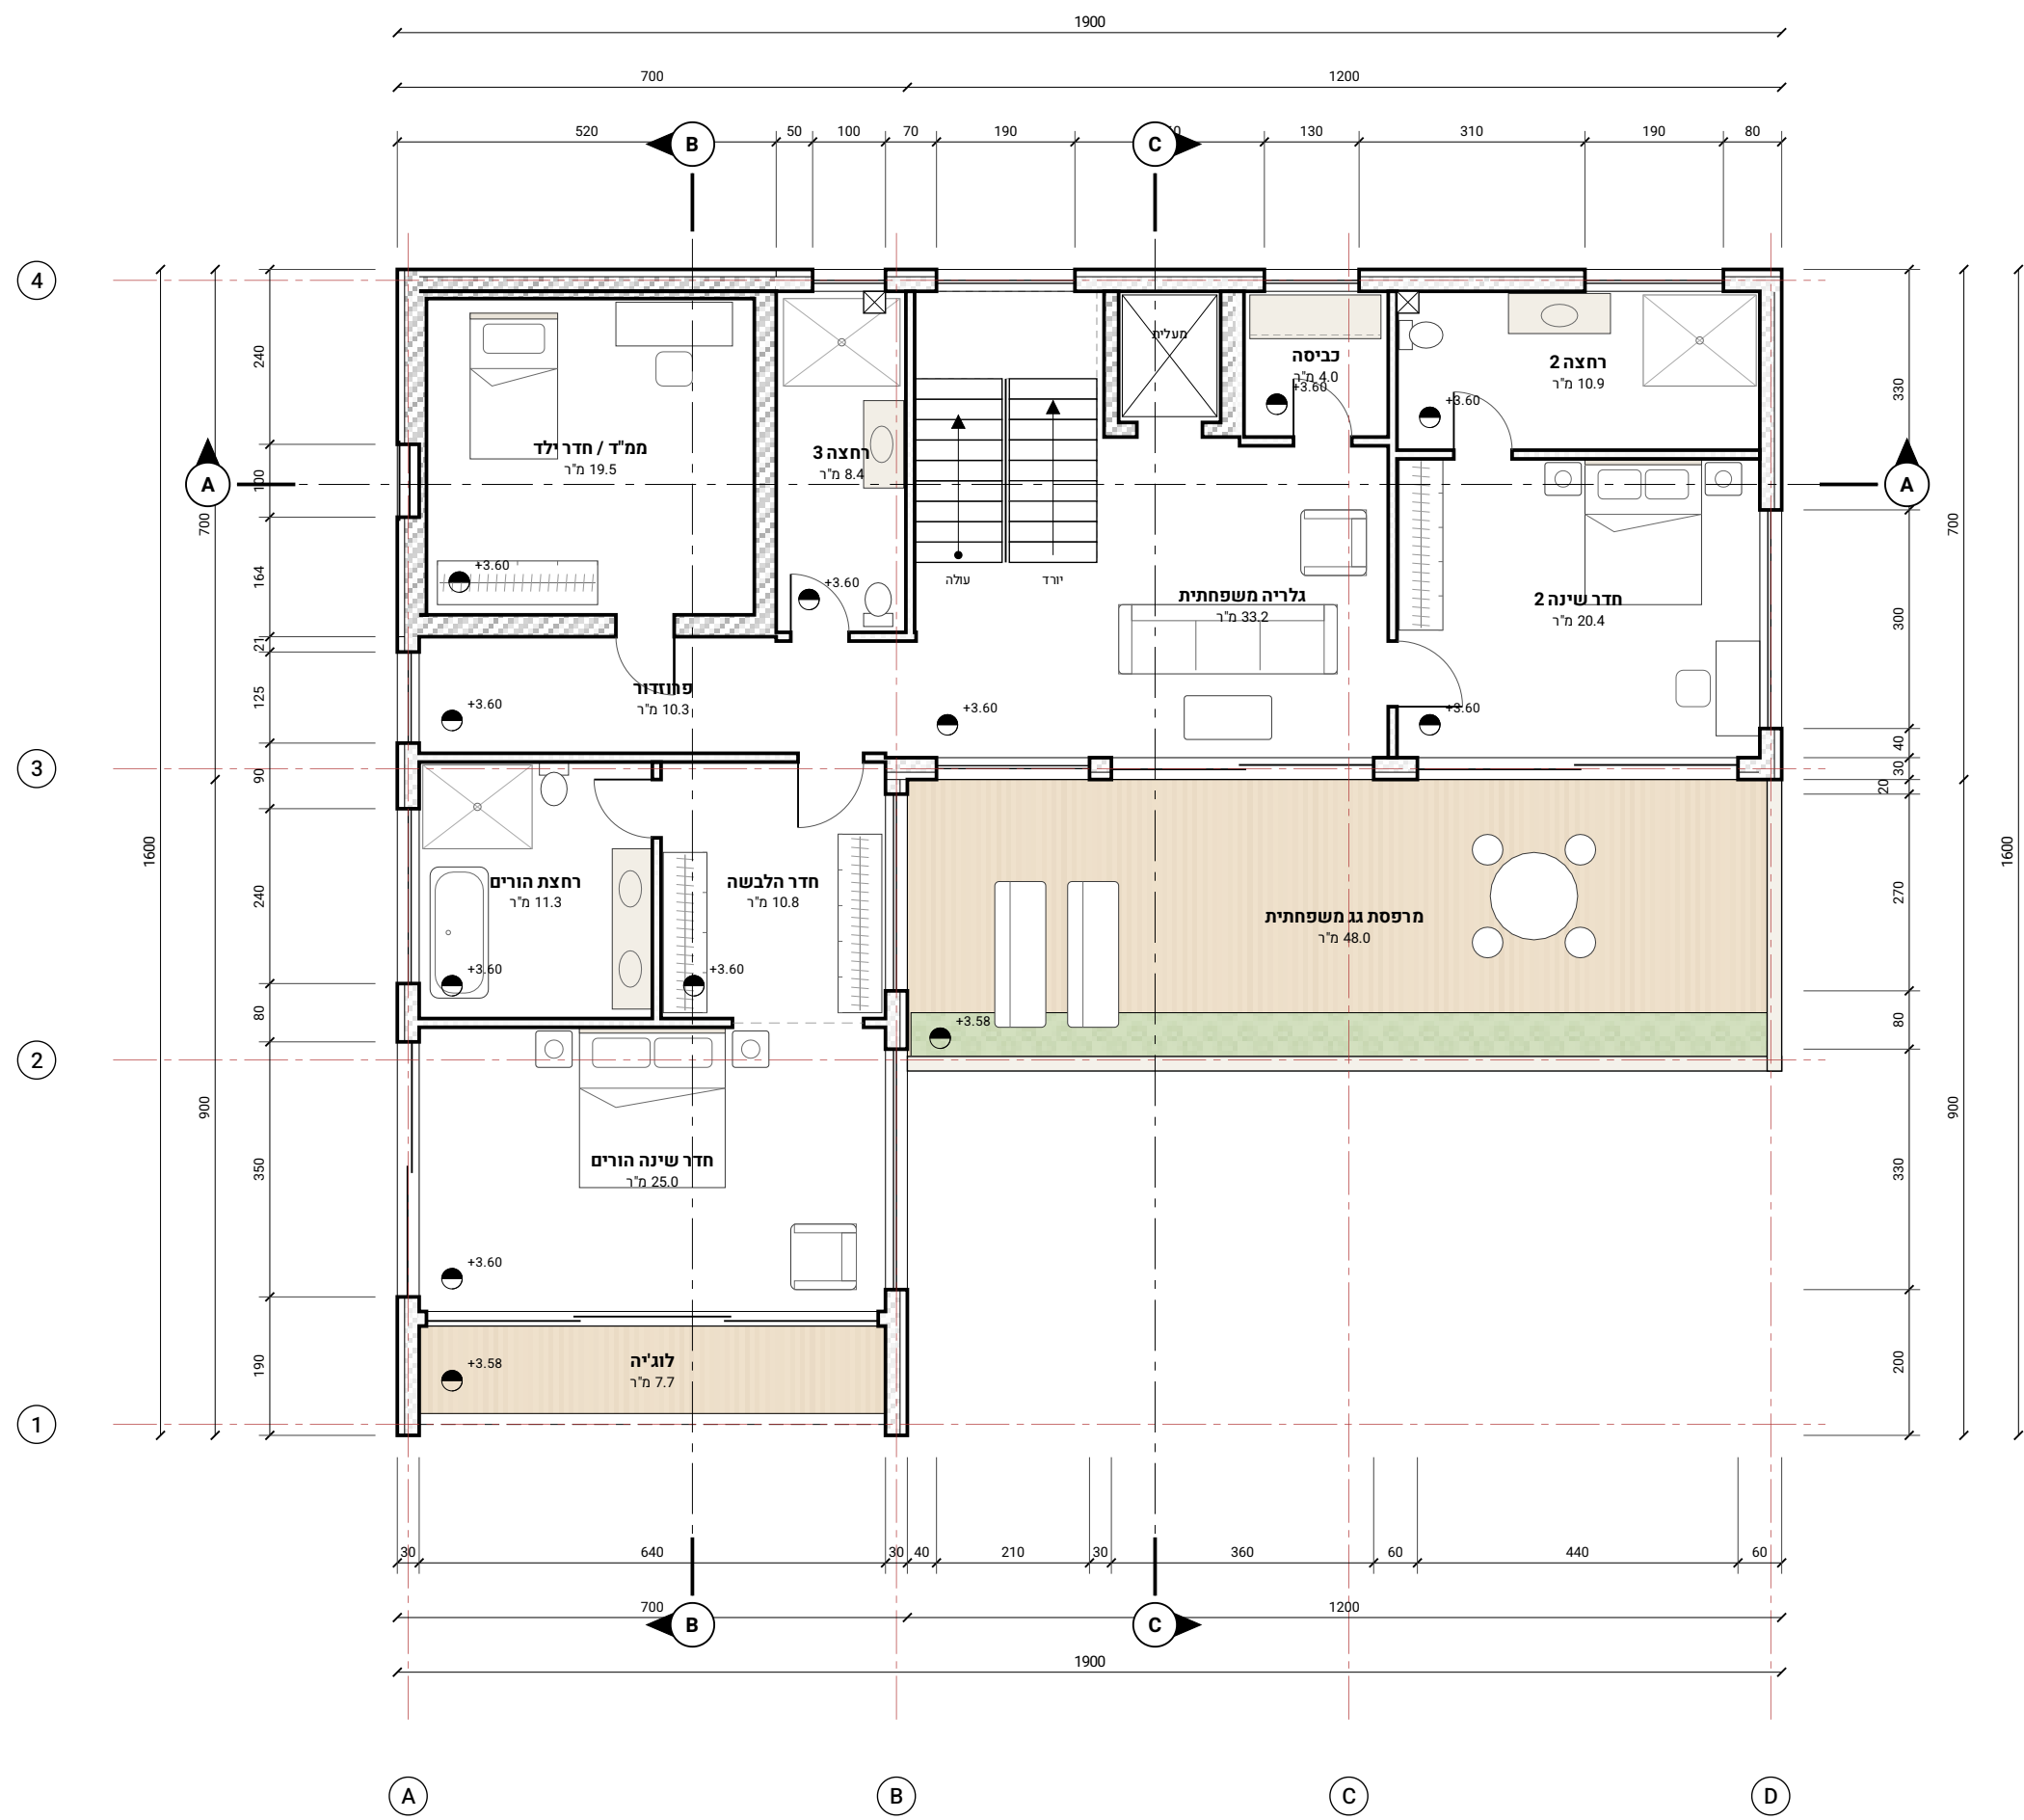

טבלת חללים - קומה א'

מס'	חלל	שטח מ"ר	ריצוף	ג. תקרה
U1	חדר שינה הורים	25.0	פרקט אלון	2.80
U2	לובי	7.7	דק עץ	-
U3	רוחצת הורים	11.3	אבן טבעית 60/120	2.70
U4	חדר הלבשה	10.8	פרקט אלון	2.70
U5	פרוזדור	10.3	פרקט אלון	2.70
U6	מס'ד / חדר ילד	19.5	פרקט אלון	2.60
U7	רוחצת 3	8.4	פויצ'ן 60/120	2.60
U8	גלריה משפחתית	33.2	פרקט אלון	2.80
U9	כביסה	4.0	פויצ'ן 60/60	2.60
U10	חדר שינה 2	20.4	פרקט אלון	2.80
U11	רוחצת 2	10.9	פויצ'ן 60/120	2.60
U12	מחסן גג משפחתית	48.0	דק עץ / אבן	-
	סה"כ פנים (נטו)	153.8		

תכנית גג

ק"מ 1:100

תכנית קומה א'

ק"מ 1:100

