



בית כורכר

BEIT KURKAR

שם הפרויקט:
וילת בוטיק בקיסריה

מיקום הפרויקט:
קיסריה, רובע 13 (מגרש לימודי)

מנהל:
שריק

שם הבניין:
סכמה סטטית

מס' בניין:
10

ק"מ:
1:100

רשימת ניליונות:




01	שער
02	קונסט ומחיר
03	ניתוח אזור וסביבה
04	תכנית העמדה וסכמת שטחים
05	תכנית פיתוח שטח
06	תכנית פרקט וקרקע
07	תכנית קומה א' וגג
08	חיתות
09	חיתות
10	סכמה סטטית
11	תכנית קומה א'
12	תכנית קומה ב'
13	חיתות
14	חיתות A-A
15	חיתות B-B
16	גיליון מדרגות
17	פרטי בניין
18	רשימת אלומיניום ונרות
19	עיצוב פנים - חלל המגורים
20	עיצוב ריהוט - אי המטבח
21	רשימת חוץ
22	רשימת פנים
23	חודה

מנהל:
הנדסאים - אדריכלות ועיצוב פנים

שם המעשה/ת.ד.:


תאריך:

10.2026

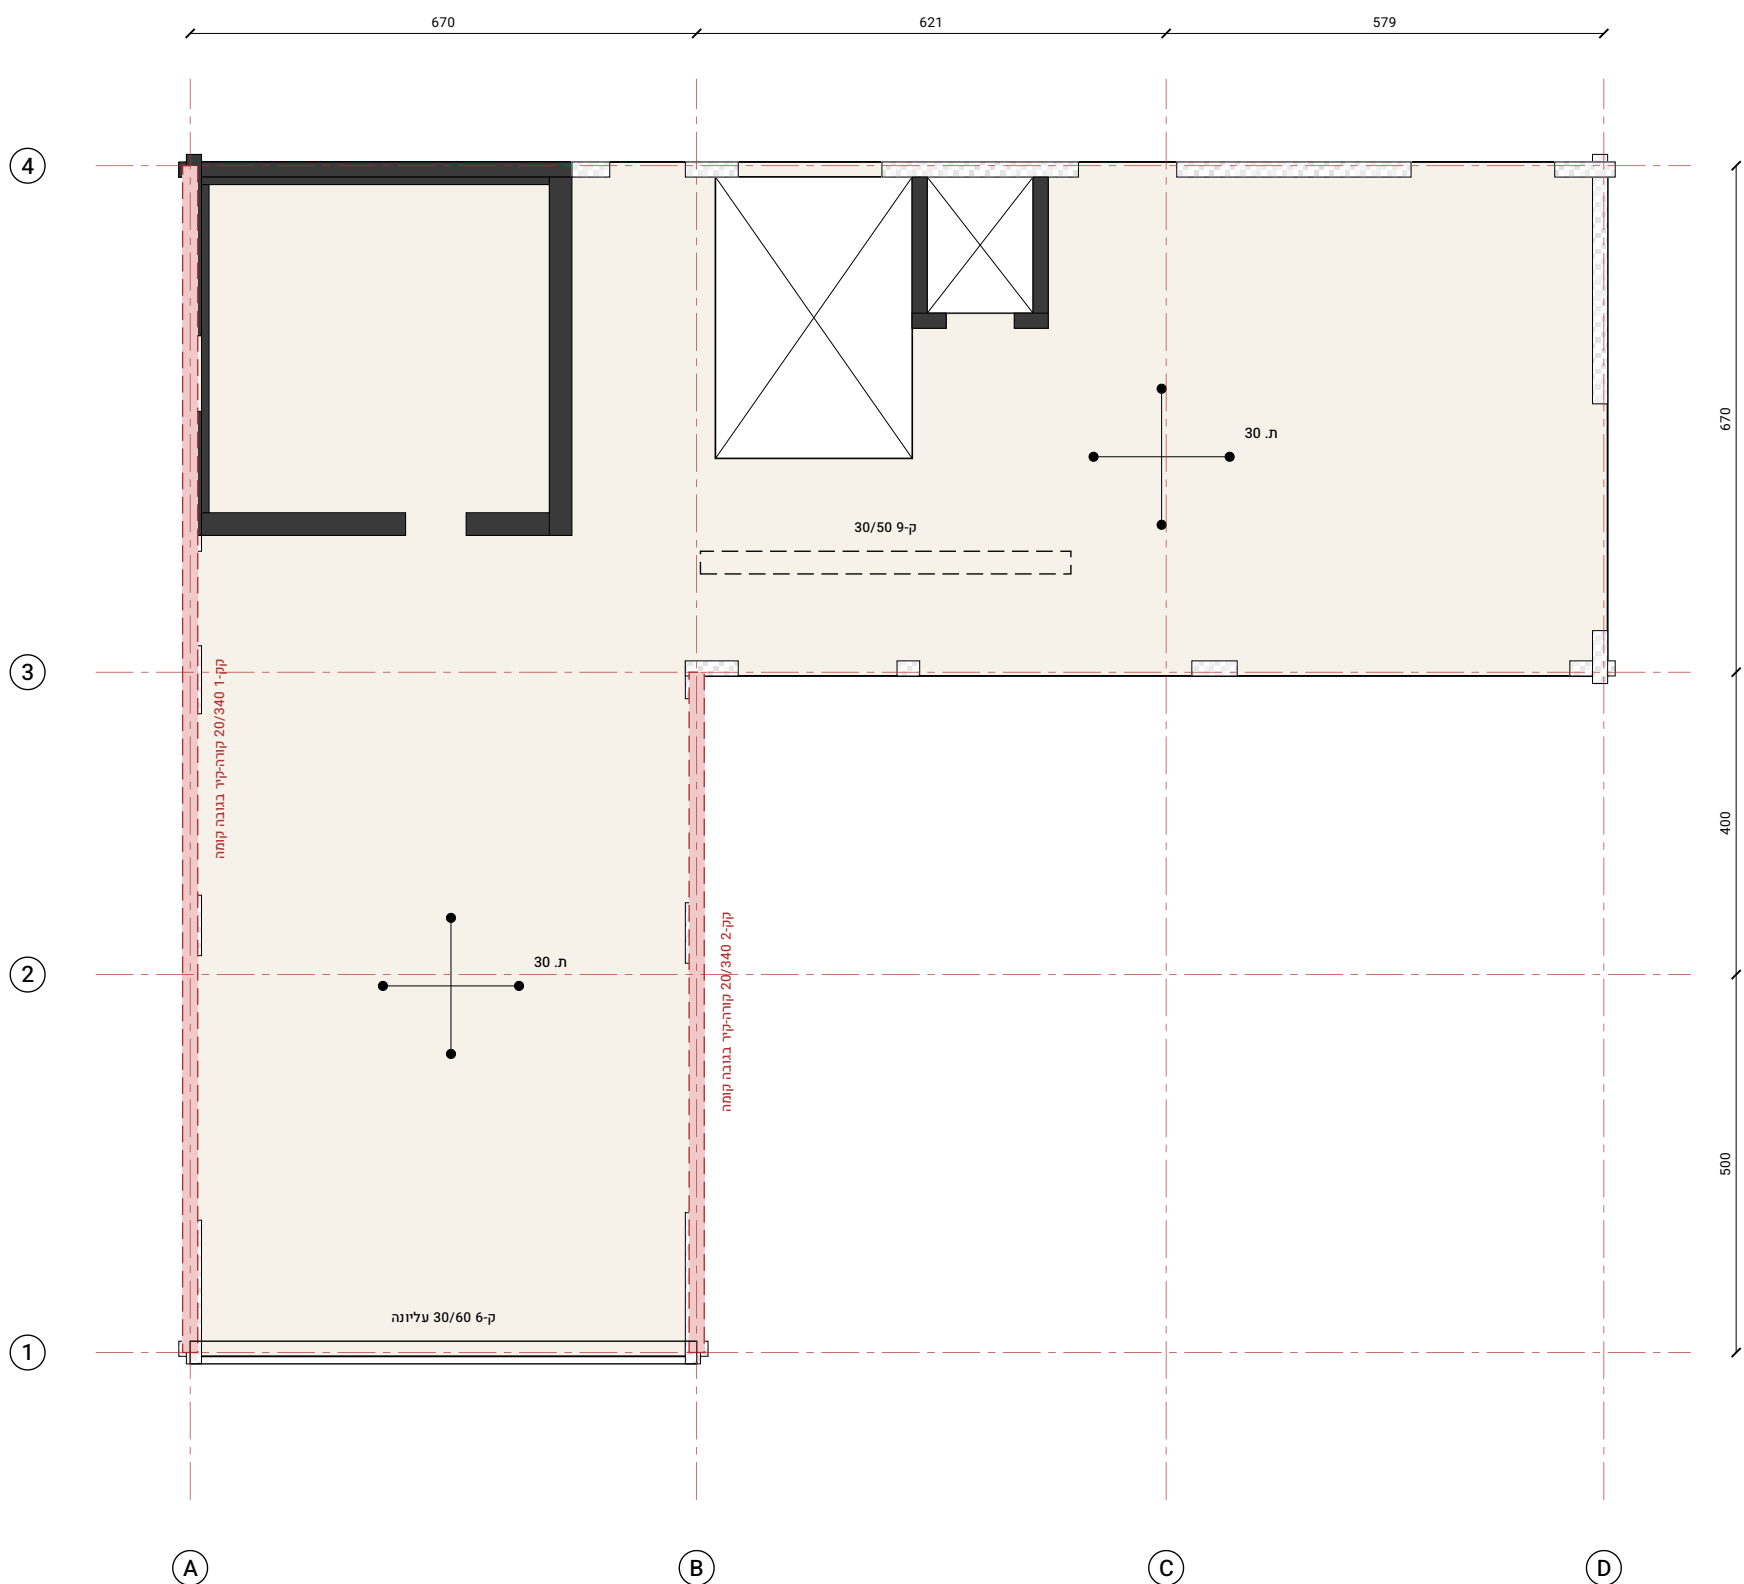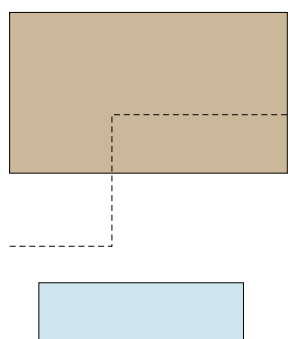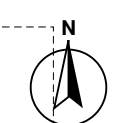


סכמה סטטית תקרה +7.00

ק"מ 1:100

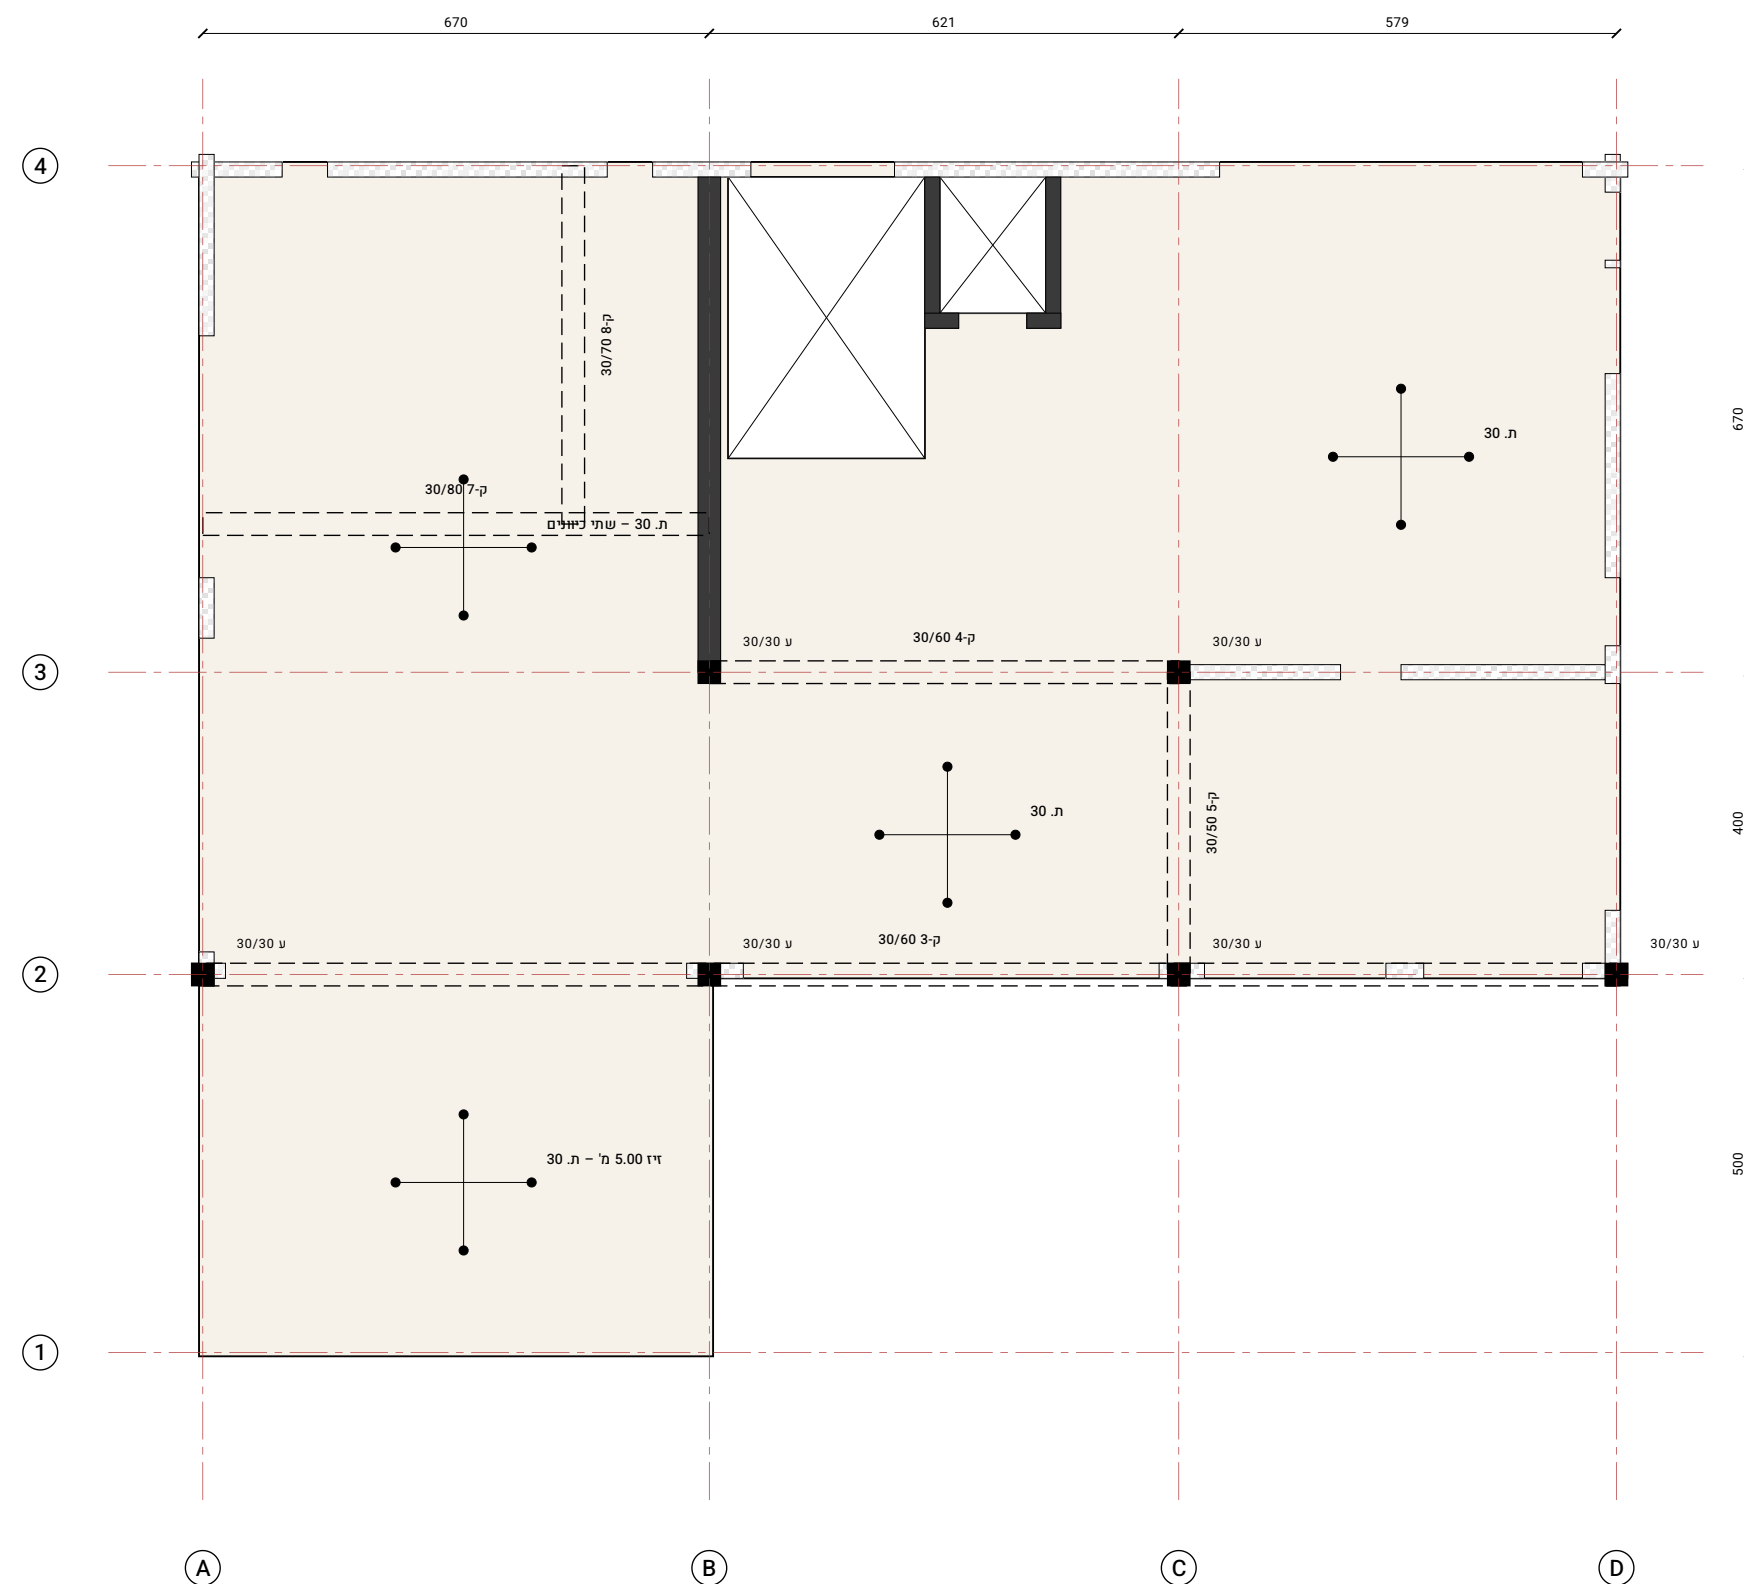

סכמה סטטית תקרה +3.60

ק"מ 1:100

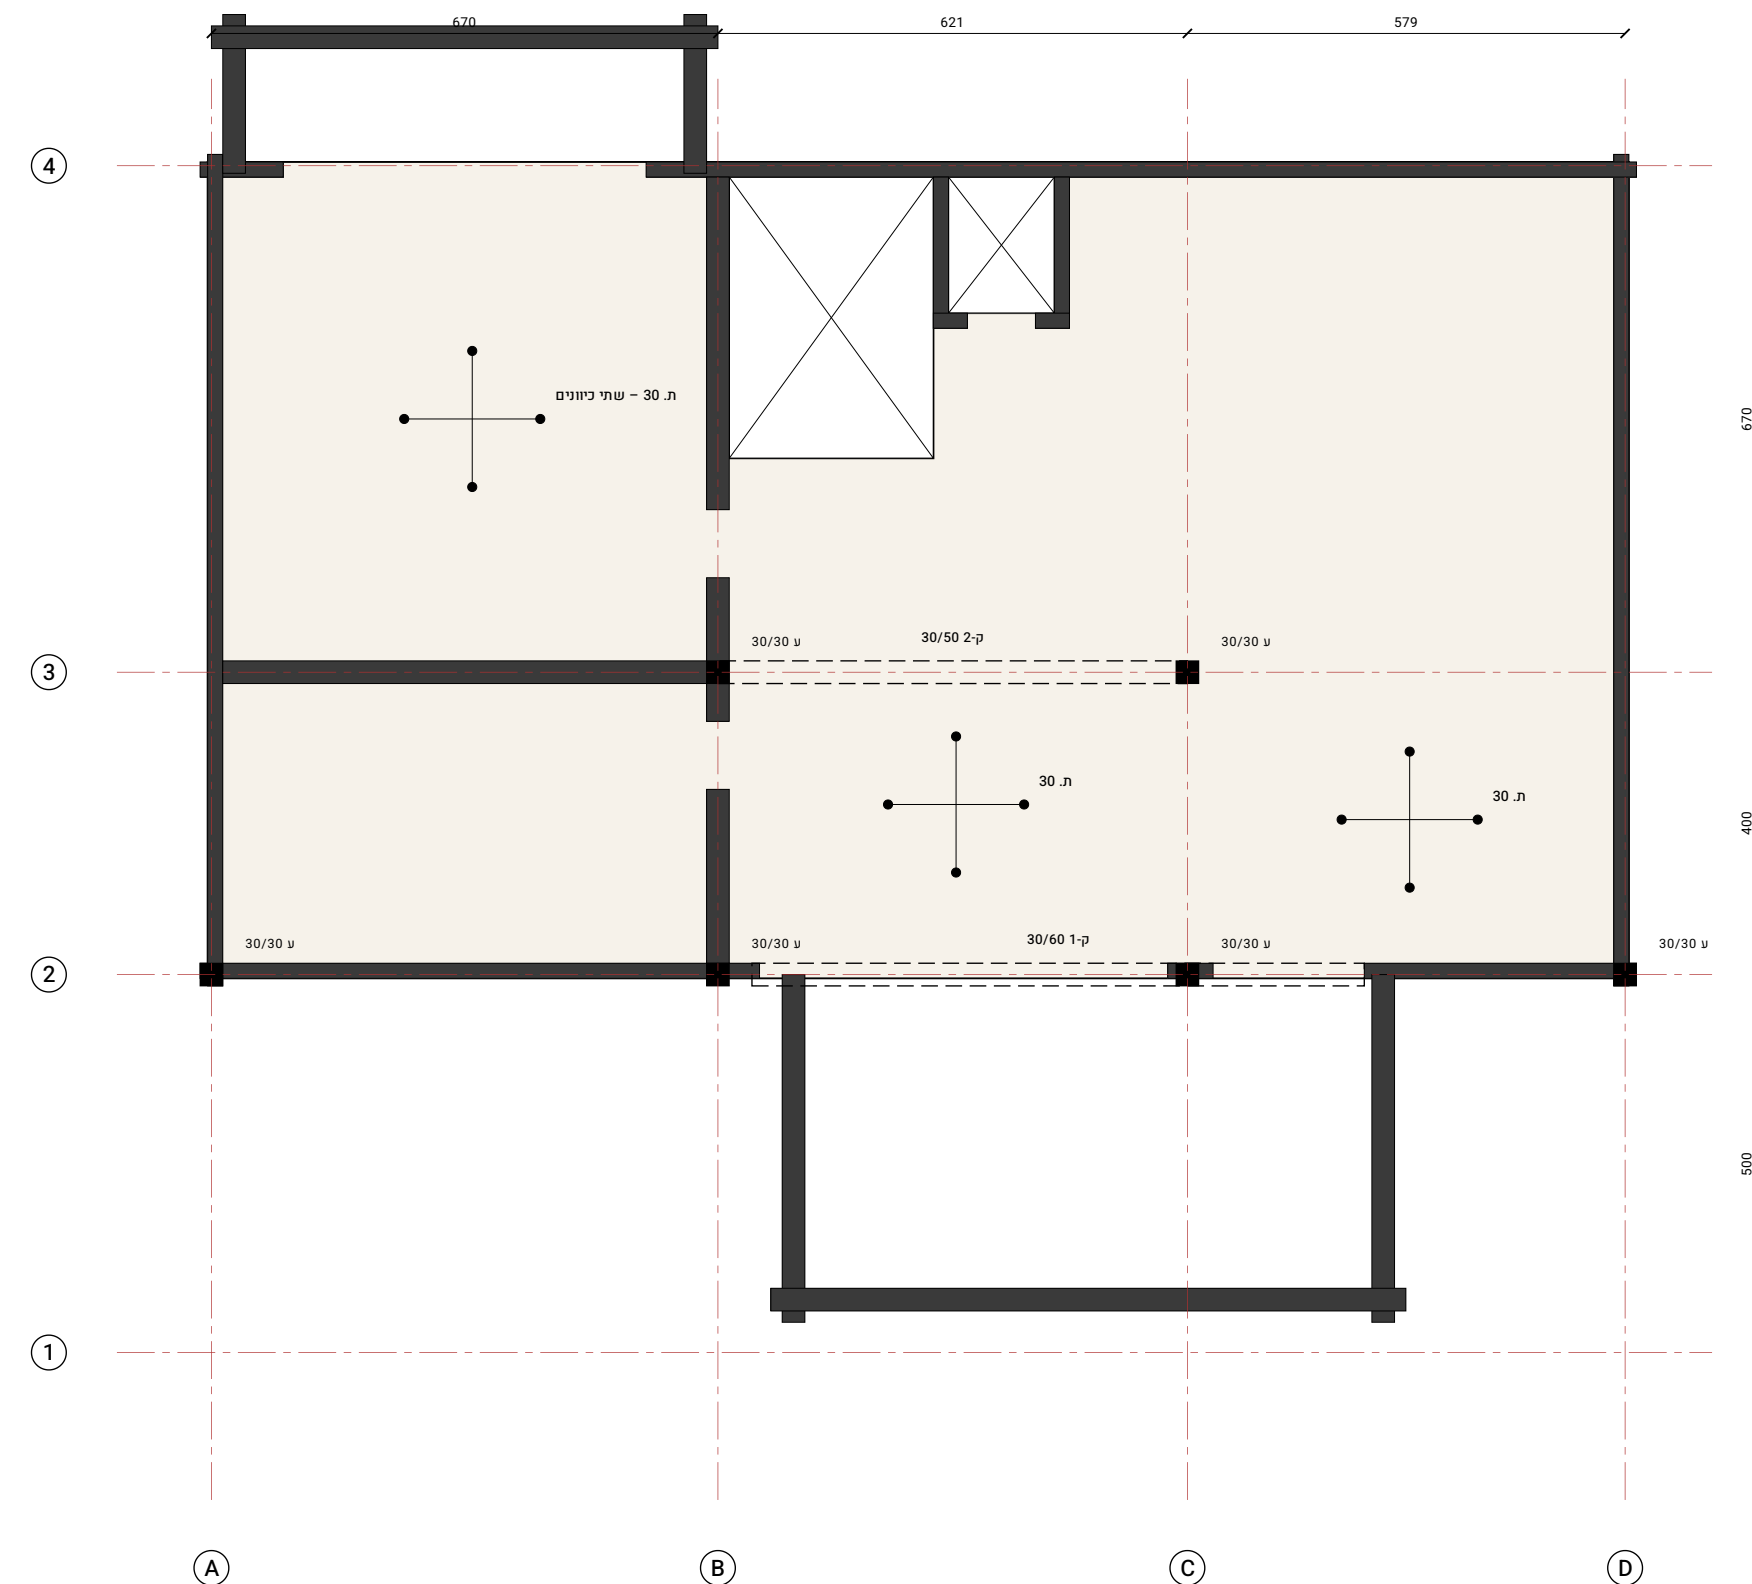

סכמה סטטית תקרה ±0.00


ק"מ 1:100

מקרא:

- קיר בטון מזוין נושא (קירות מחך, פיר מעלית, ממ"ד, קיר ג"ק)
- קיר בלוק נושא 20
- עמוד ב"מ 30/30
- קורה תחתונה (ק-אא רוחב/גובה ס"מ)
- קורה-קיר בגובה קומה - נושאת את חוץ
- תקרה ב"מ מלאה ת. 30


עקרונות המערכת הקונסטרוקטיבית:

- שילד בטון מזוין וזיבן באתר: רפסודה 50, קירות תמך 30, תקרות מלאות 30.
- זיבן הדומי (מ 5.00) יישא ע"י שני קירות-קורה בגובה קומה (קק-1, קק-2).
- הפועלים כקורות בגובה 3.40 מ' וממשיכים 10.7 מ' לאחר עד ציר 4 - יחס עונן 1.2.
- קיר הליבה (פיר מעלית) + קיר האון משמש קיר ביירה לנחוצות אופקיים (מ"י 413).
- יכסיו בטון מוגבר 5-4 ס"מ ובטון ב-40 לסביבה יחית (מ"י 466).
- כל המידות והזינוקים לפי חישוב סטטי של מהנדס הקונסטרוקציה.

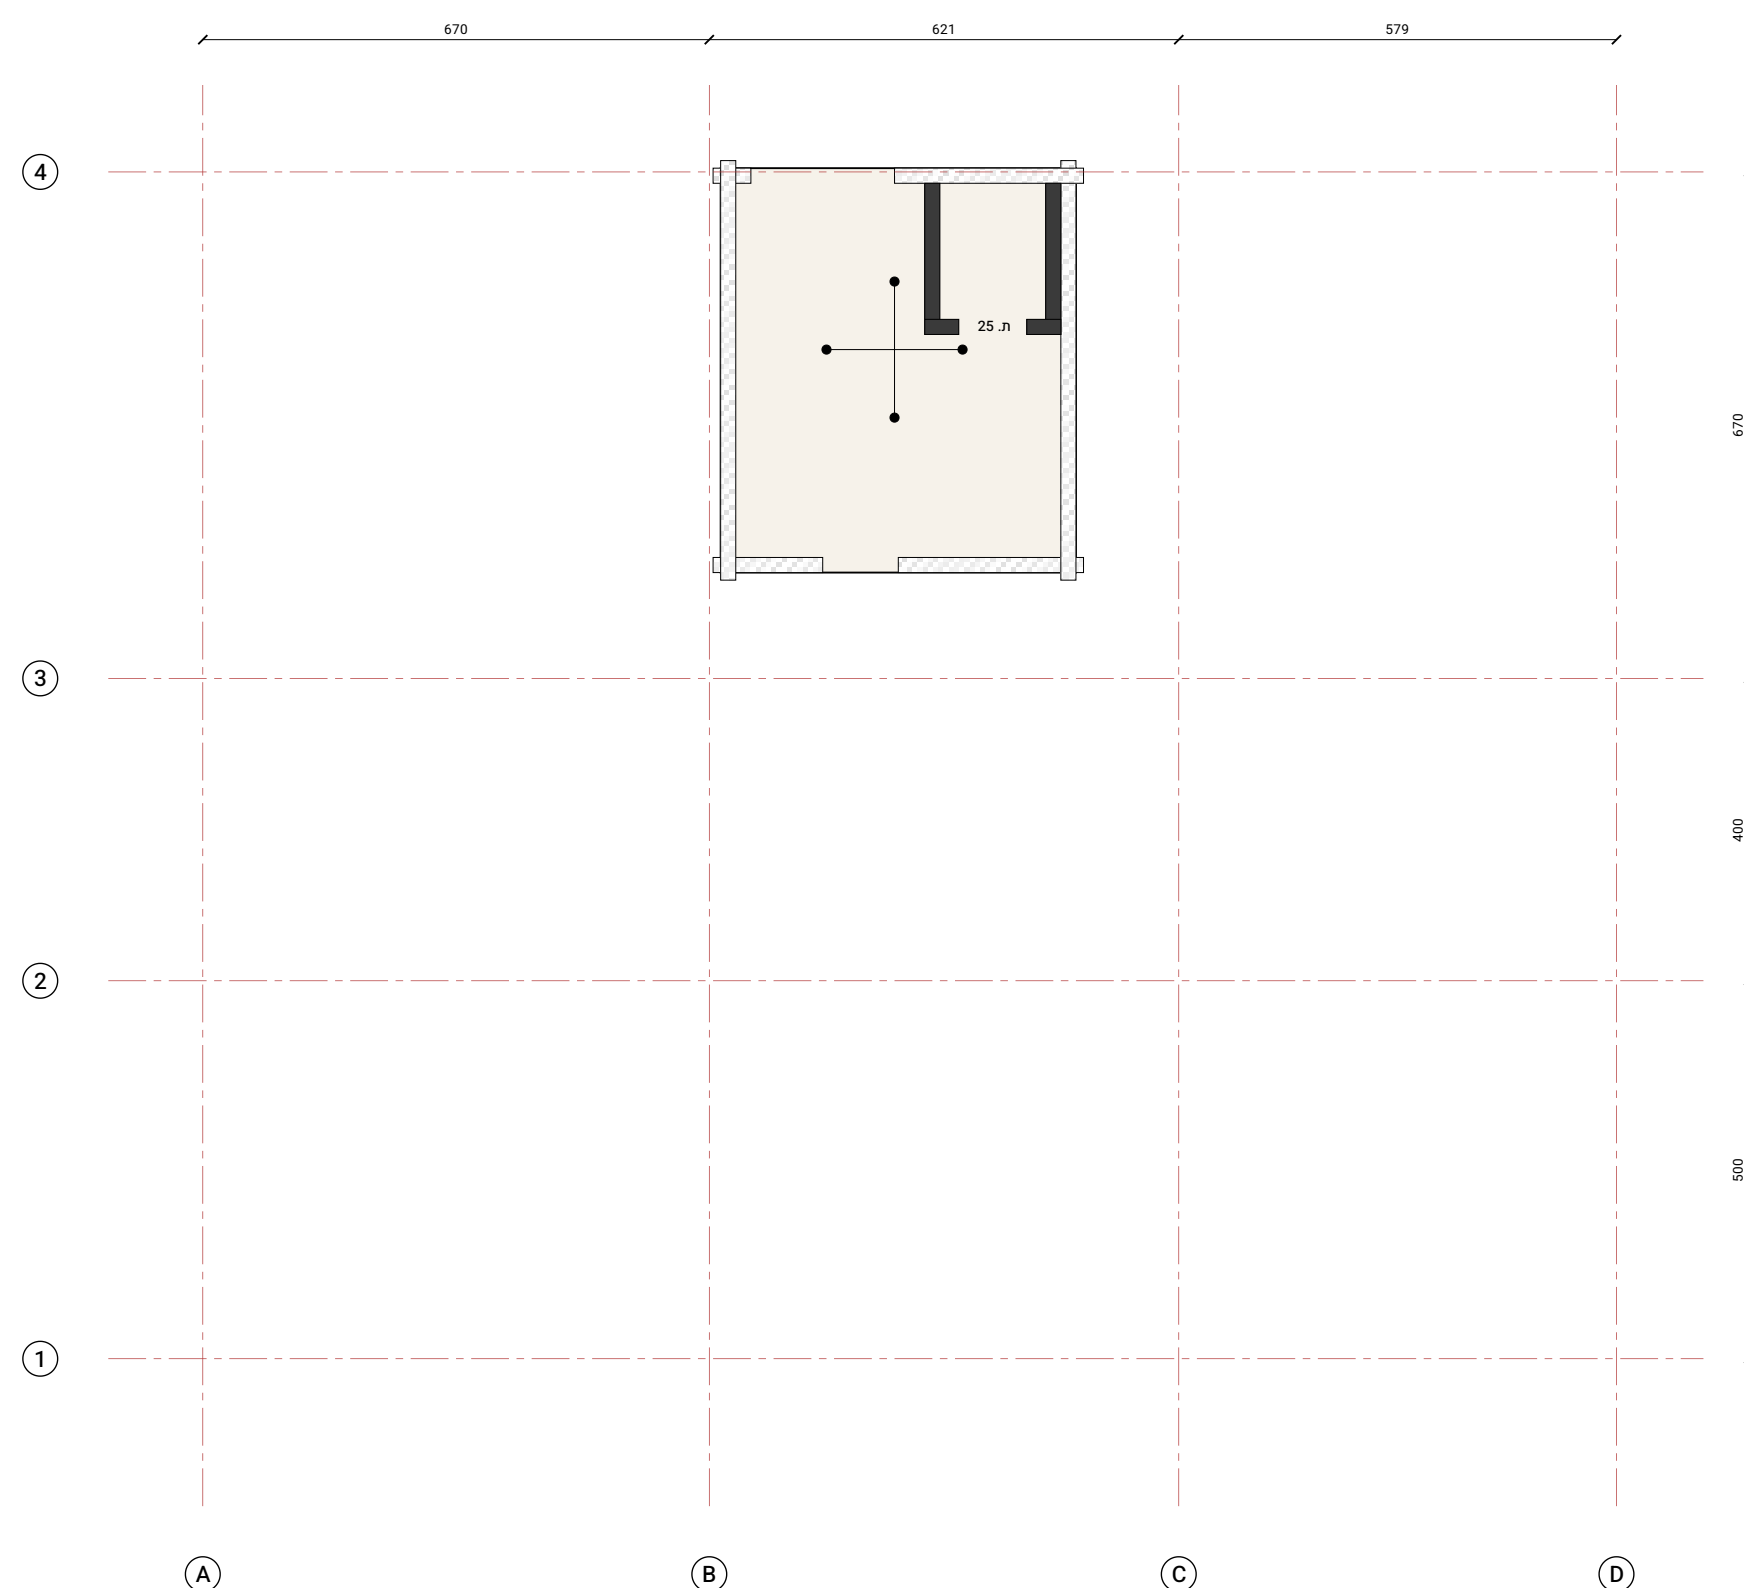

סכמה סטטית תקרה +9.80

ק"מ 1:100

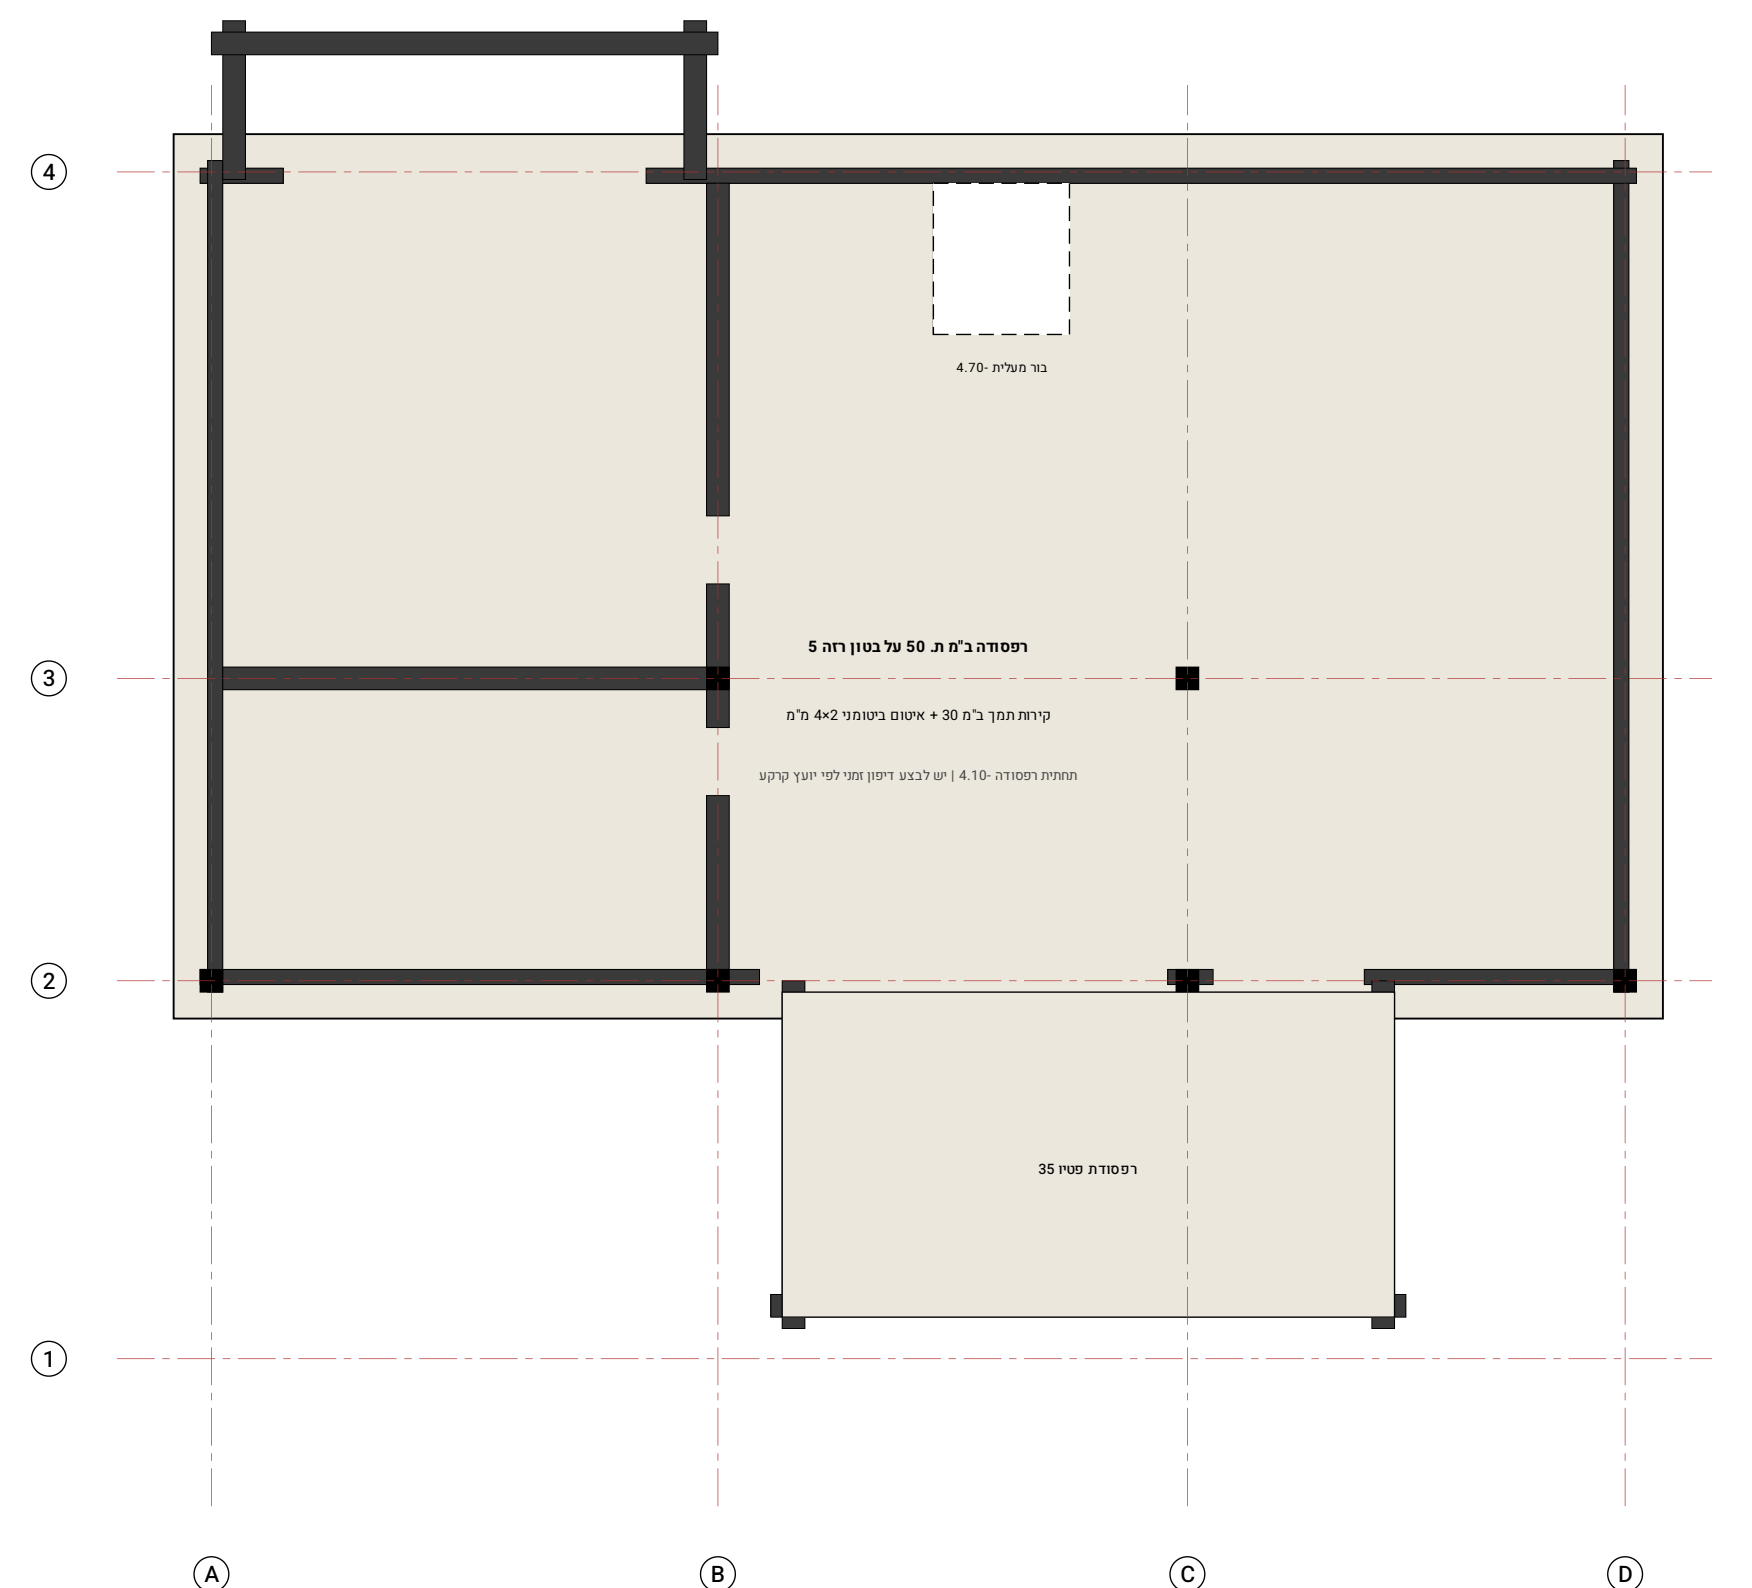

תכנית יסודות - רפסודה

ק"מ 1:100