

בית כורכר



שם הפרויקט:

וילת בוטיק בקיסריה

מיקום הפרויקט:

קיסריה, רובע 13 (מגרש לימודי)

מנהל:

שירן שריקי

שם הבניין:

תכנית קומת קרקע

חסי גריליון: 11

ק"מ: 1:50

רשימת ניליונות:

01	שער
02	קונסטרוקציה ומחבר
03	ניתוח אדריכלי וסביבה
04	תכנית העמדה וסלול שטחים
05	תכנית פיתוח שטח
06	תכנית פרק קרקע
07	תכנית קומה א' וגג
08	חיתות
09	חיתות
10	פרסומים פוטנציות
11	תכנית קומת קרקע
12	תכנית קומה א'
13	חיתות
14	חיתות A-A
15	חיתות B-B
16	גיליון מדרגות
17	פרטי בניין
18	רשימת אלמנטים וגזרות
19	עיצוב פנים - חלל המגורים
20	עיצוב ריהוט - אי המטבח
21	גרמיות חוץ
22	גרמיות פנים
23	תודה




מנהל:

הנדסאים - אדריכלות ועיצוב פנים

שם המעשה/תחל:


תאריך:

10.2026

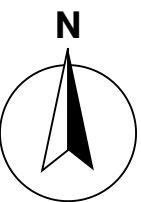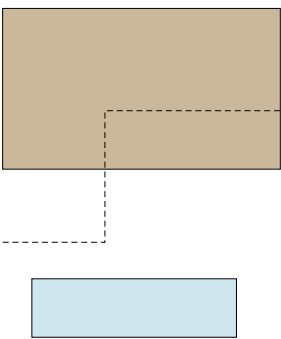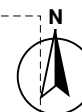

הערות כלליות:

- המידות בס"מ, המפלסים במטרים, ±0.00 = מעל פני הים.
- קירות חוץ בלבד בסטן 20 + ביזוז חצר סרטנים 5 + חיפוי אבן/טיח חומי.
- קירות פנים בלבד, 10 מטריון / גבס דו-צדדי לפי סיסטון.
- כל מידות הפתחים לפי דרישה או שינוי בשטח לפני יציאה.
- מפלס לפי הנחיות פיקוד העורף - קירות ותקרה בסטן 30.
- אלמנטים פורפיל חומי, צבע תנור דרזת, ידענו בידוד Low-E.

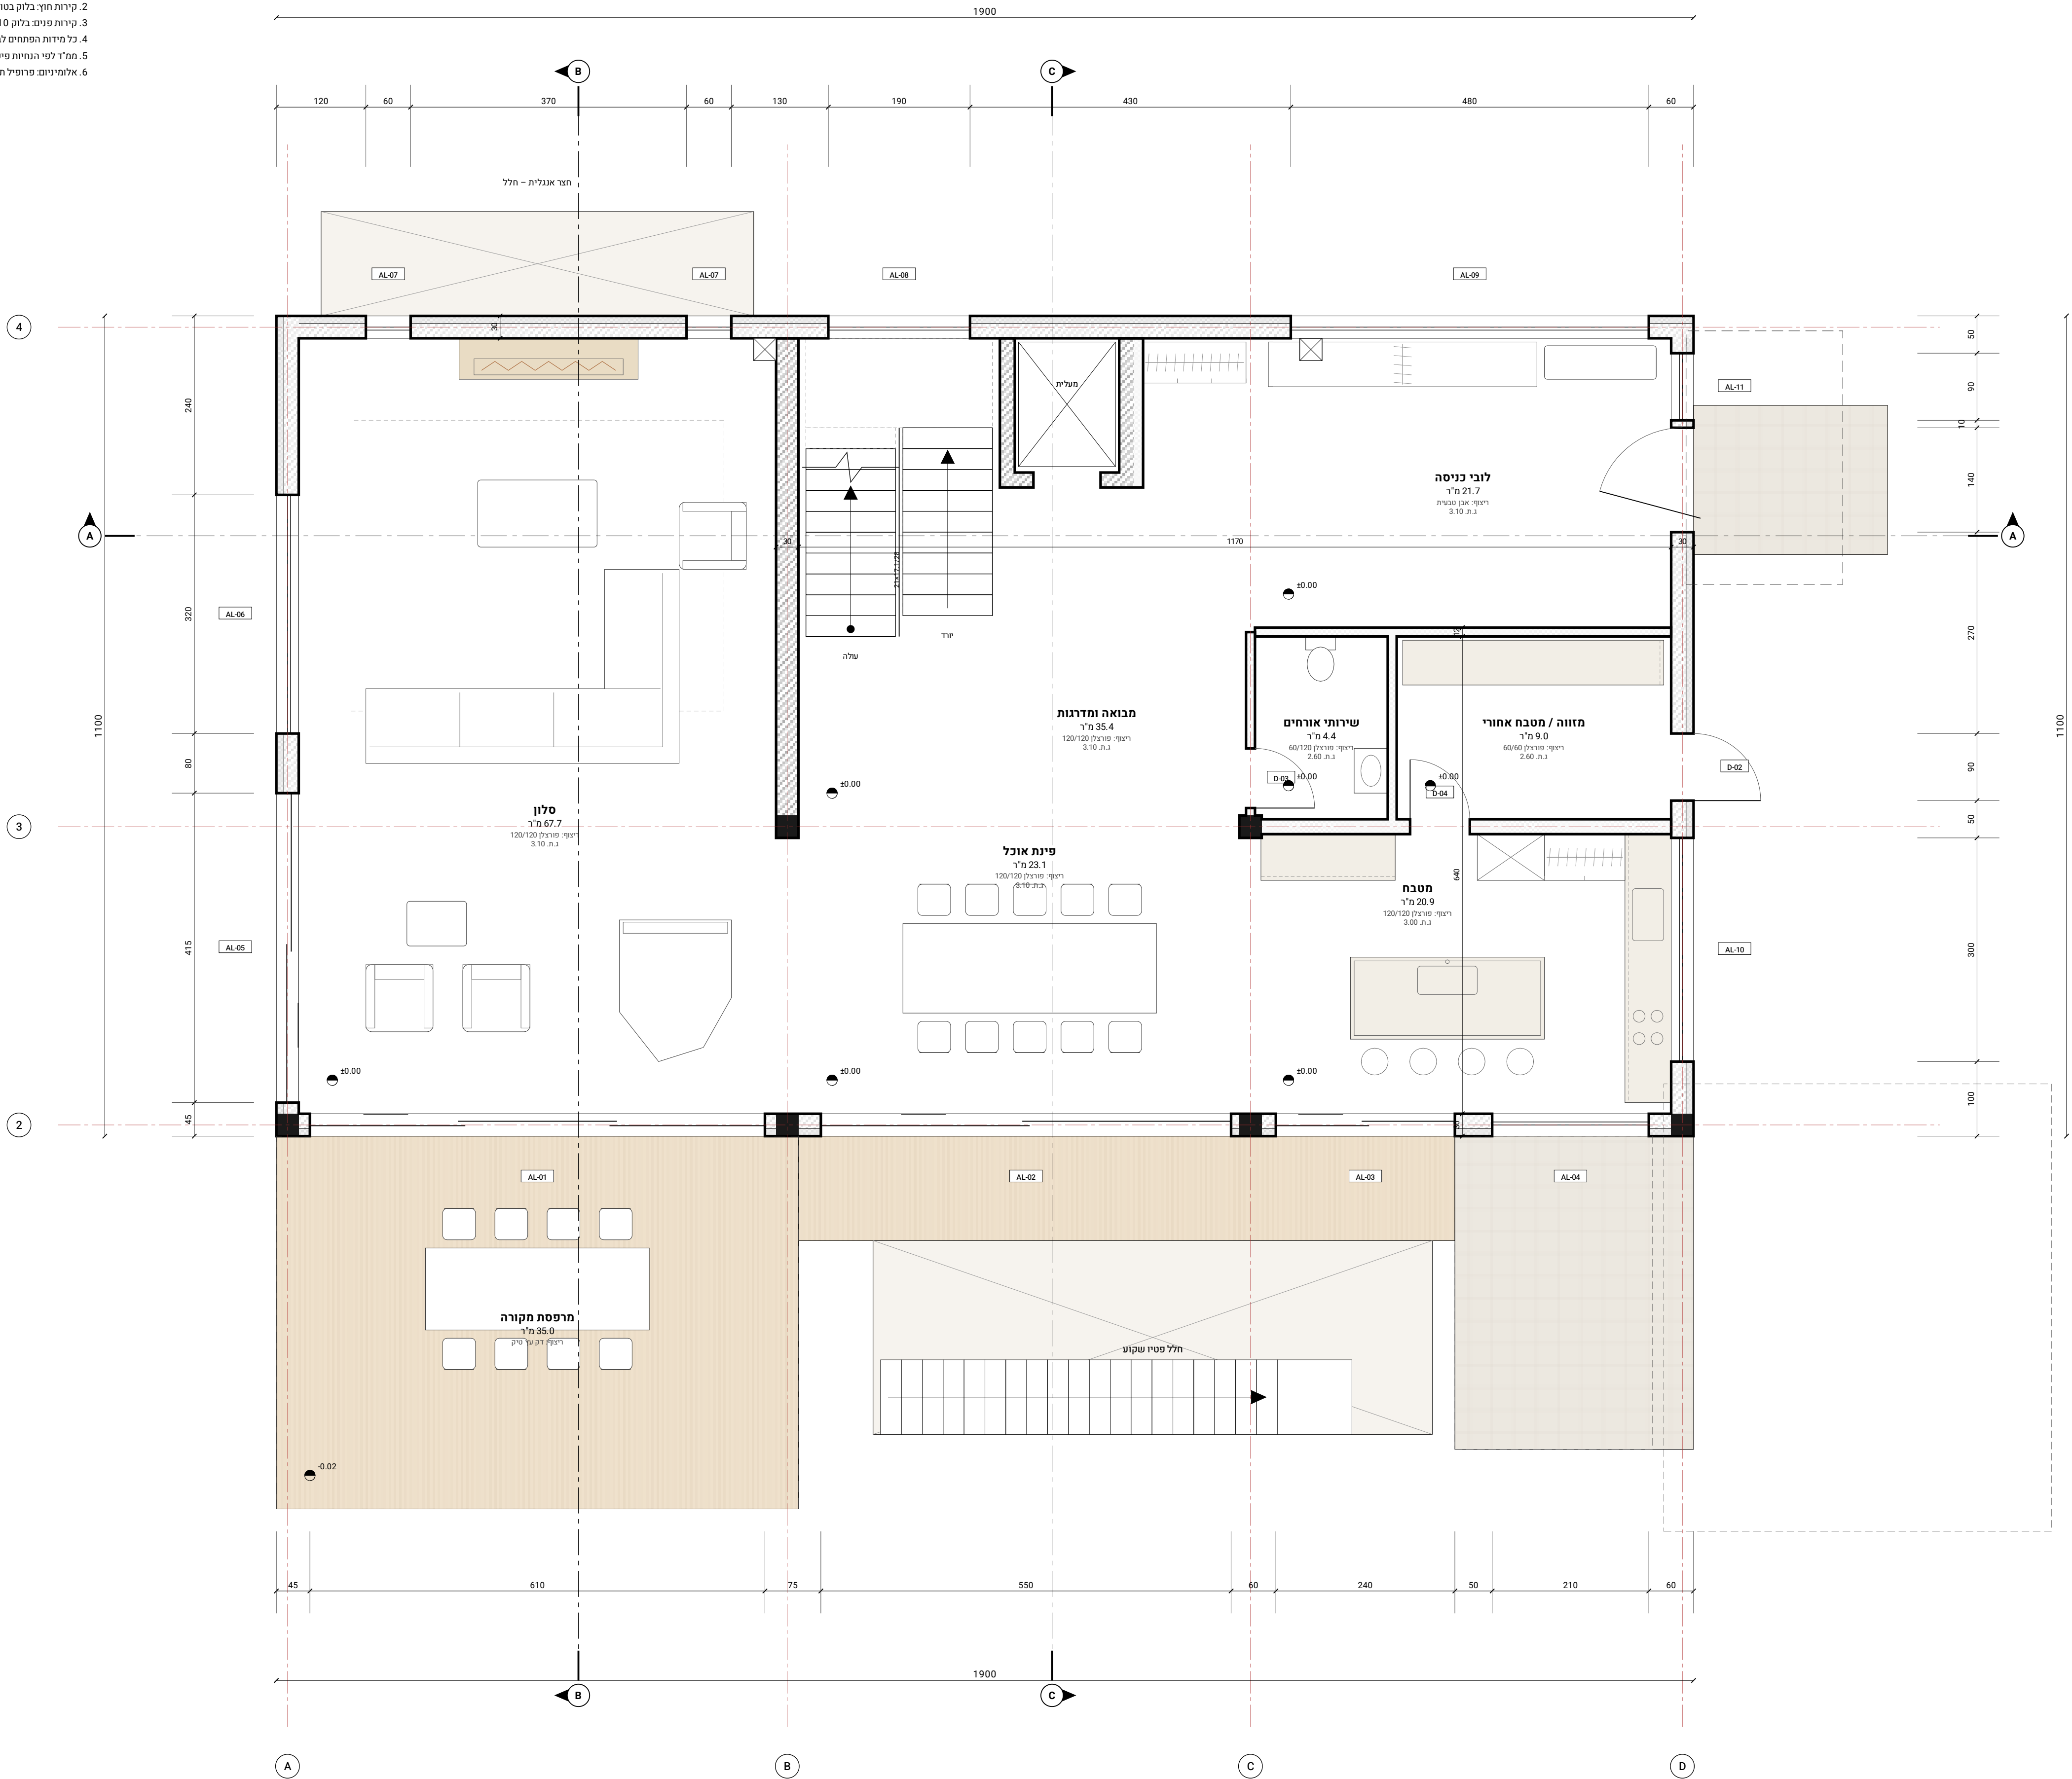

תכנית קומת קרקע

קנ"מ 1:50

