


בית כורכר

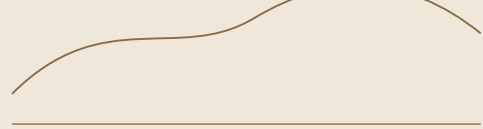

שם הפרויקט:

וילת בוטיק בקיסריה

מיקום הפרויקט:

קיסריה, רובע 13 (מגרש לימודי)

מנהל:

שירן שריקי

שם הבניין:

תכנית קומה א'

חסי גרילוק:

12

ק"מ:

1:50

רשימת נילוחות:

01 שער

02 קונסטרוקציה וחלקי

03 ניתוח אזור וסביבה

04 תכנית העמדה וסלול שטחים

05 תכנית פיתוח שטח

06 תכנית פרק קרקע

07 תכנית קומה א' ונג

08 חיתות

09 חתכים

10 סכמות טכניות

11 תכנית קומת קרקע

12 תכנית קומה א'

13 חיתות

14 חתך A-A

15 חתך B-B

16 נילון מדרגות

17 פרטי בניין

18 רשימת אלומיניום וגזרות

19 עיצוב פנים - חלל המגורים

20 עיצוב ריהוט - אי המטבח

21 דרימות חוץ

22 דרימות פנים

23 חודה

מנהל:

הנדסים - אדריכלות ועיצוב פנים

שם המעשה/ת.ד.:

תאריך:

10.2026

תאריך:

10.2026

הערות כלליות:

1. המידות בט"מ, המפלסים במטרים, $\pm 0.00 = 18.50$ מעל פני הים.


2. קירות חוץ: בלוק בטון 20 + בידוד חיצוני 5 ס"מ + חיפוי אבן/טיח חיצוני.

3. קירות פנים: בלוק 10 משיח / גבס דו-צדדי לפי סיסטון.

4. כל מידות הפתחים לבדיקה ואישור בטמח לפני יצוא.

5. מ"ד לפי הנחיות פיקוד העורף - קירות ותקרה בטון מזוין 30.

6. אלמנטים פורפיל חומי, צבע תנור דרזת ים, זיגוג בידודי Low-E.

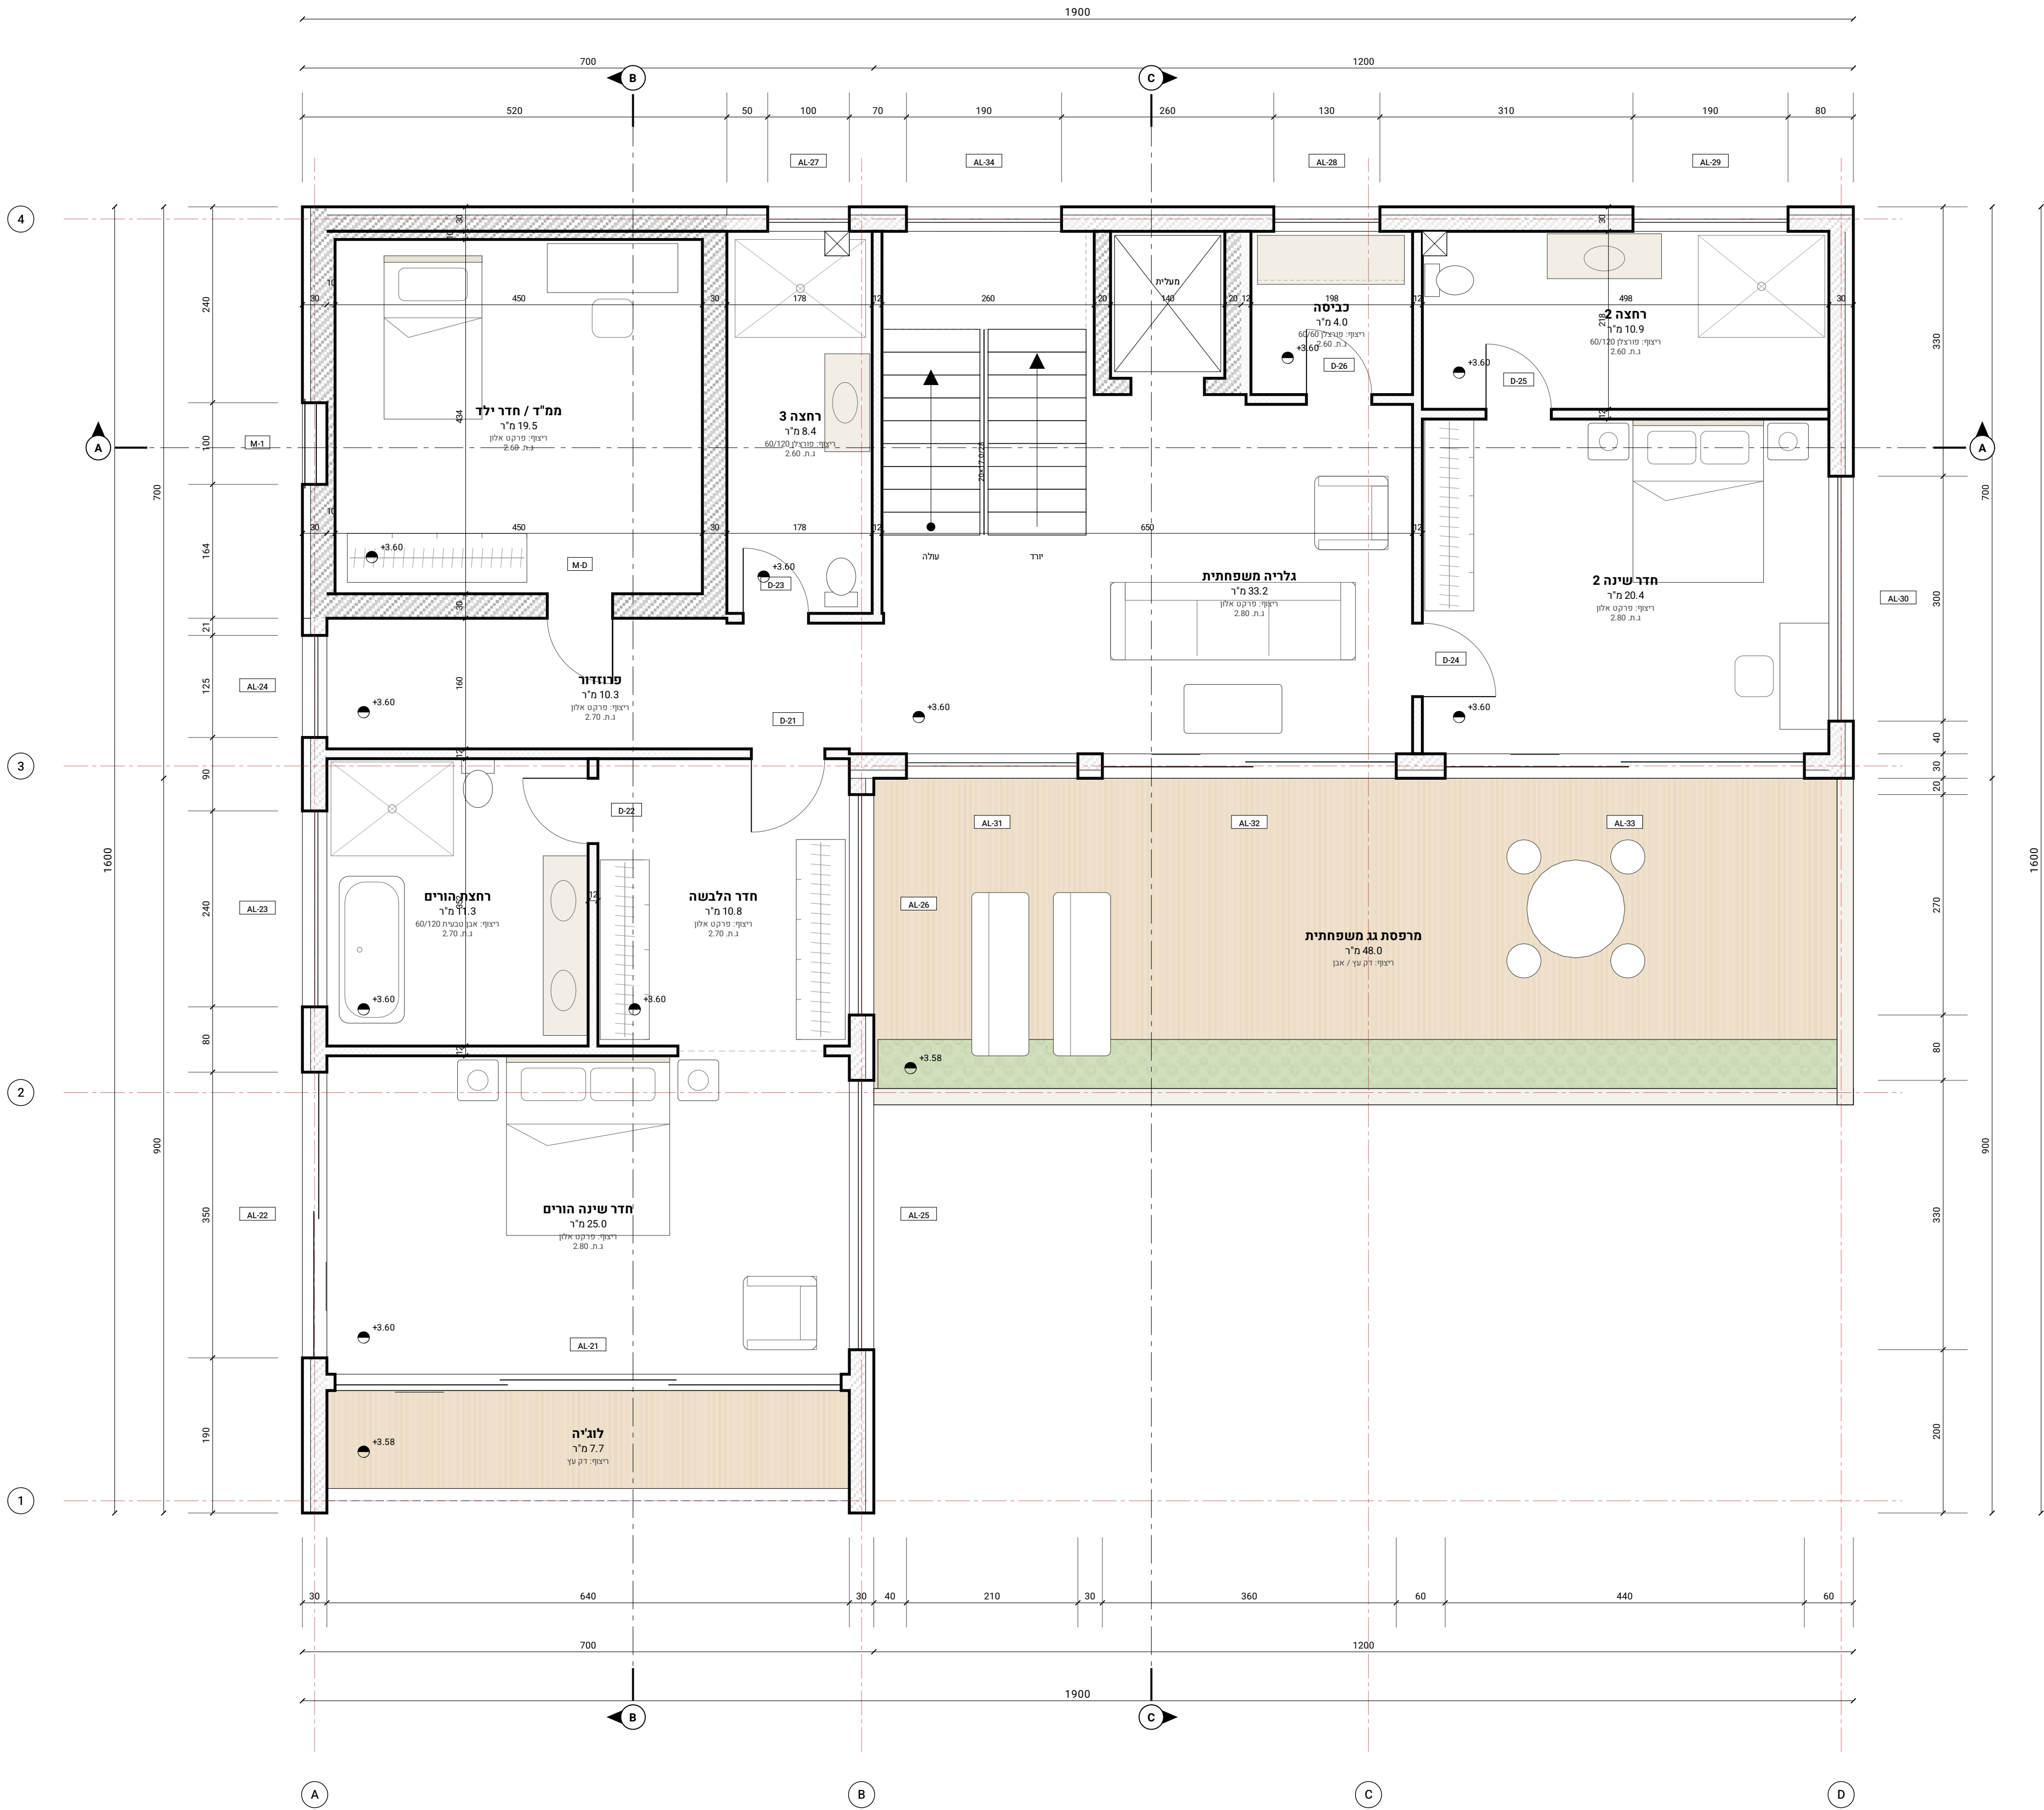

תכנית קומה א'

קנ"מ 1:50

0 1 2 3 4 5 מ'