בית כורכר

BEIT KURKAR

שם הפרויקט:
וילת בוטיק בקיסריה

מיקום הפרויקט:
קיסריה, רובע 13 (מגרש לימודי)

מנחה:
שירן שריקי

שם הגיליון:
גיליון מדרגות

מס' גיליון: **16**
קנ"מ: 1:25, 1:5

רשימת גיליונות:

01	שער	
02	קונספט ומחקר	
03	ניתוח אתר וסביבה	
04	תכנית העמדה וטבלת שטחים	1:200
05	תכנית פיתוח שטח	1:100
06	תכניות מרתף וקרקע	1:100
07	תכניות קומה א' וגג	1:100
08	חזיתות	1:100
09	חתכים	1:100
10	סכמות סטטיות	1:100
11	תכנית קומת קרקע	1:50
12	תכנית קומה א'	1:50
13	חזיתות	1:50
14	חתך A-A	1:50
15	חתך B-B	1:50
16	**גיליון מדרגות**	1:25, 1:5
17	פרטי בניין	1:20, 1:5
18	רשימת אלומיניום ונגרות	1:50
19	עיצוב פנים – חלל המגורים	1:50
20	עיצוב ריהוט – אי המטבח	1:25, 1:10, 1:2
21	הדמיות חוץ	
22	הדמיות פנים	
23	תודה	

מגמה:
הנדסאים – אדריכלות ועיצוב פנים

שם המגיש/ה ות.ז.:
__________ __________

תאריך:
10.2026

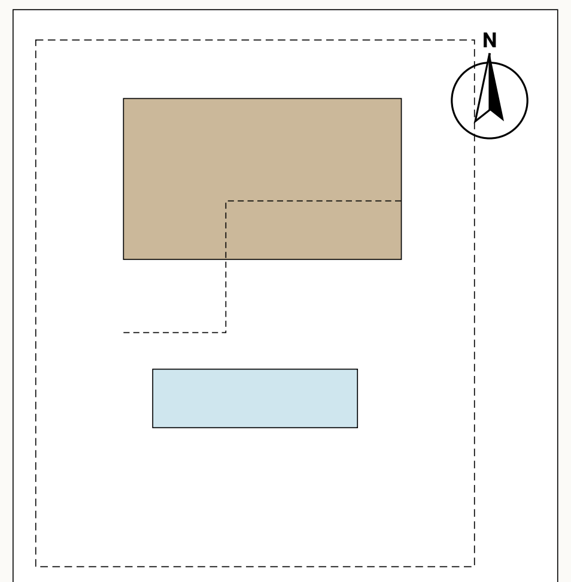

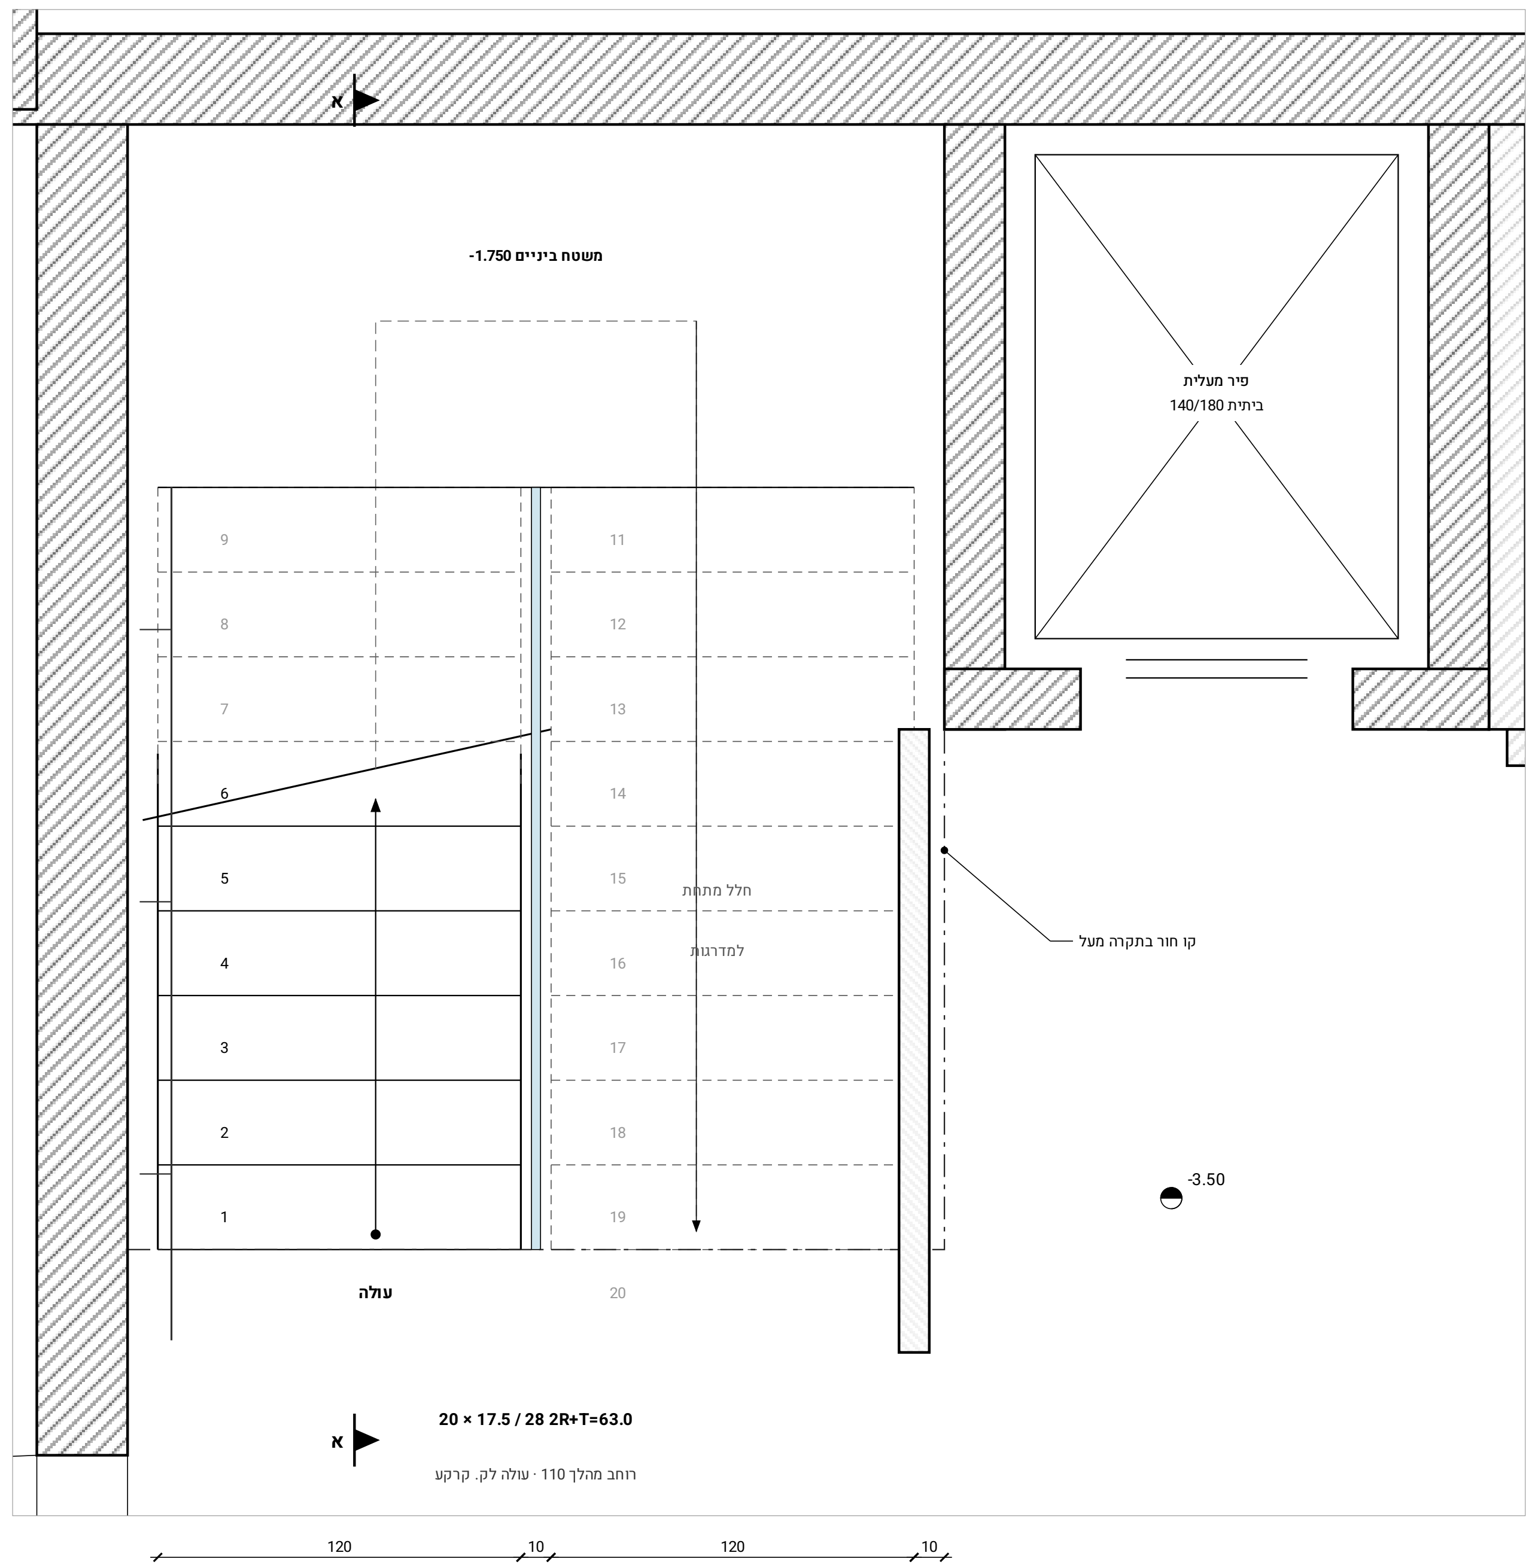

תכנית מדרגות – קומת מרתף

קנ"מ 1:25

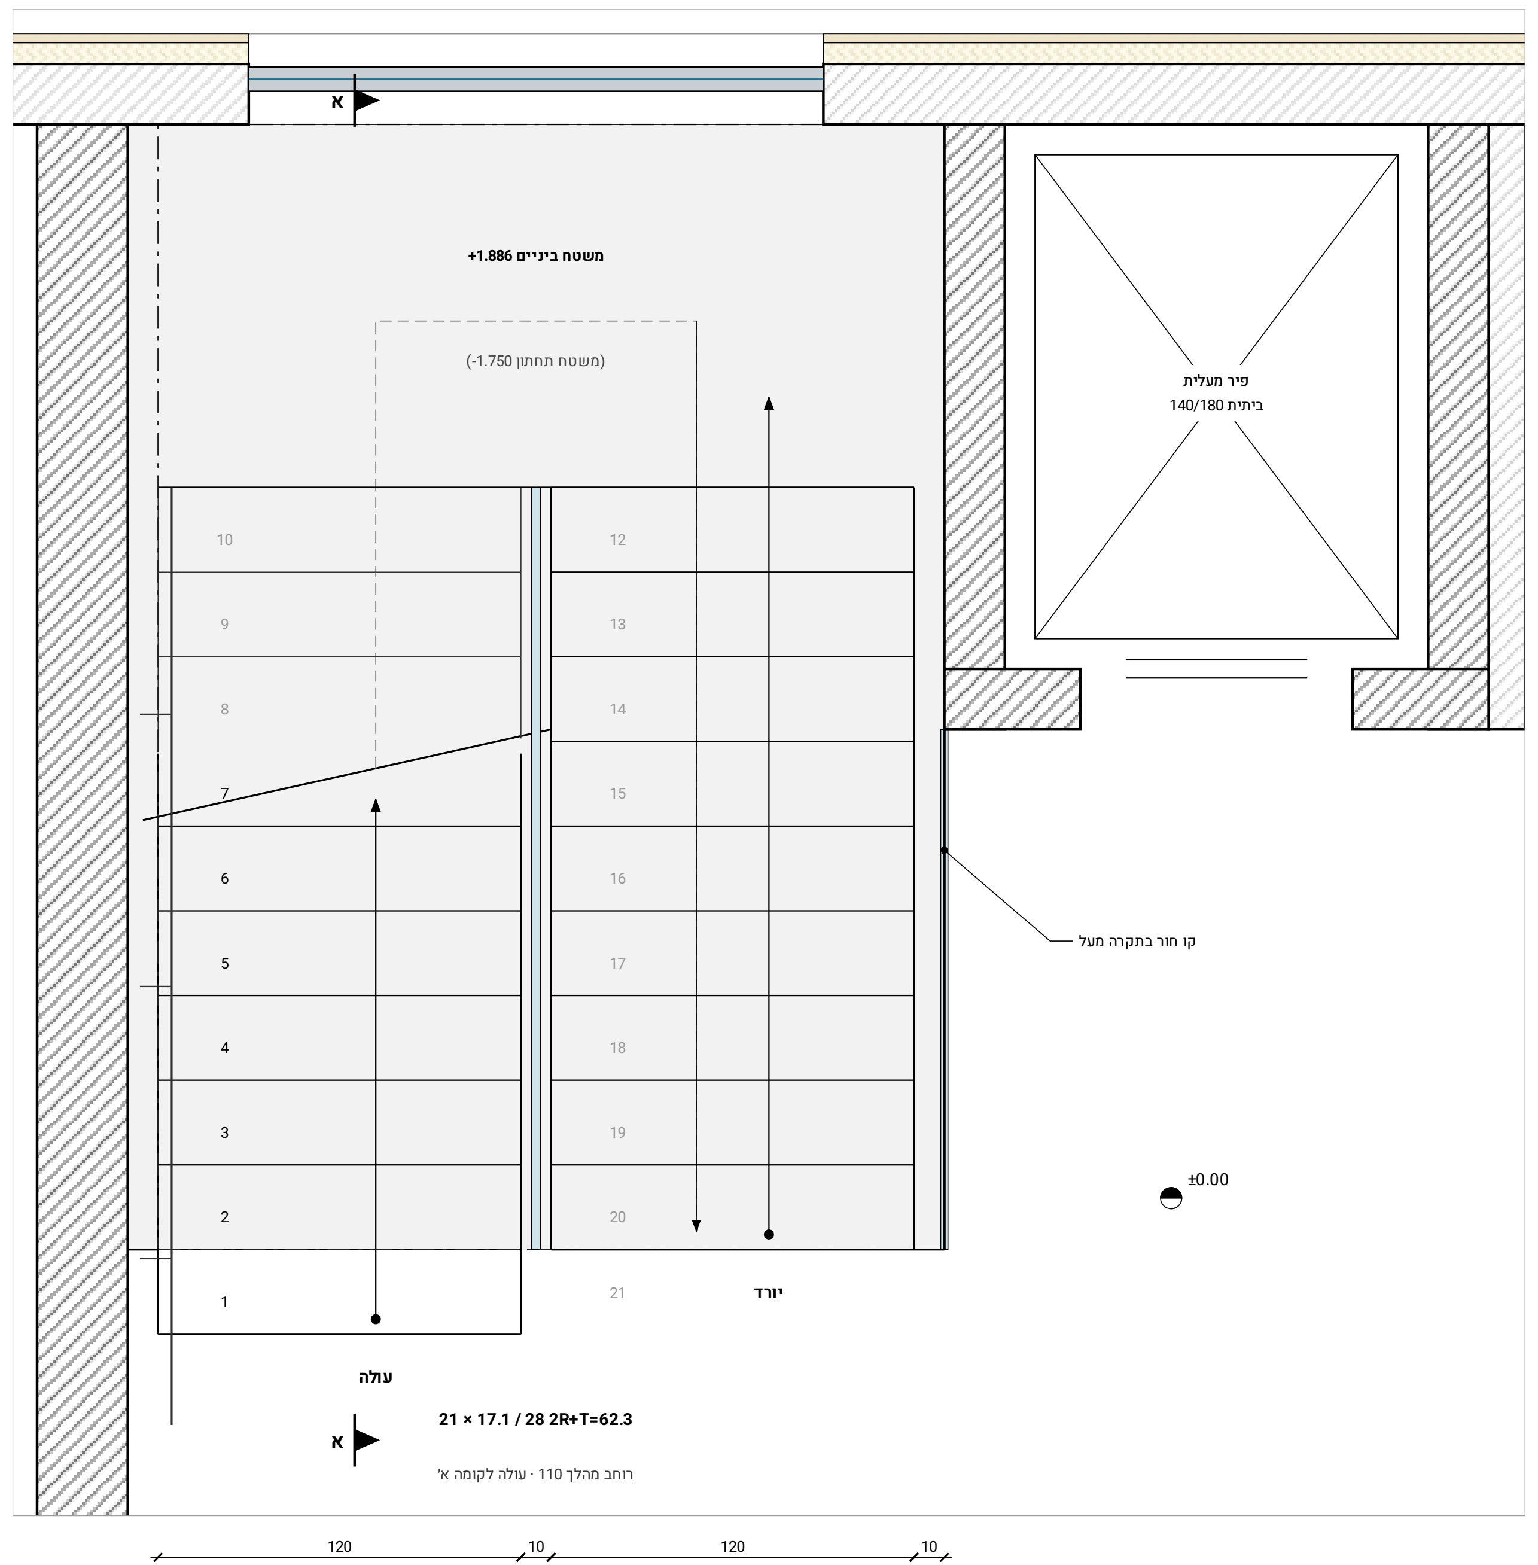

תכנית מדרגות – קומת קרקע

קנ"מ 1:25

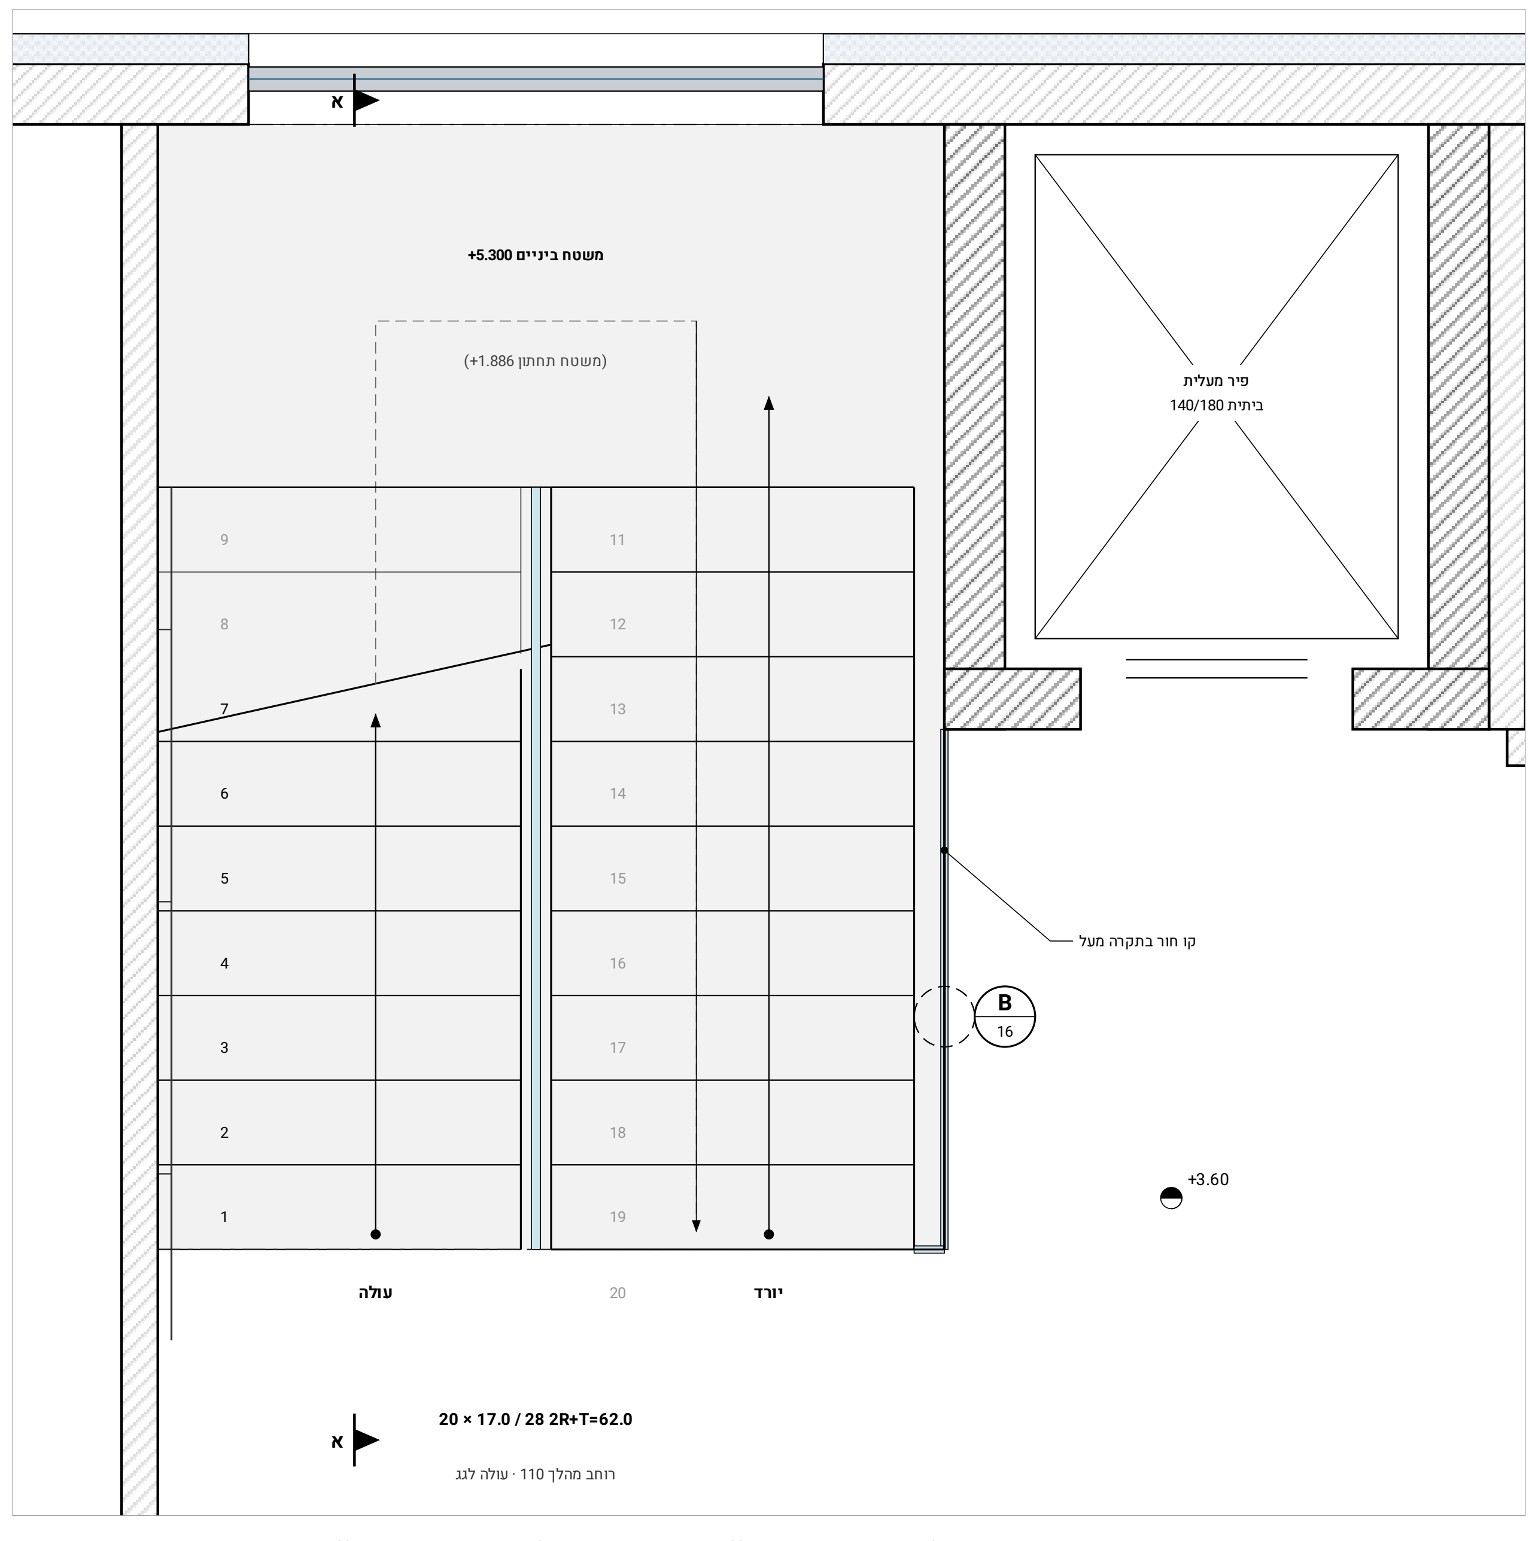

תכנית מדרגות – קומה א'

קנ"מ 1:25

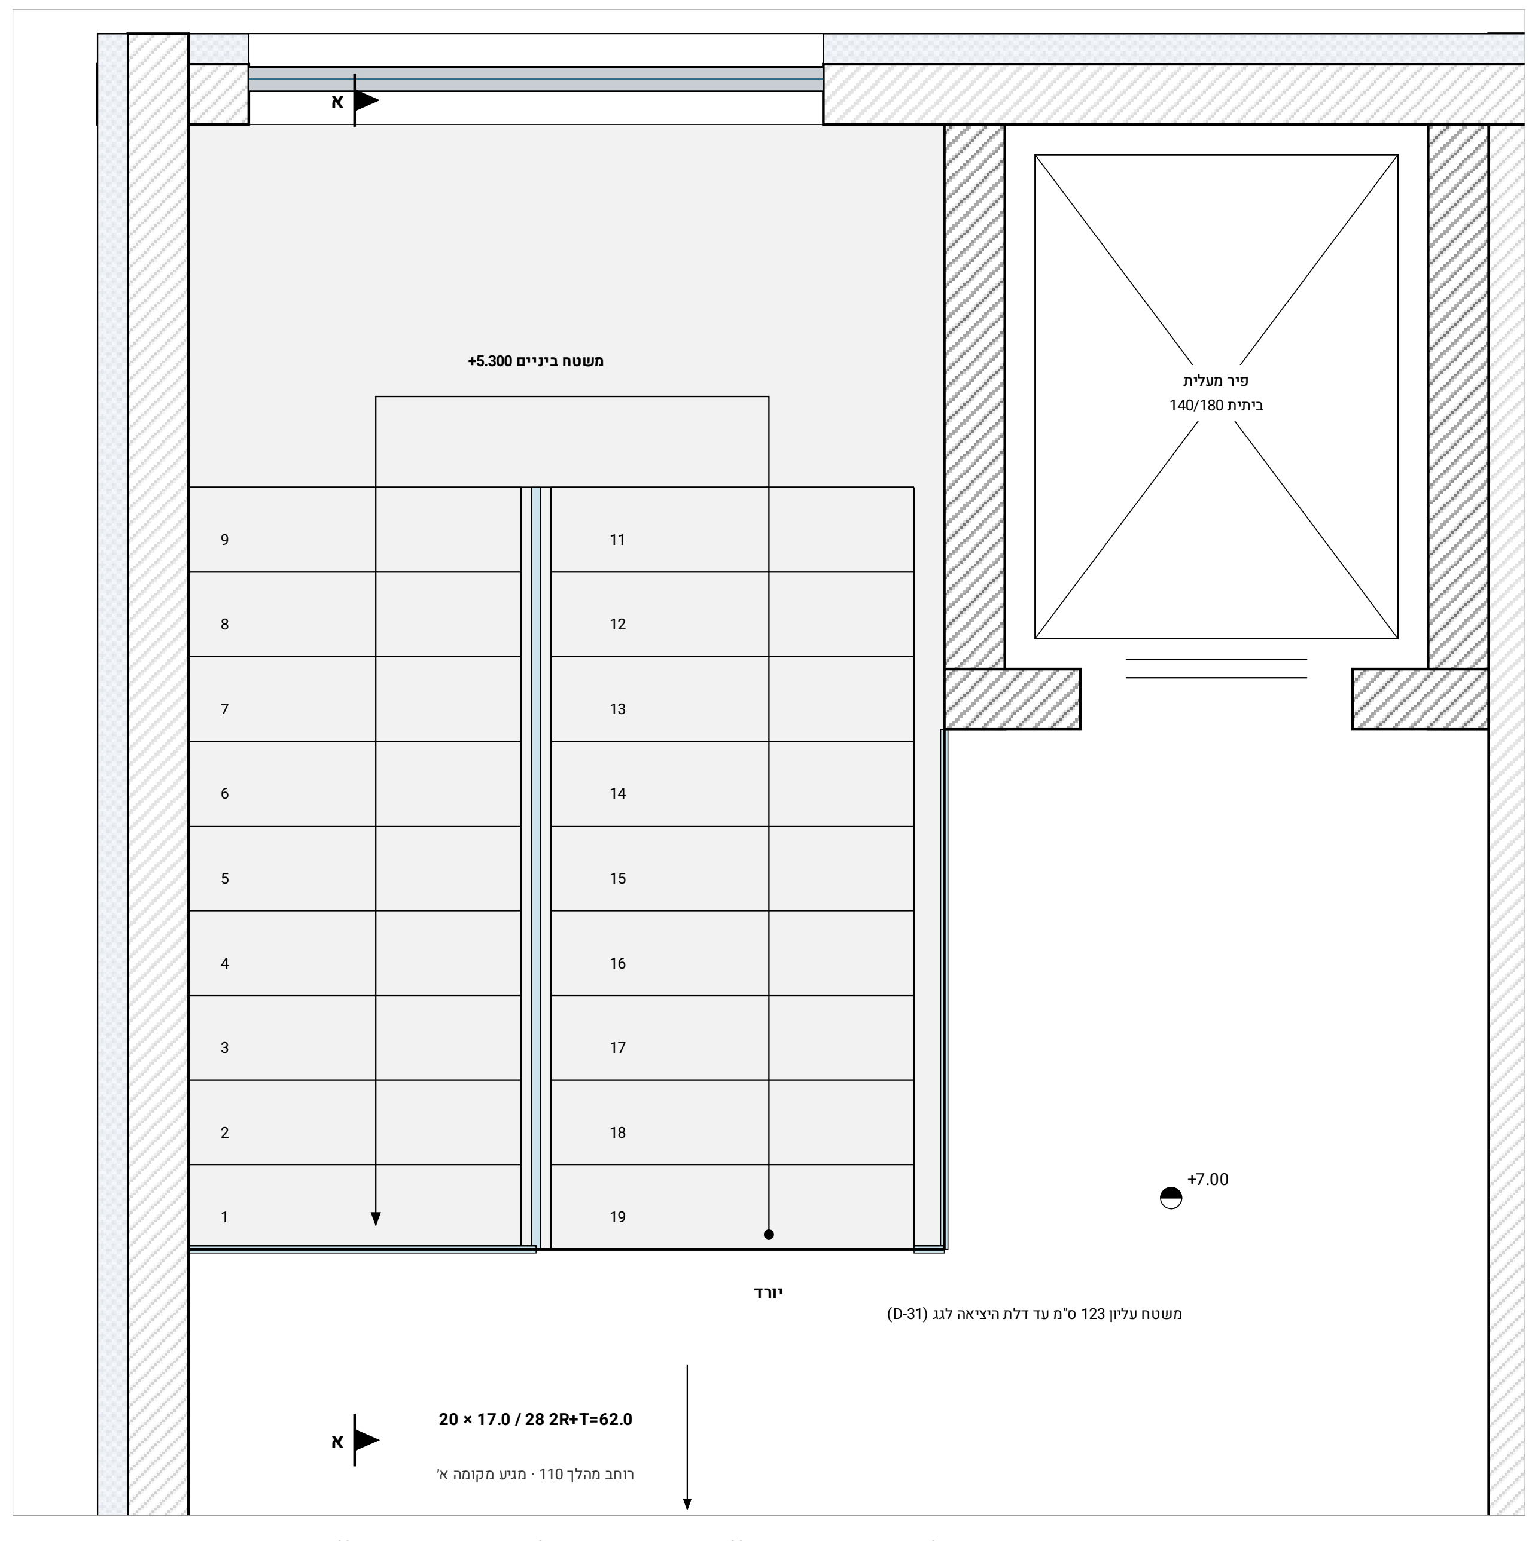

תכנית מדרגות – יציאה לגג

קנ"מ 1:25

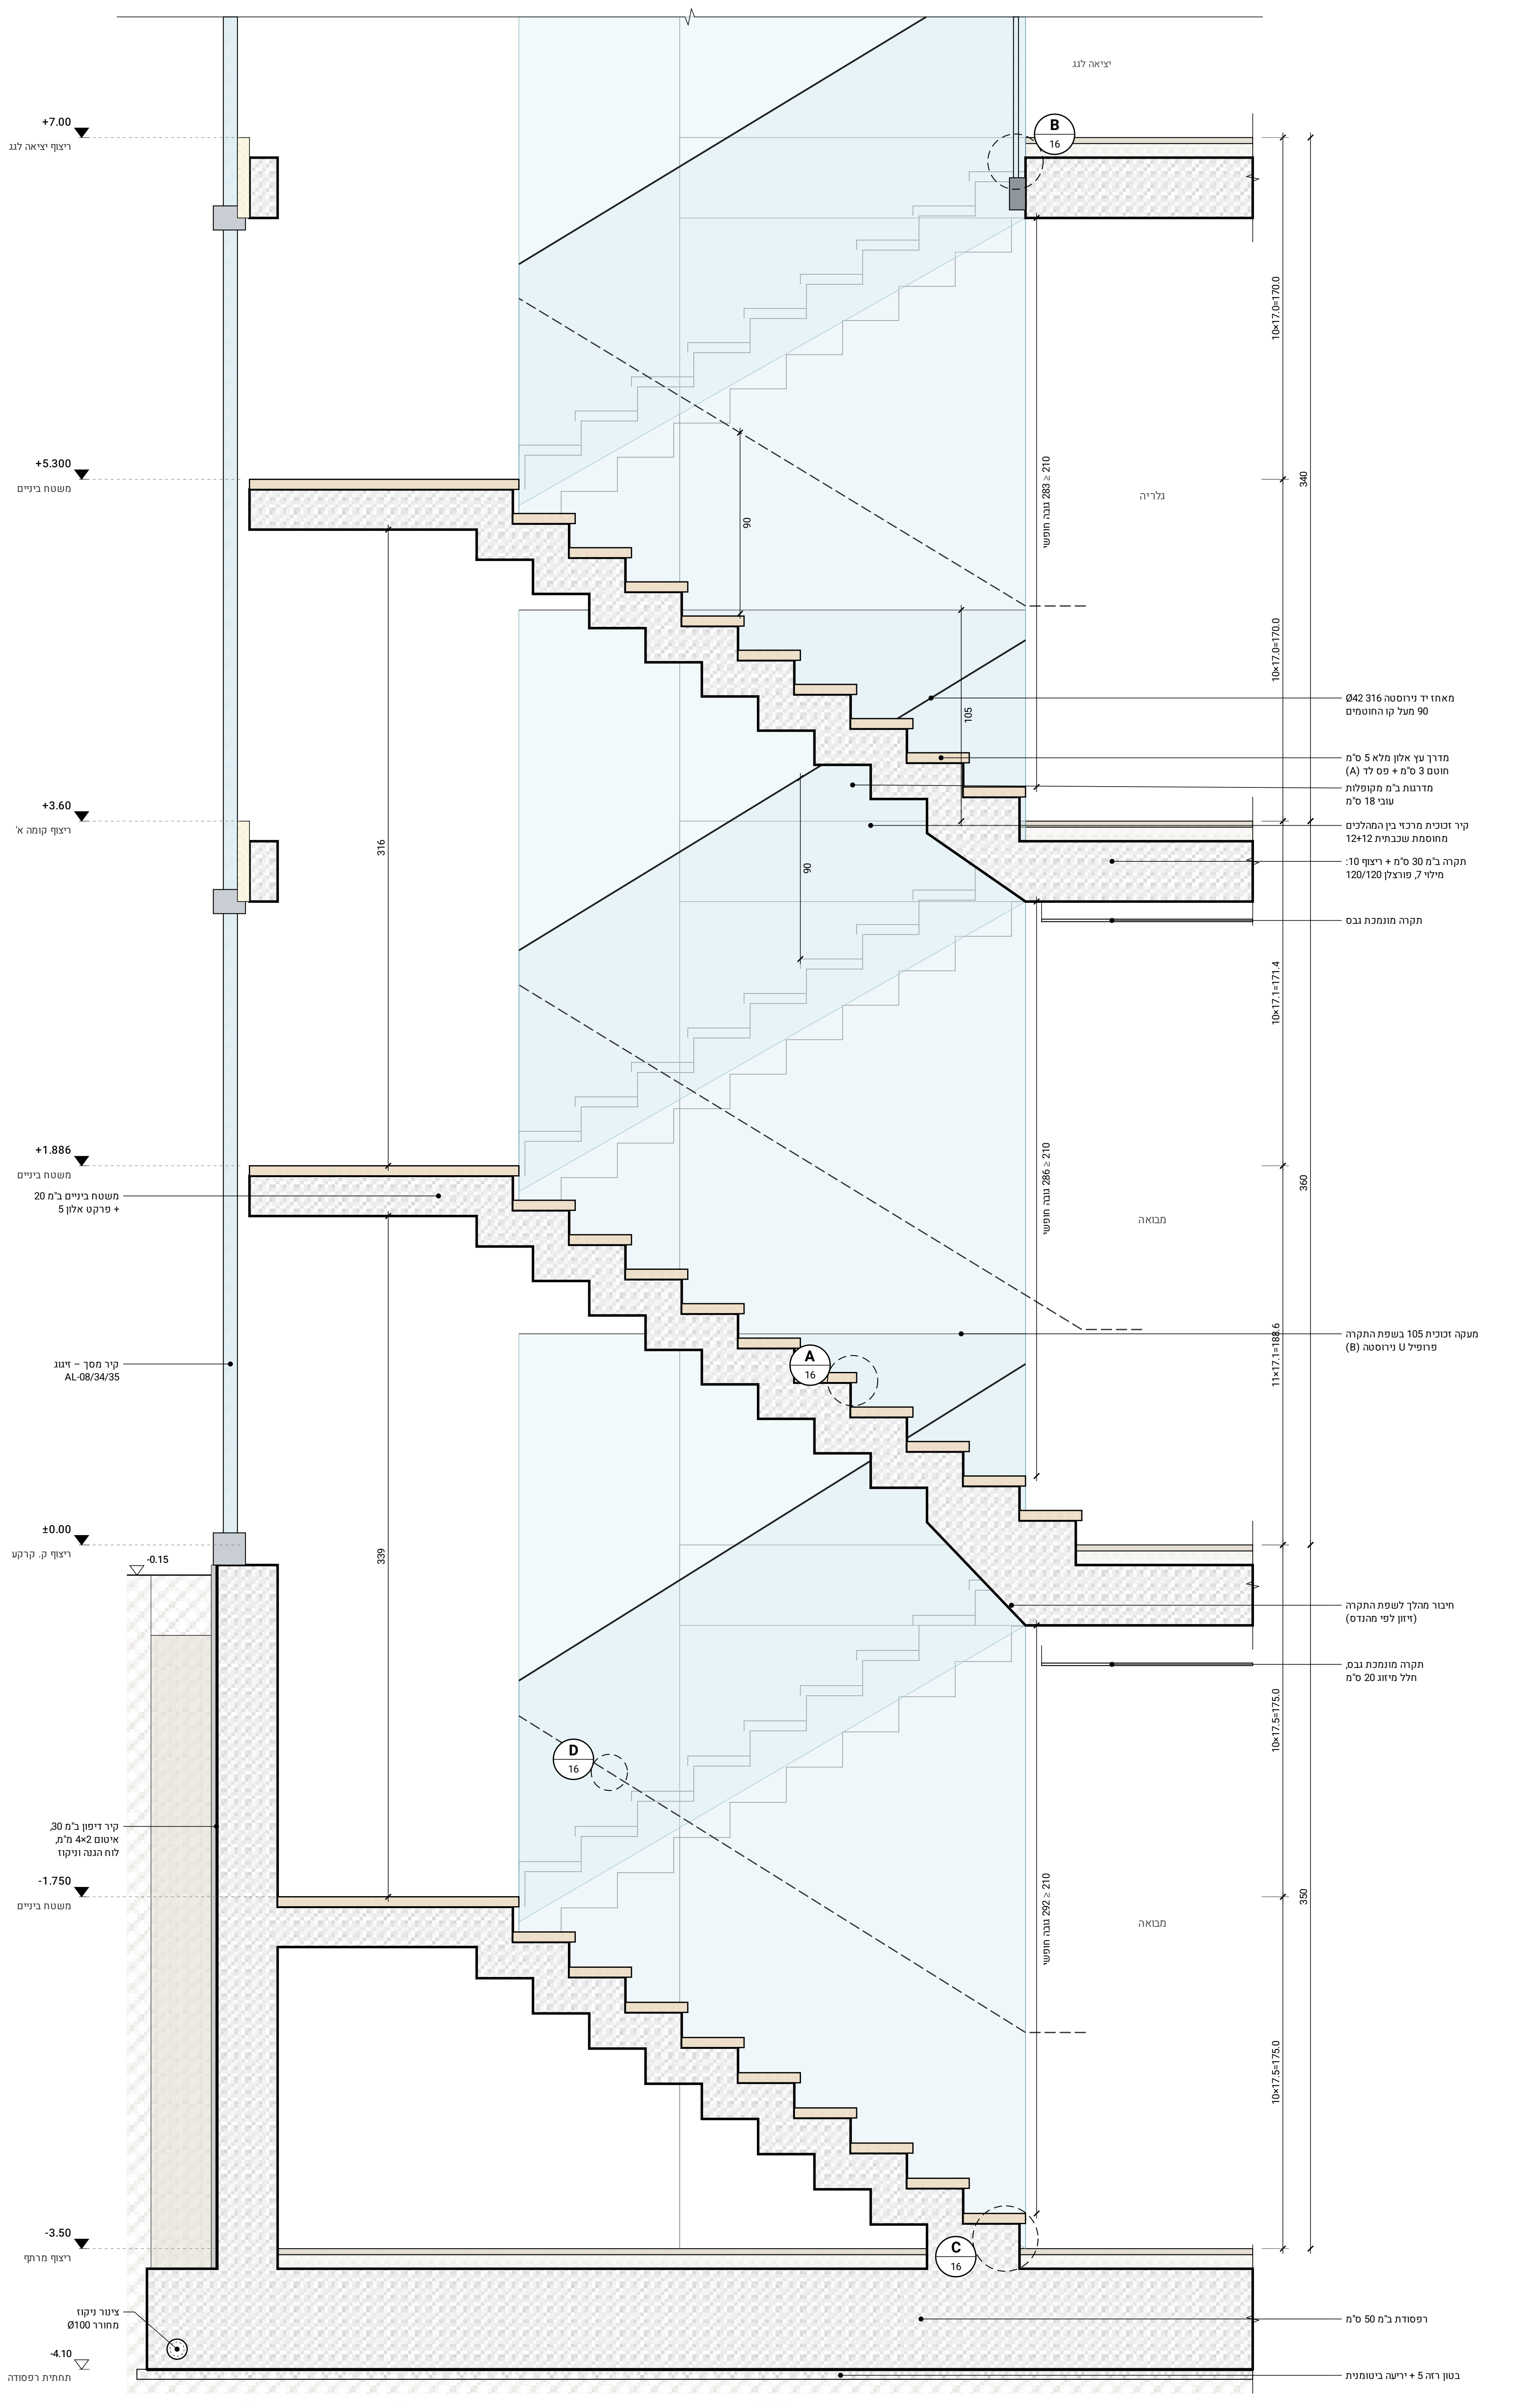

חתך א-א – מדרגות

קנ"מ 1:25

הערות:
1. מידות בס"מ, מפלסים במ' (±0.00 = +18.50).
2. 2R+T בתחום 61–63 ס"מ; רום ≤17.5, שלח 28.
3. מעקה 105 במשטחים, 90 לאורך המהלך;
מרווח פתוח ≤10 ס"מ.
4. גובה חופשי מעל קו החוטמים ≥210.
5. נירוסטה 316 ואלומיניום ימי (אוויר מלוח).
6. מדרגות ב"מ – לפי תכנון מהנדס קונסטרוקציה.
7. גובה חופשי מינ' מחושב: 265 ס"מ.

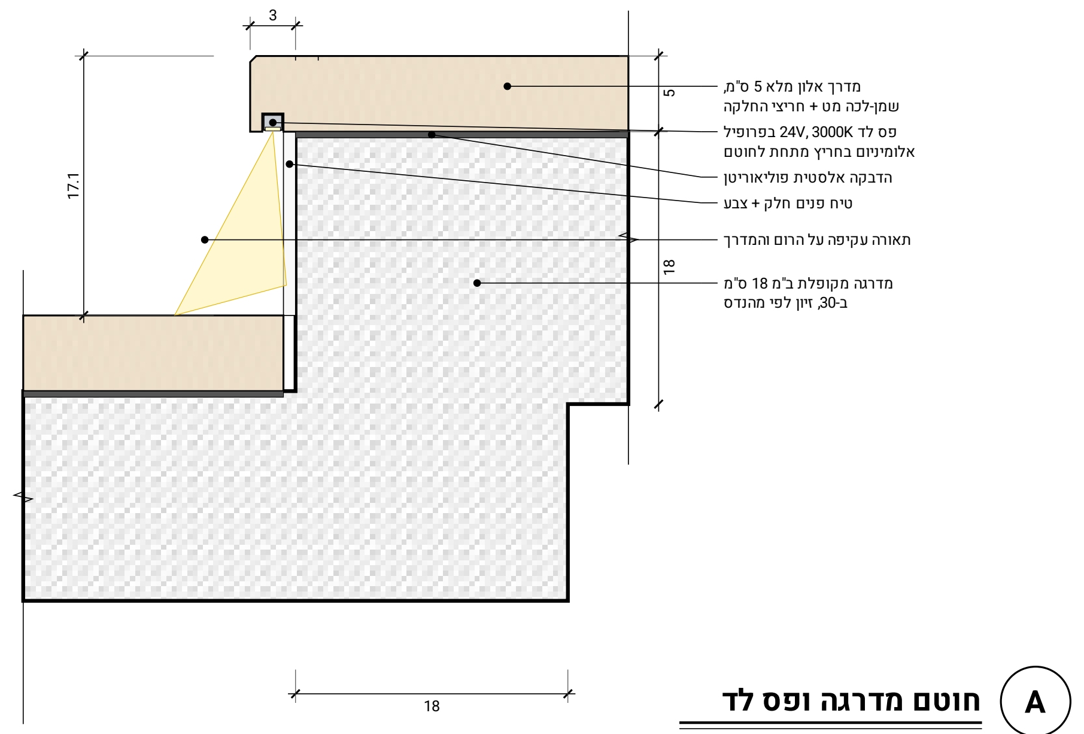

A **חוטם מדרגה ופס לד**

קנ"מ 1:5

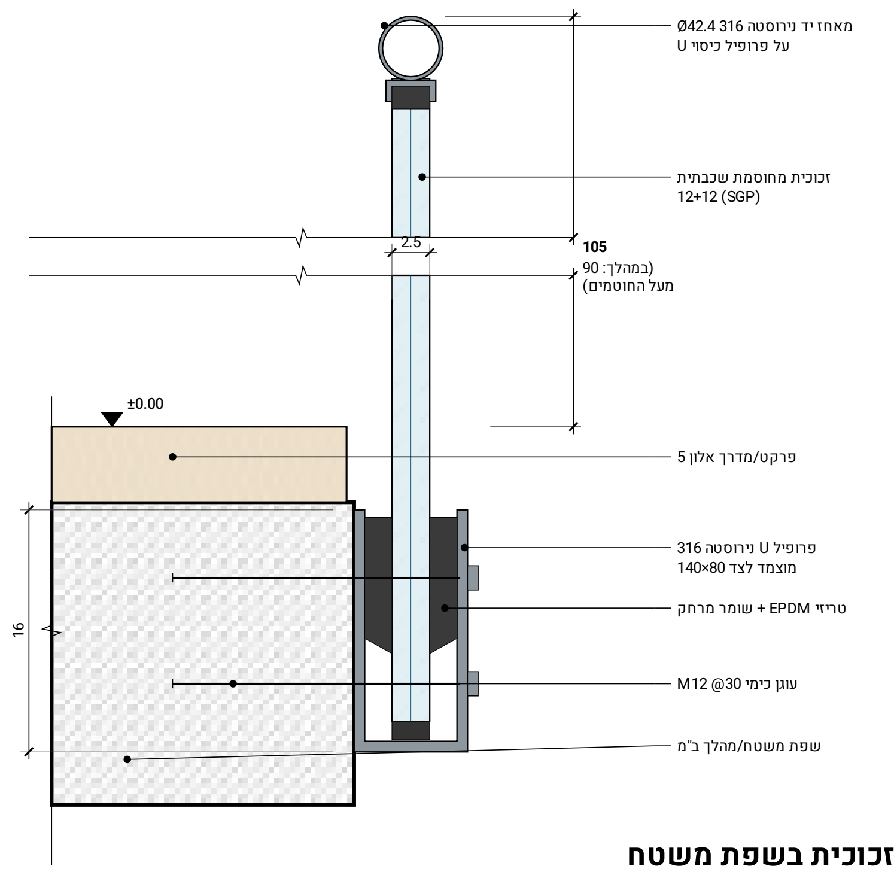

B **מעקה זכוכית בשפת משטח**

קנ"מ 1:5

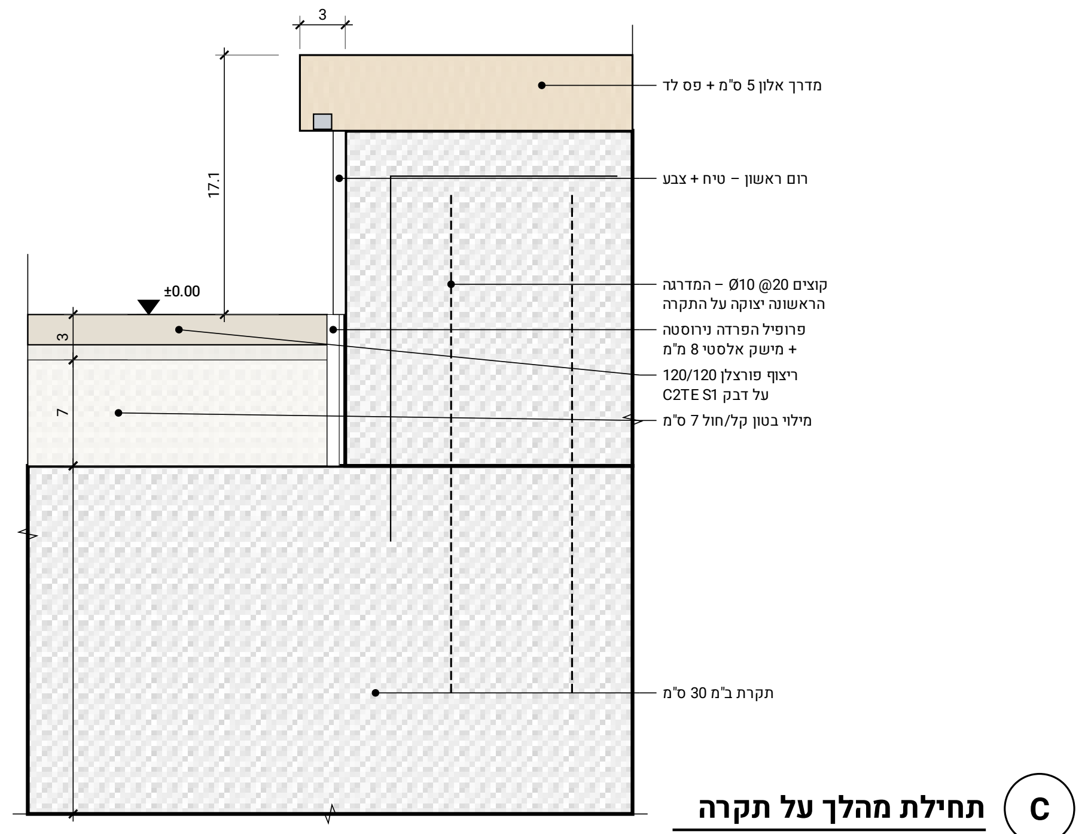

C **תחילת מהלך על תקרה**

קנ"מ 1:5

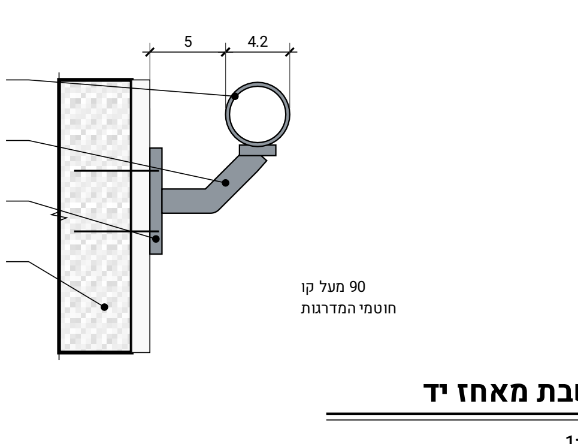

D **תושבת מאחז יד**

קנ"מ 1:5