ניתוח אתר וסביבה

קיסריה · רובע 13 (שכונת הגולף) · אקלים, תכנון ואסטרטגיות

בית כורכר

BEIT KURKAR

שם הפרויקט:
וילת בוטיק בקיסריה

מיקום הפרויקט:
קיסריה, רובע 13 (מגרש לימודי)

מנחה:
שירן שריקי

שם הגיליון:
ניתוח אתר וסביבה

מס' גיליון: **03**
קנ"מ: –

רשימת גיליונות:

01 שער
02 קונספט ומחקר
03 ניתוח אתר וסביבה
04 תכנית העמדה וטבלת שטחים 1:200
05 תכנית פיתוח שטח 1:100
06 תכניות מרתף וקרקע 1:100
07 תכניות קומה א' וגג 1:100
08 חזיתות 1:100
09 חתכים 1:100
10 סכמות סטטיות 1:100
11 תכנית קומת קרקע 1:50
12 תכנית קומה א' 1:50
13 חזיתות 1:50
14 חתך A-A 1:50
15 חתך B-B 1:50
16 גיליון מדרגות 1:25, 1:5
17 פרטי בניין 1:20, 1:5
18 רשימת אלומיניום ונגרות 1:50
19 עיצוב פנים – חלל המגורים 1:50
20 עיצוב ריהוט – אי המטבח 1:25, 1:10, 1:2
21 הדמיות חוץ
22 הדמיות פנים
23 תודה

מגמה:
הנדסאים – אדריכלות ועיצוב פנים

שם המגיש/ה ות.ז.:
__________ __________

תאריך:
10.2026

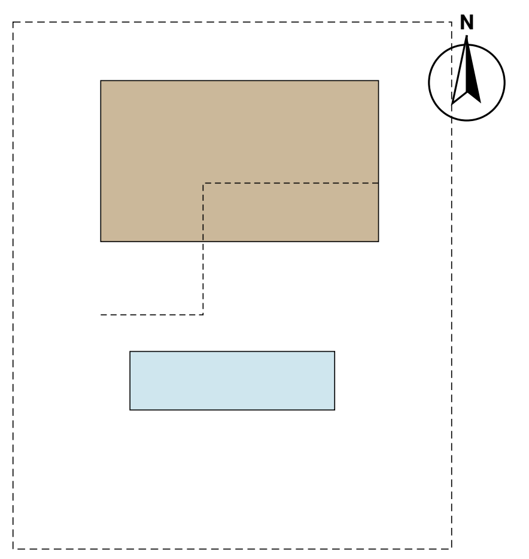

01 קיסריה – סכמת העיר וסביבתה

סכמה – לא בקנה מידה

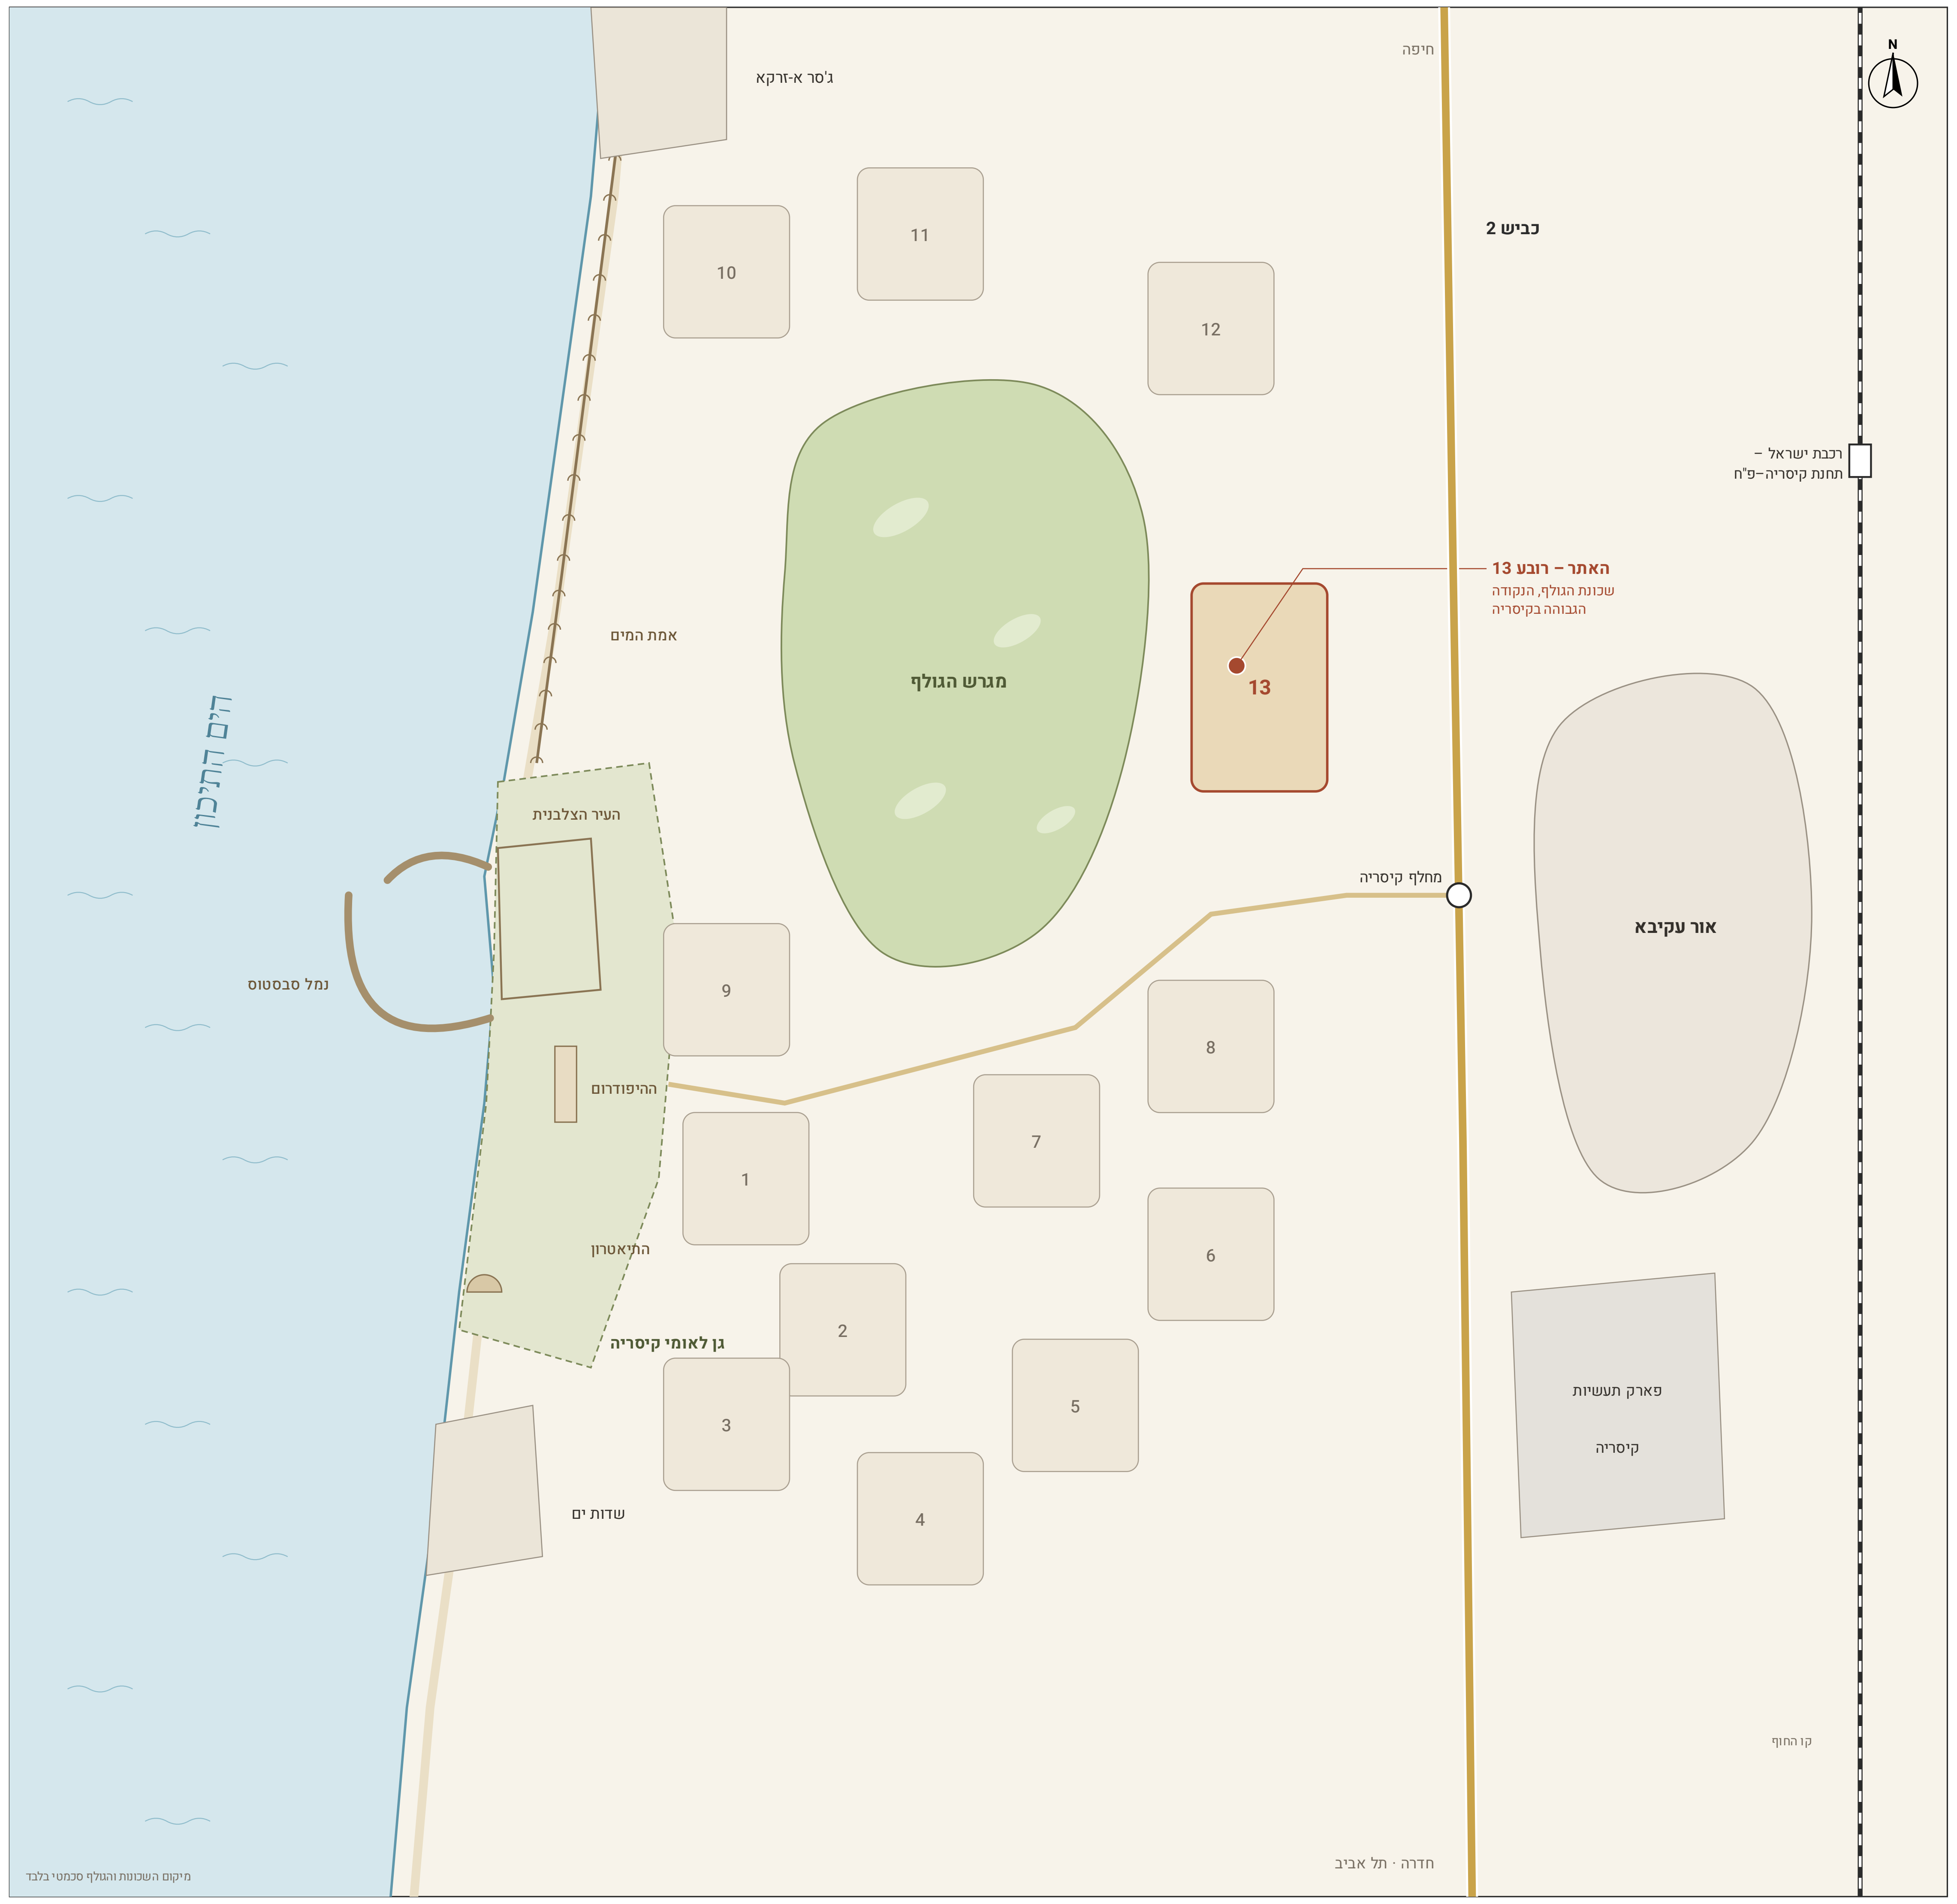

02 ניתוח המגרש – רובע 13

מקרא

- 〰 בריזת ים קיצית מערב–צפון-מערב
- 〰 סערות חורף מדרום-מערב
- 〰 שרב – רוח מזרחית חמה ויבשה
- – – מסלול שמש – קיץ (21.6)
- - - - מסלול שמש – חורף (21.12)
- ◁ מבט פתוח לגולף ולשקיעה
- ⋀⋀⋀ רעש תנועה מן הרחוב
- ●●●● מיסוך צמחייה – פרטיות
- ▨ קווי בניין – תחום בנייה
- —·— גבול מגרש 30×36 מ'

שטח המגרש	1,080 מ"ר
חזית לרחוב	30 מ' (מזרח)
עומק	36 מ'
גבול מערבי	מגרש הגולף
מפלס ±0.00	+18.50 מעל פני הים

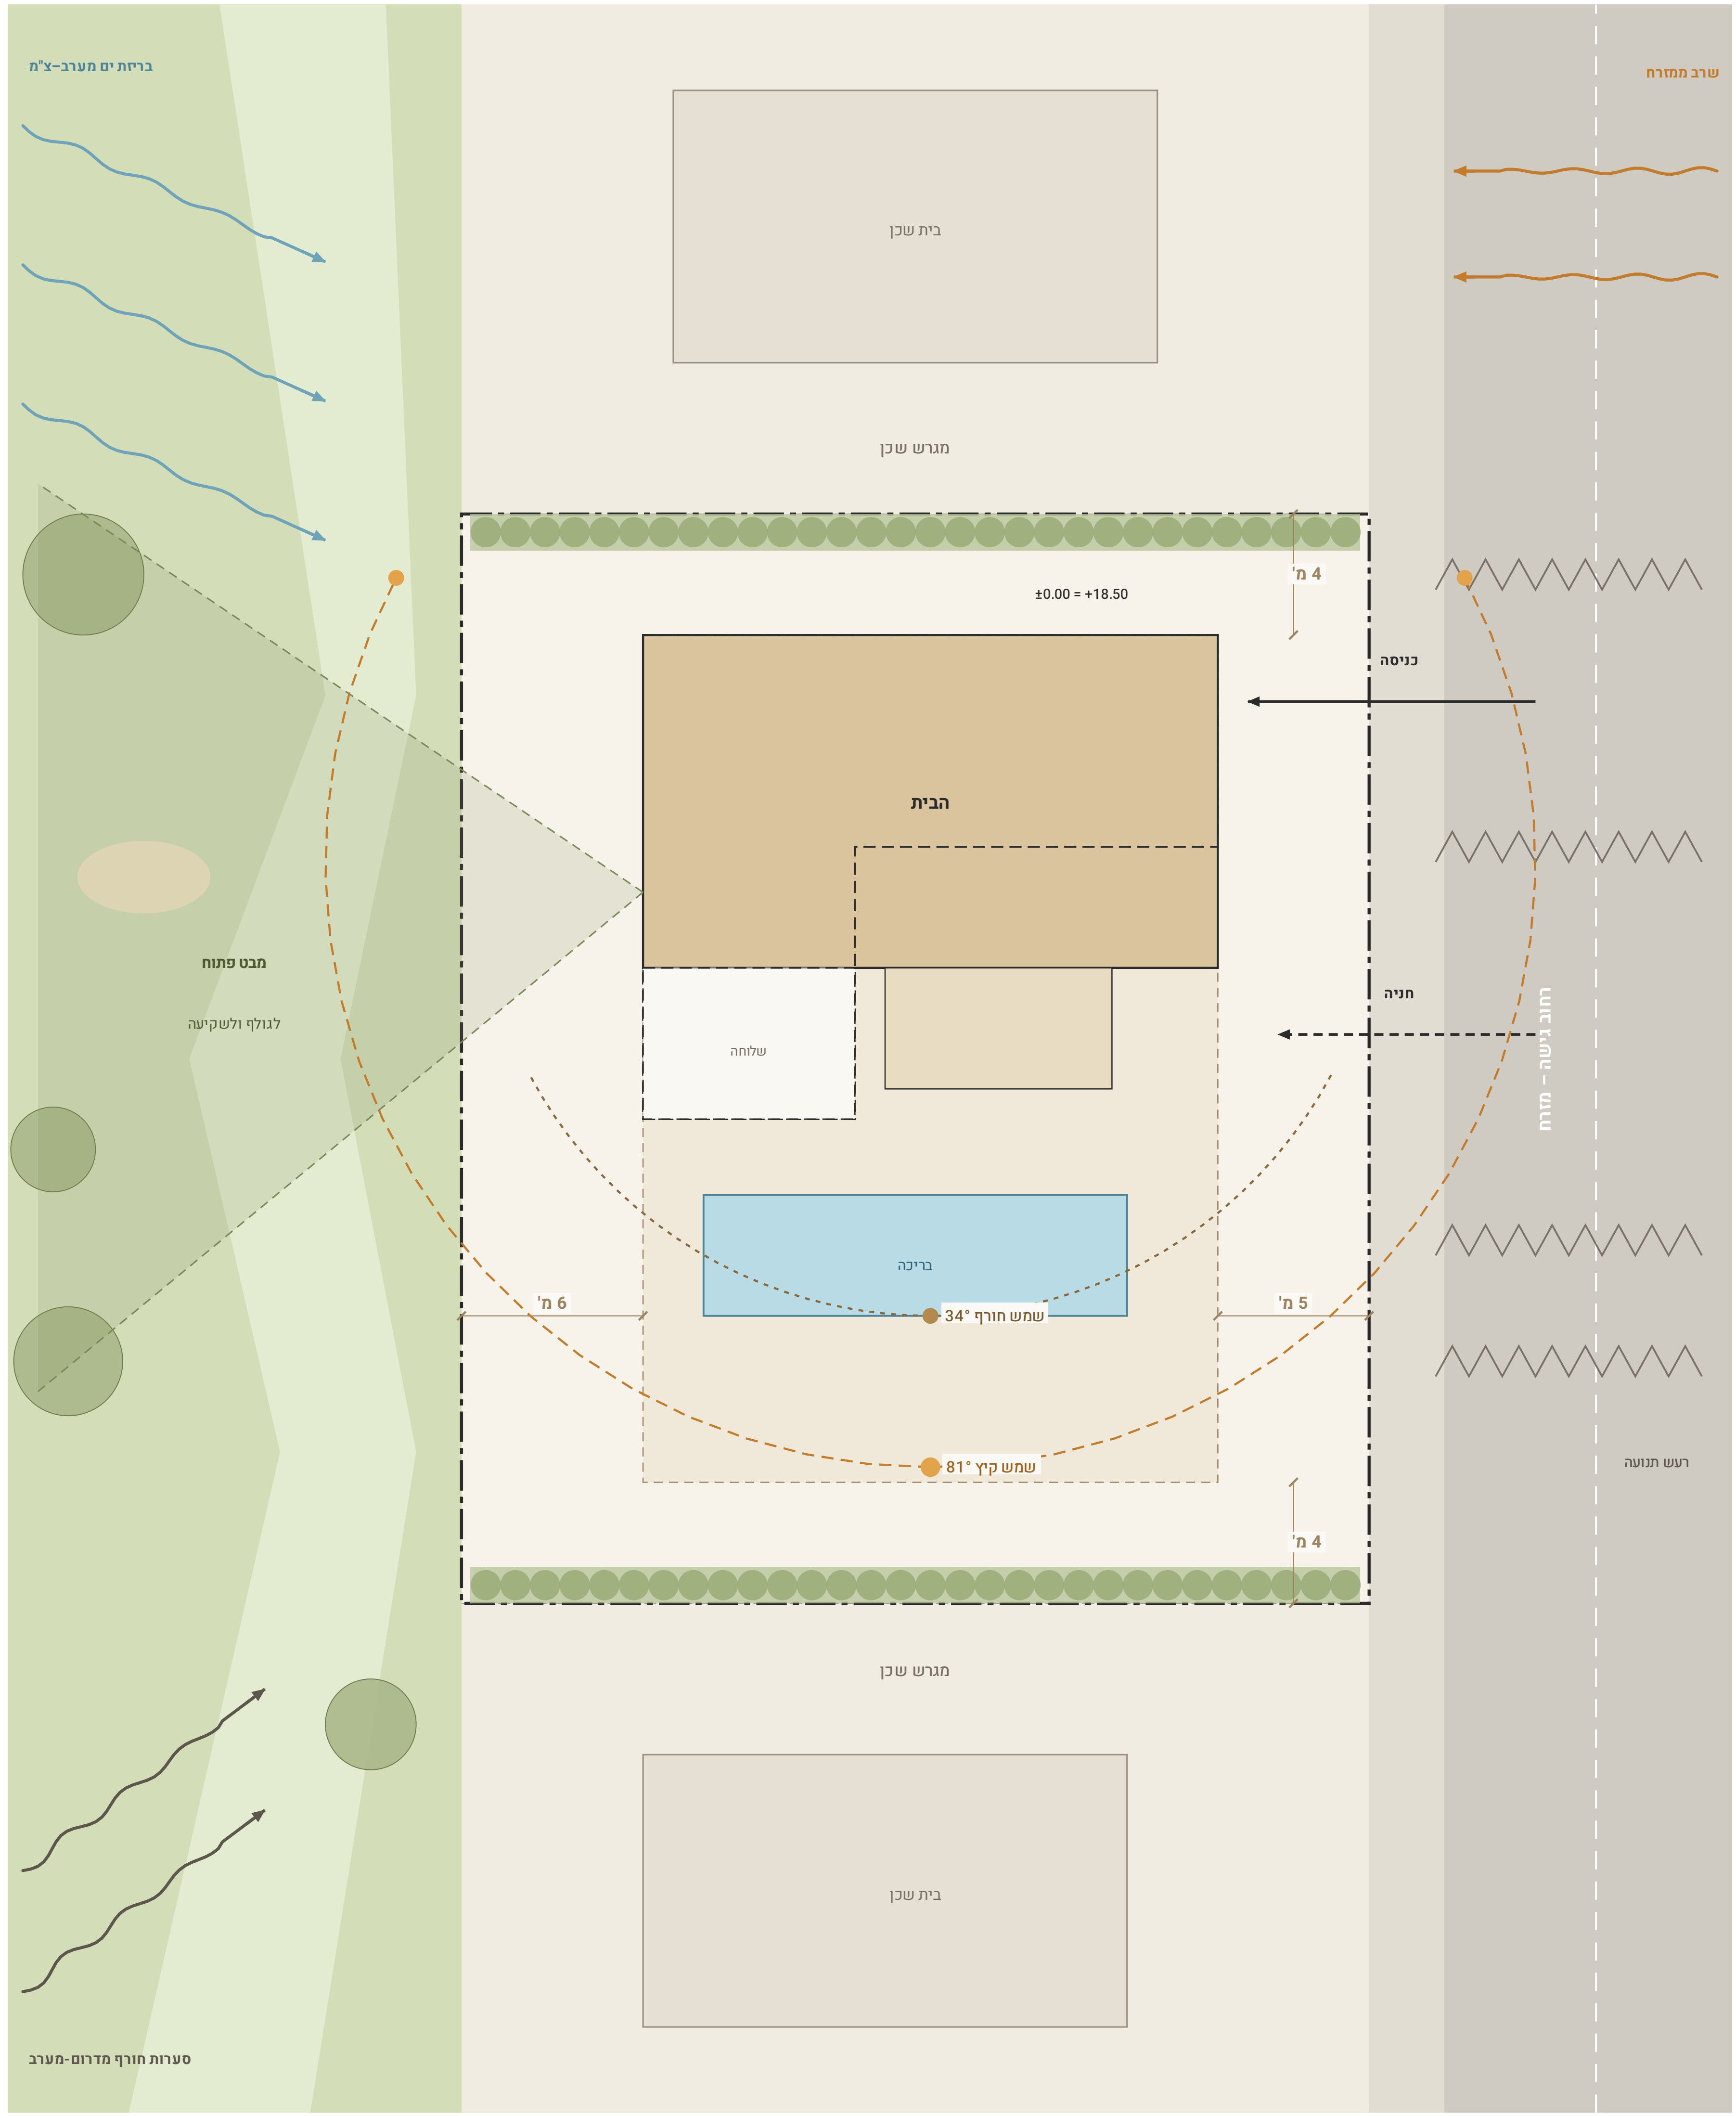

03 אסטרטגיות תכנון – מן הניתוח אל הבית

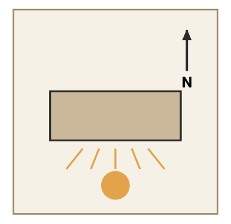

01 אוריינטציה

ציר ארוך מזרח–מערב; חללי המגורים והוויטרינות פונים דרומה אל הגן, חזית הרחוב במזרח סגורה ושקטה.

יישום: סלון, אוכל ומטבח בחזית הדרומית; לובי, שירות וחניה במזרח.

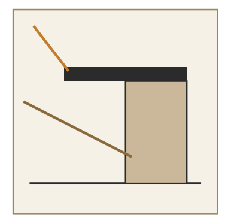

02 הצללה דרומית

שלוחה של 5 מ' ולוג'יה שקועה 1.6 מ' – חוסמות את שמש הקיץ (81°) ומכניסות את שמש החורף (34°).

יישום: מרפסת מקורה של 35 מ"ר מתחת לשלוחה; לוג'יית ההורים.

03 רפפות מערביות

רפפות אנכיות 50/200 מ"מ במרווח 180 בחזית המערבית חוסמות את שמש אחר-הצהריים הנמוכה ושומרות על המבט לגולף.

יישום: חזית מערב של סוויטת ההורים וחזית מזרח של חדר שינה 2.

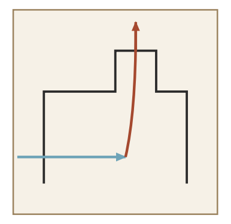

04 אוורור צולב וארובה

פתחים מנוגדים בכיוון בריזת הים, ופליטת אוויר חם דרך חדר המדרגות והיציאה לגג; פטיו שקוע מאוורר את המרתף.

יישום: ויטרינות הזזה בדרום ובמערב, זיגוג רציף בחדר המדרגות.

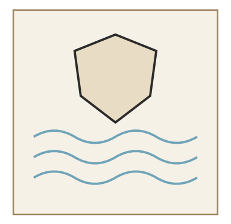

05 חומרים לאוויר מלוח

אלומיניום בגימור ימי, נירוסטה 316, אבן טבעית ספוגה, טיח סיליקט; פרטי איטום וניקוז מוגברים.

יישום: פרזול נירוסטה 316, אלומיניום בצביעה בתנור בדרגה ימית.

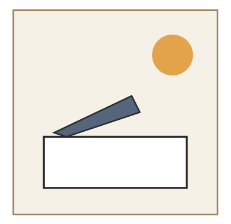

06 אנרגיה ומים

מערכת PV על הגג (חובה), דוד שמש, השקיה בטפטוף וצמחייה ים-תיכונית חסכונית במים.

יישום: פאנלים על גג האגף המערבי; מרפסת גג עם פרגולה.

04 נתוני אקלים

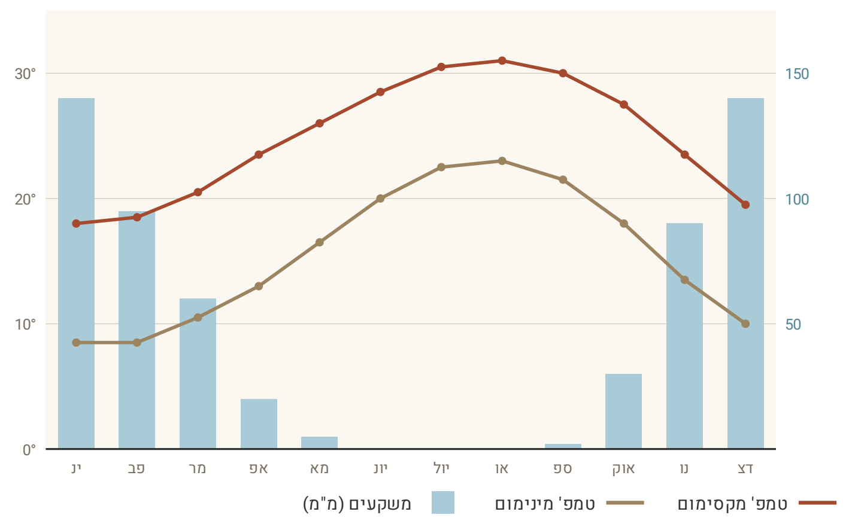

טמפ' ממוצעת יולי–אוגוסט	31° / 23°
טמפ' ממוצעת ינואר	18° / 8.5°
לחות יחסית	65%–75% (גבוהה בקיץ)
משקעים שנתיים	כ-580 מ"מ, נוב'–מרץ
רוח שלטת	מערב–צ"מ, 3–5 מ'/ש'
קרינת שמש	כ-2,000 קוט"ש/מ"ר·שנה
אוויר	מלוח – כ-2 ק"מ מן הים

ערכים משוערים – מישור החוף הצפוני (חדרה/קיסריה), לפי ממוצעי השירות המטאורולוגי.

05 נתוני תכנון – הנחת בסיס

נושא	רובע 13	מוצע
שטח מגרש	1,080 מ"ר	1,080 מ"ר
שטח עיקרי	35% = 378 מ"ר	גיליון 04
שטחי שירות	16% = 173 מ"ר	גיליון 04
תכסית	40% = 432 מ"ר	244 מ"ר = 22.6%
קומות	2 + מרתף	2 + מרתף + גג
מרתף	בקונטור קומה מעל	בקונטור
קו בניין קדמי (מזרח)	5 מ'	5 מ'
קווי בניין צדדיים	4 מ'	4 מ'
קו בניין אחורי (מערב)	6 מ'	6 מ'
חניה	2 בתחום המגרש	2 מקורות
בריכה – שטח מים	עד 60 מ"ר	56 מ"ר
בריכה – עומק	עד 1.8 מ'	1.45 מ'
מערכת PV על הגג	חובה	מתוכנן

יש לאמת מול תב"ע 303-0207092

ונספח הבינוי של רובע 13 לפני הגשה לוועדה המקומית חוף הכרמל.

תקנות: מדרגות 2R+T = 61–63 ס"מ, רום עד 17.5; מעקה 105 ס"מ; ממ"ד נטו 9 מ"ר לפחות; גובה חדר מגורים 2.50 מ' לפחות.

06 מסלול השמש – 32.5° צפון

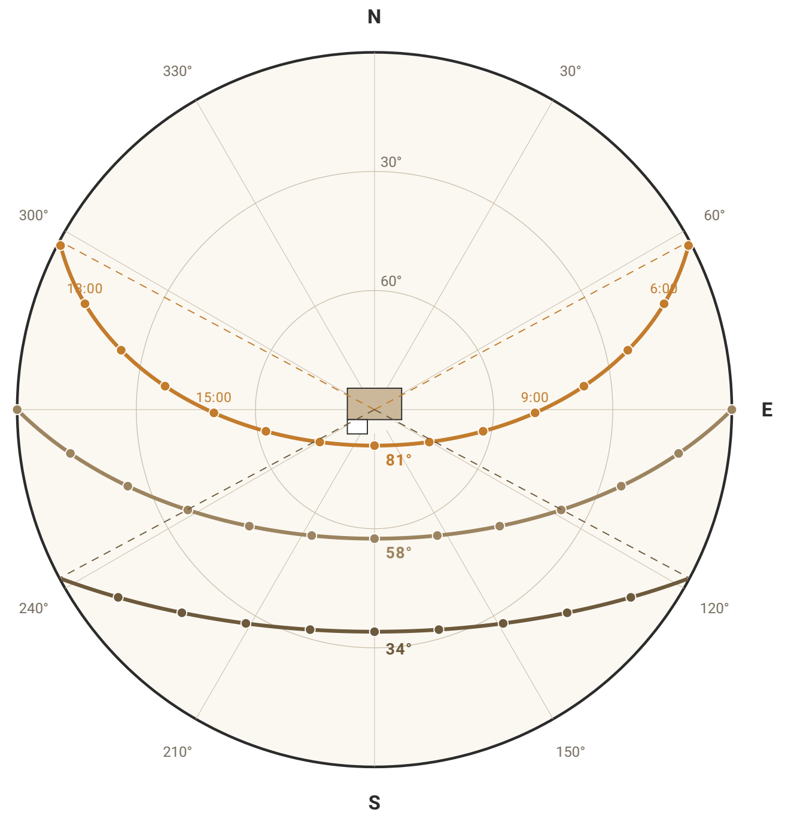

- 21.6 – שיא 80.9° · זריחה 62° / שקיעה 298°
- 21.3 / 23.9 – שיא 57.5° · זריחה 90° / שקיעה 270°
- 21.12 – שיא 34.1° · זריחה 118° / שקיעה 242°

היטל קוטבי – אזימוט מצפון, רדיוס = 90° פחות גובה השמש.

07 שושנת רוחות

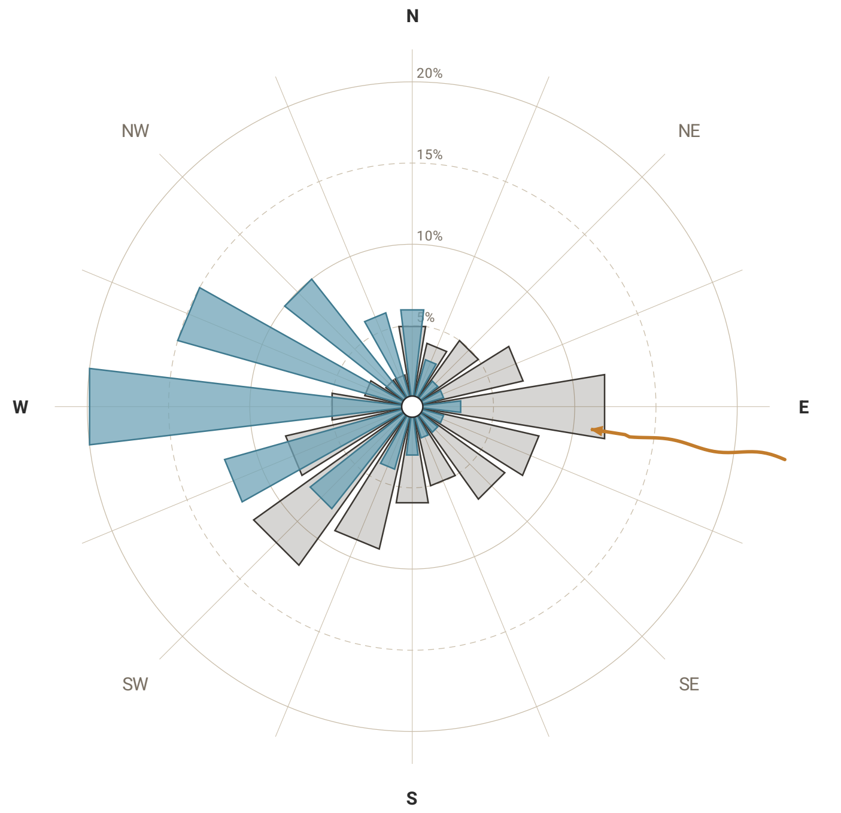

- 🟦 קיץ – בריזת ים מערב–צפון-מערב (צהריים)
- ⬜ חורף – סערות מדרום-מערב, רוח יבשה מזרחית
- 🟧 שרב – מזרח/דרום-מזרח, אביב וסתיו

תדירות משוערת לפי עונה – סכמה להמחשה.