

בית כורכר

BEIT KURKAR

שם הפרויקט:
יולת בוטיק בקיסריה

מיקום הפרויקט:
קיסריה, רובע 13 (מגרש לימודי)

מנהל:
שרית שריקי

שם הבניין:
תכנית מרתף וקרקע

מס' בניין:
06

ק"מ:
1:100




רשימת ניליונות:

- 01 שער
02 קונסטרוקציה ומחיצה
03 ניתוח אדריכלי וסביבה
04 תכנית העבודה וסלול שטחים
05 תכנית פיתוח שטח
06 **תכנית מרתף וקרקע**
07 תכנית קומה א' וגג
08 חיתוך
09 חתכים
10 סכמות סטטיות
11 תכנית קומת קרקע
12 תכנית קומה א'
13 חיתוך
14 חתך A-A
15 חתך B-B
16 ניליון מדרגות
17 פורטל
18 רשימת אלומיניום וגזרות
19 עיצוב פרטים - חלל המגורים
20 עיצוב פרטים - אי המטבח
21 דרימות חוץ
22 דרימות פנים
23 תודה

מנהל:
תכנון - אדריכלות ועיצוב פנים

שם המעשה/ת.ד.:

תאריך:
10.2026

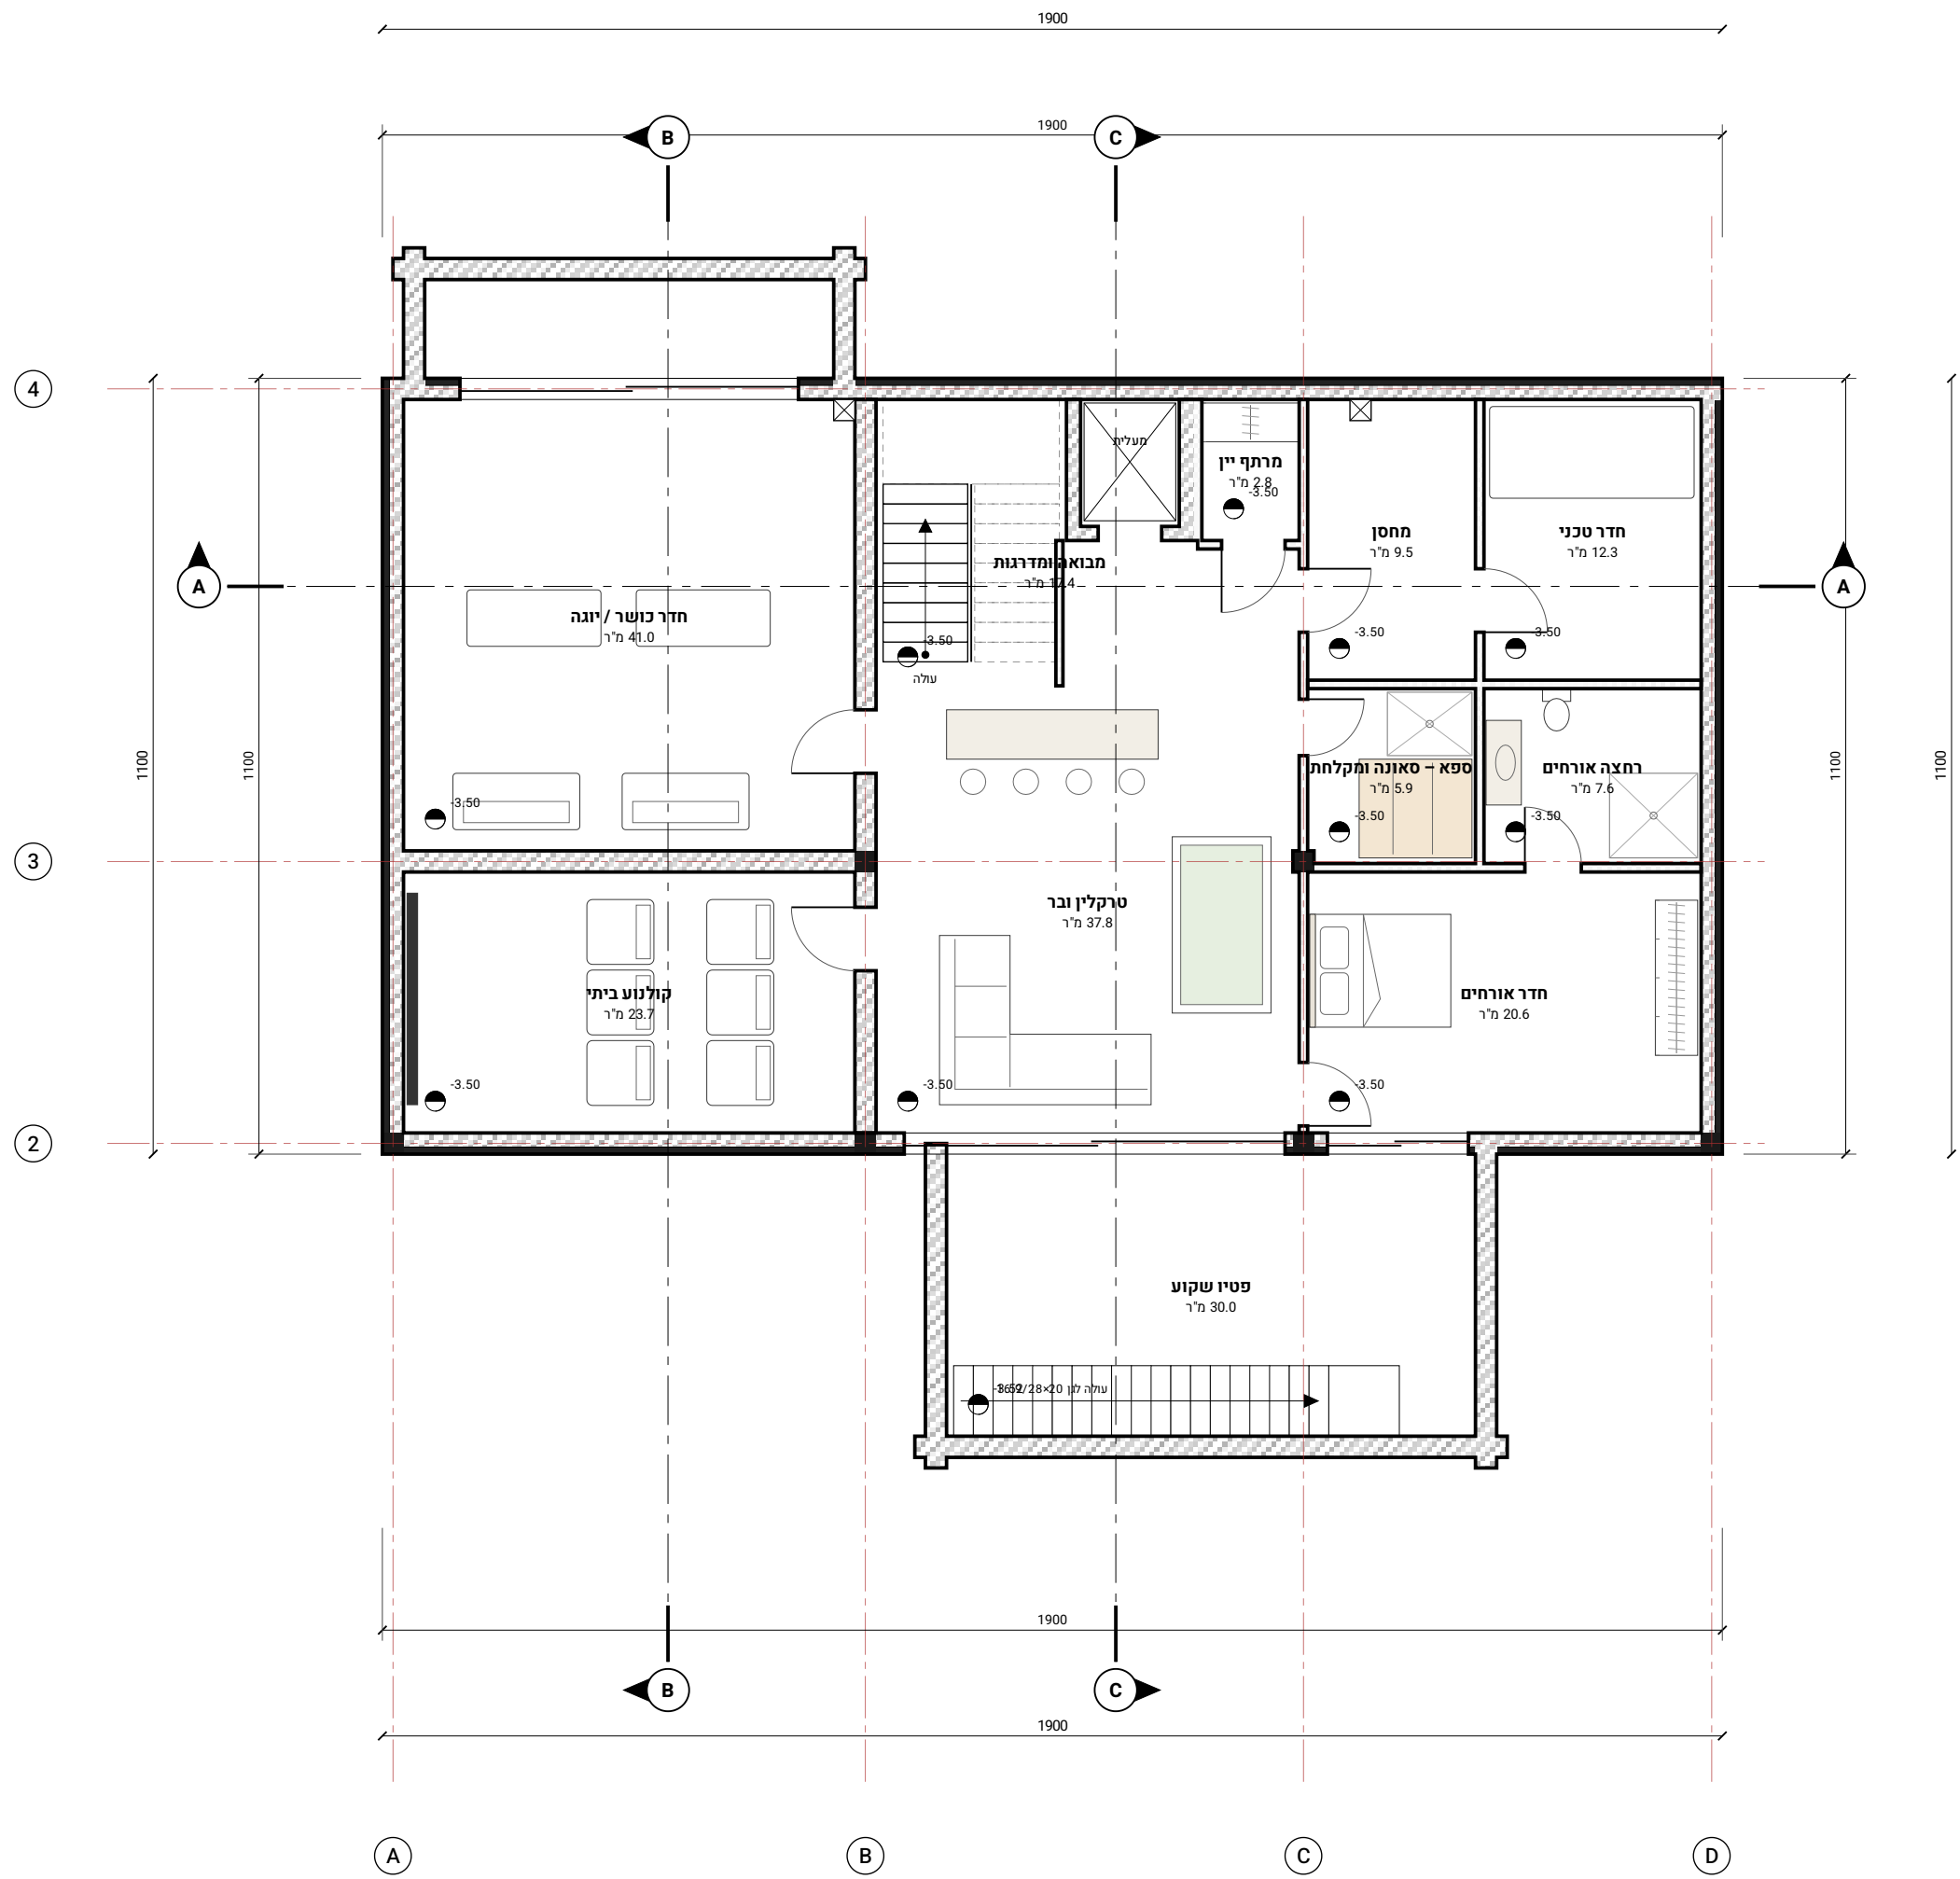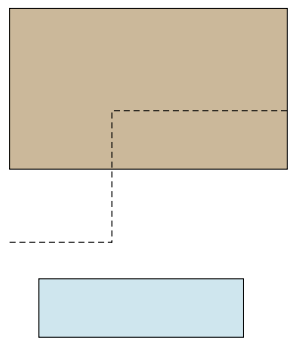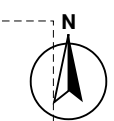


טבלת חללים - קומת מרתף

מס'	חלל	שטח מ"ר	ריצוף	ג. תקרה
B1	קולנוע ביתי	23.7	שטיח אקוסטי	2.90
B2	חדר כושר / יוזה	41.0	פריקט ספורט	2.90
B3	טרקלין וגר	37.8	פורצלן 120/120	2.90
B4	חדר אורחים	20.6	פריקט עץ	2.90
B5	רחצה אורחים	7.6	פורצלן 60/120	2.60
B6	ספא - סאונה ומקלחת	5.9	אבן טבעית	2.60
B7	מחסן	9.5	פורצלן 60/60	2.60
B8	חדר טכני	12.3	בטון מוחלק	2.90
B9	מרחץ יין	2.8	אבן טבעית	2.60
B10	מבואה ומדרגות	17.4	פורצלן 120/120	2.90
B11	מסדרון ושקוע	30.0	אבן לריכר	-
	סה"כ פנים (טוט)	178.6		

תכנית קומת מרתף

ק"מ 1:100

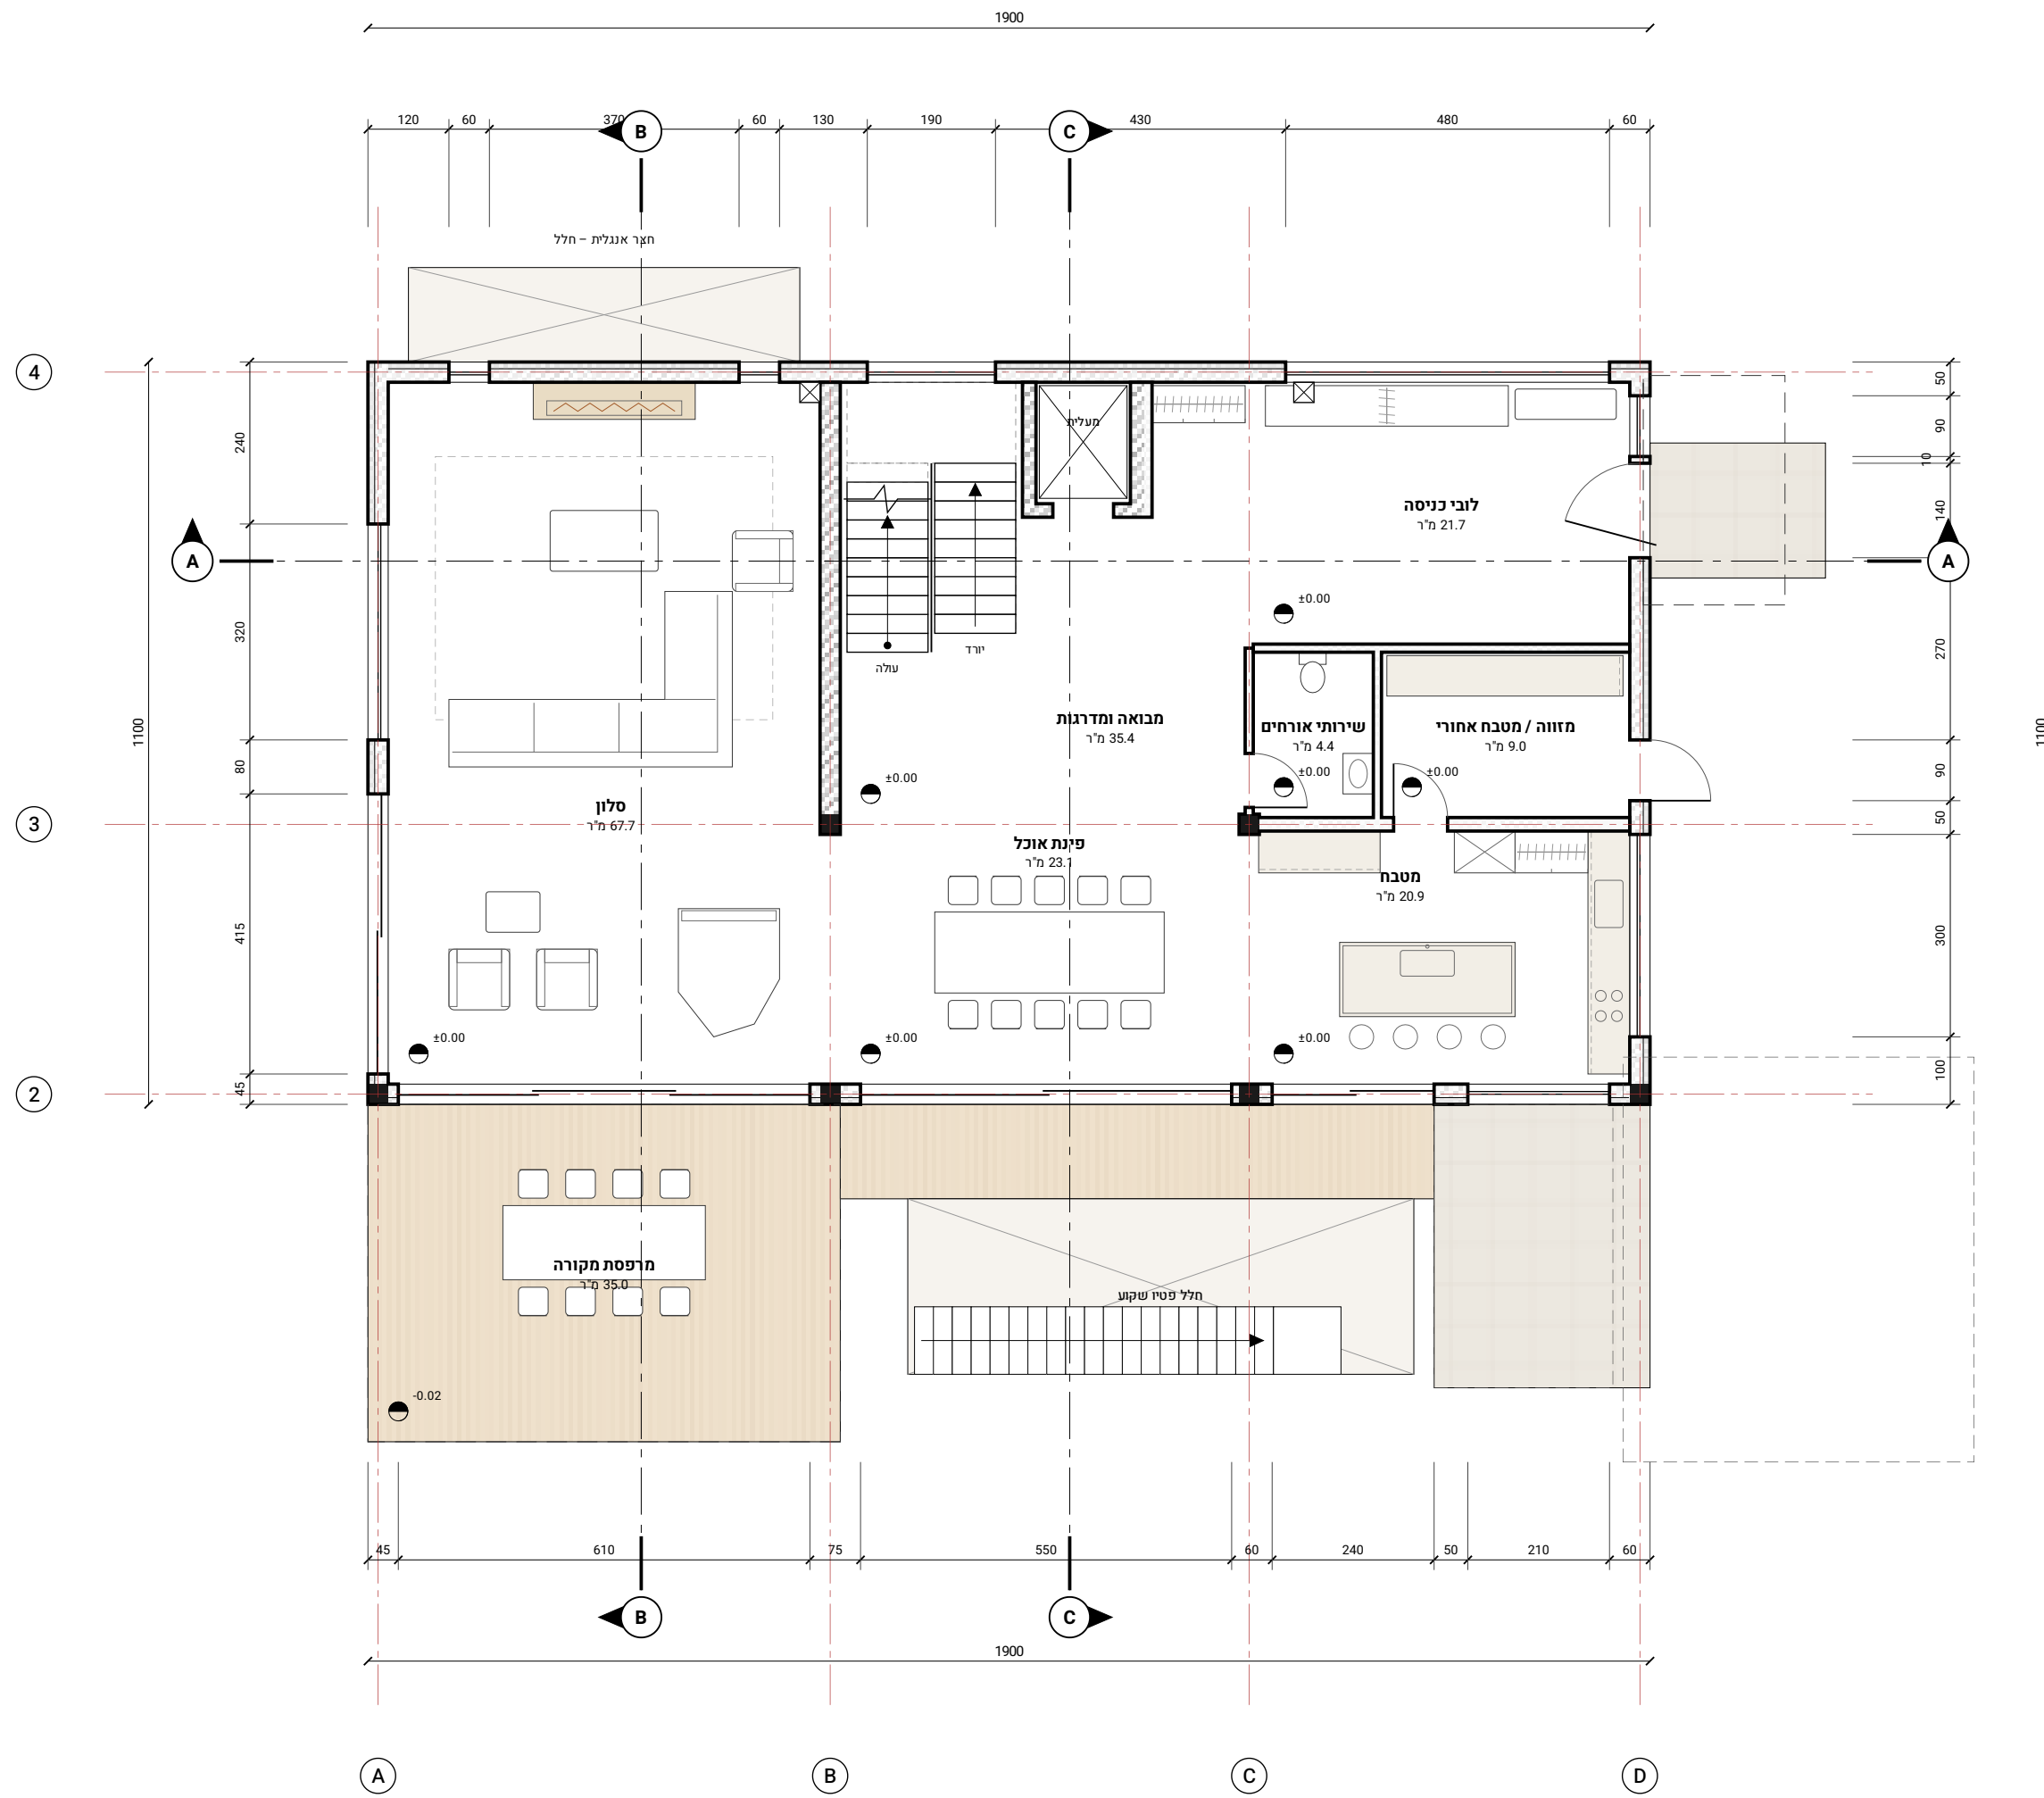

טבלת חללים - קומת קרקע

מס'	חלל	שטח מ"ר	ריצוף	ג. תקרה
G1	סלון	67.7	פורצלן 120/120	3.10
G2	פינת אוכל	23.1	פורצלן 120/120	3.10
G3	מטבח	20.9	פורצלן 120/120	3.00
G4	מבואה ומדרגות	35.4	פורצלן 120/120	3.10
G5	שירותי אורחים	4.4	פורצלן 60/120	2.60
G6	מזווה / מטבח אחורי	9.0	פורצלן 60/60	2.60
G7	לובי כניסה	21.7	אבן טבעית	3.10
G8	מחסן מרתף	35.0	דק עץ טיק	-
	סה"כ פנים (טוט)	182.2		

תכנית קומת קרקע

ק"מ 1:100

