

בית כורכר

BEIT KURKAR

שם הפרויקט:
וילת בוטיק בקיסריה

מיקום הפרויקט:
קיסריה, רובע 13 (מגרש לימודי)

מנהל:
שירן שריקי

שם הבניין:
תכניות קומה א' וגג

מס' בניין:
07




ק"מ:
1:100

רשימת ניליונות:	
01 שער	
02 קונסטרוקציה ומחיצות	
03 ניתוח אדריכלי וסביבתי	
04 תכנית העמדה וסכמת שטחים	1:200
05 תכנית פיתוח שטח	1:100
06 תכנית פרקט וקרקע	1:100
07 תכנית קומה א' וגג	1:100
08 חיתות	1:100
09 חתכים	1:100
10 סכמת סטטיות	1:100
11 תכנית קומה א'	1:50
12 תכנית קומה א'	1:50
13 חיתות	1:50
14 חתך A-A	1:50
15 חתך B-B	1:50
16 ניליון מדרגות	1:25, 1:5
17 פרטי בניין	1:20, 1:5
18 רשימת אלמנטים וגזרות	1:50
19 עיצוב ריהוט - חלל המגורים	1:50
20 עיצוב ריהוט - אי המטבח	1:25, 1:10, 1:2
21 דרימות חוץ	
22 דרימות פנים	
23 תודה	

מנהל:
הנדסאים - אדריכלות ועיצוב פנים


שם המעשה/ת.ד.:

תאריך:
10.2026

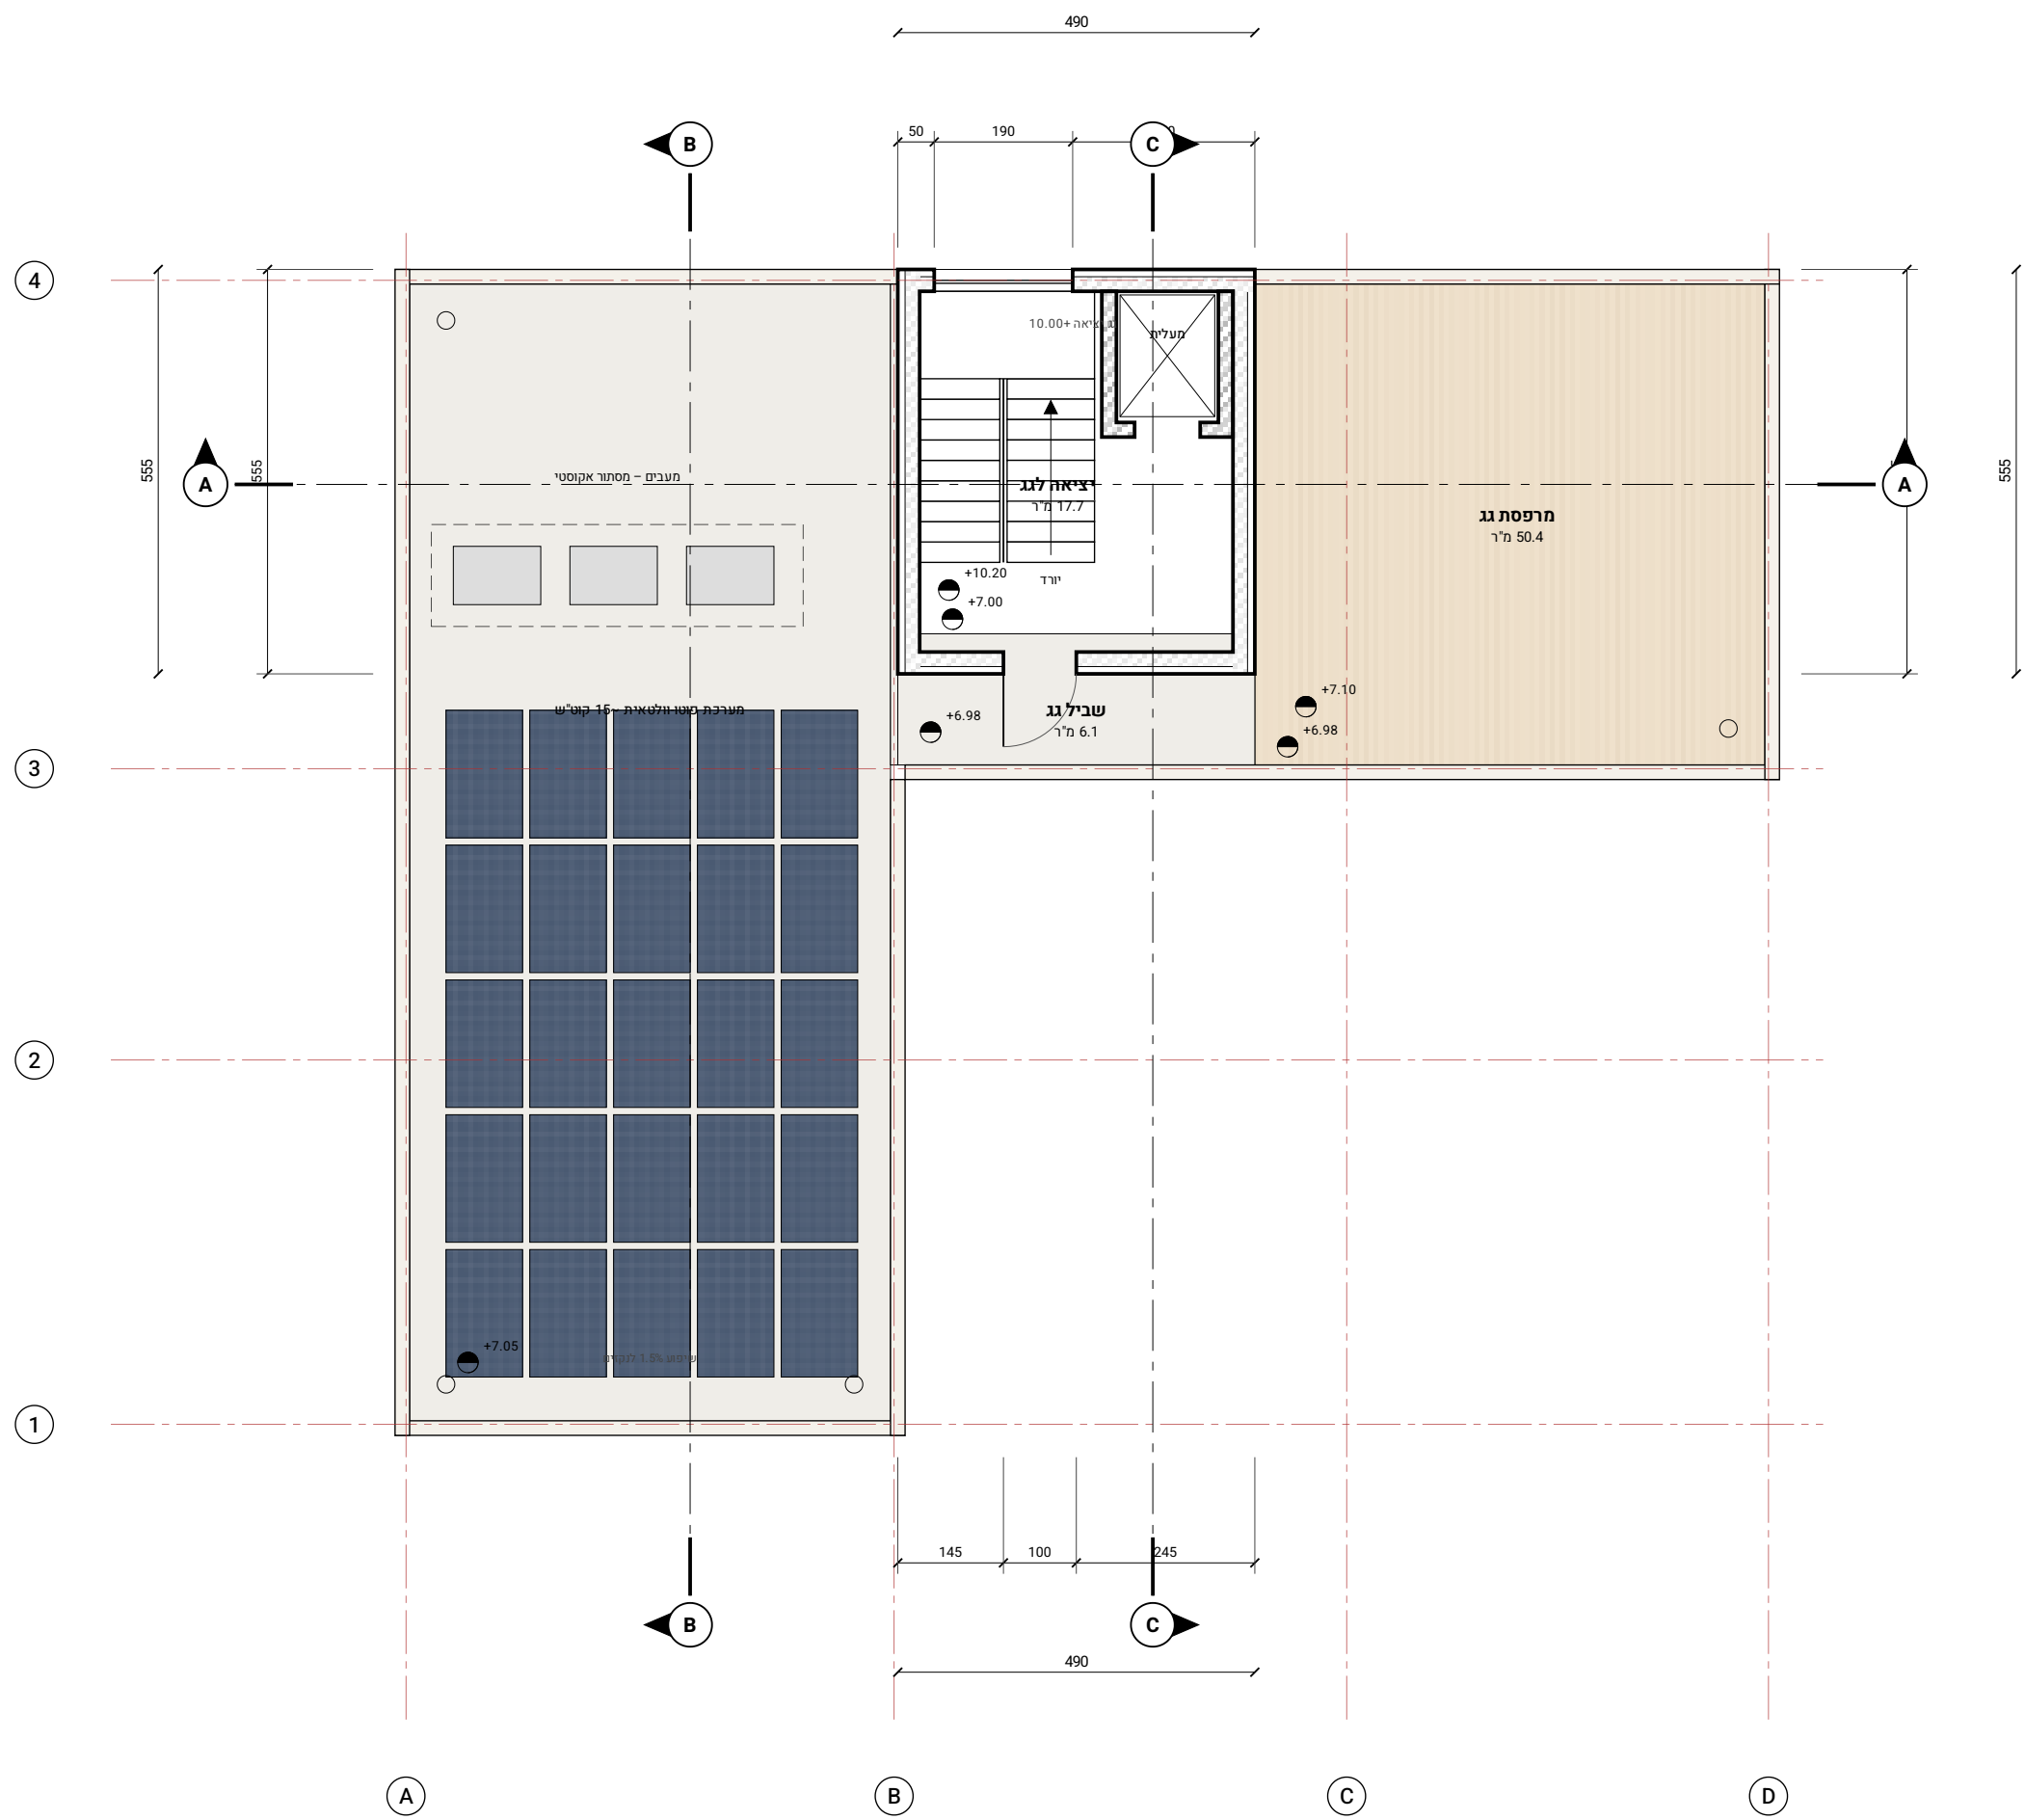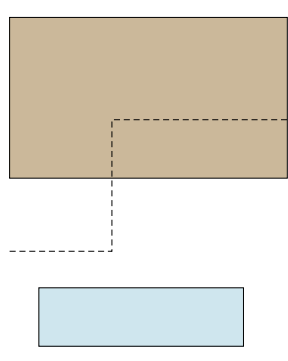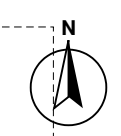

טבלת חללים - תכנית ג

חלל	שטח מ"ר	ריצוף	ג. תקרה
חלל	17.7	פריקט אלון	3.00
חדר שינה	50.4	דק עץ	-
שטח פנים (טו)	6.1	אריזי דק	-
סך הכל	17.7		

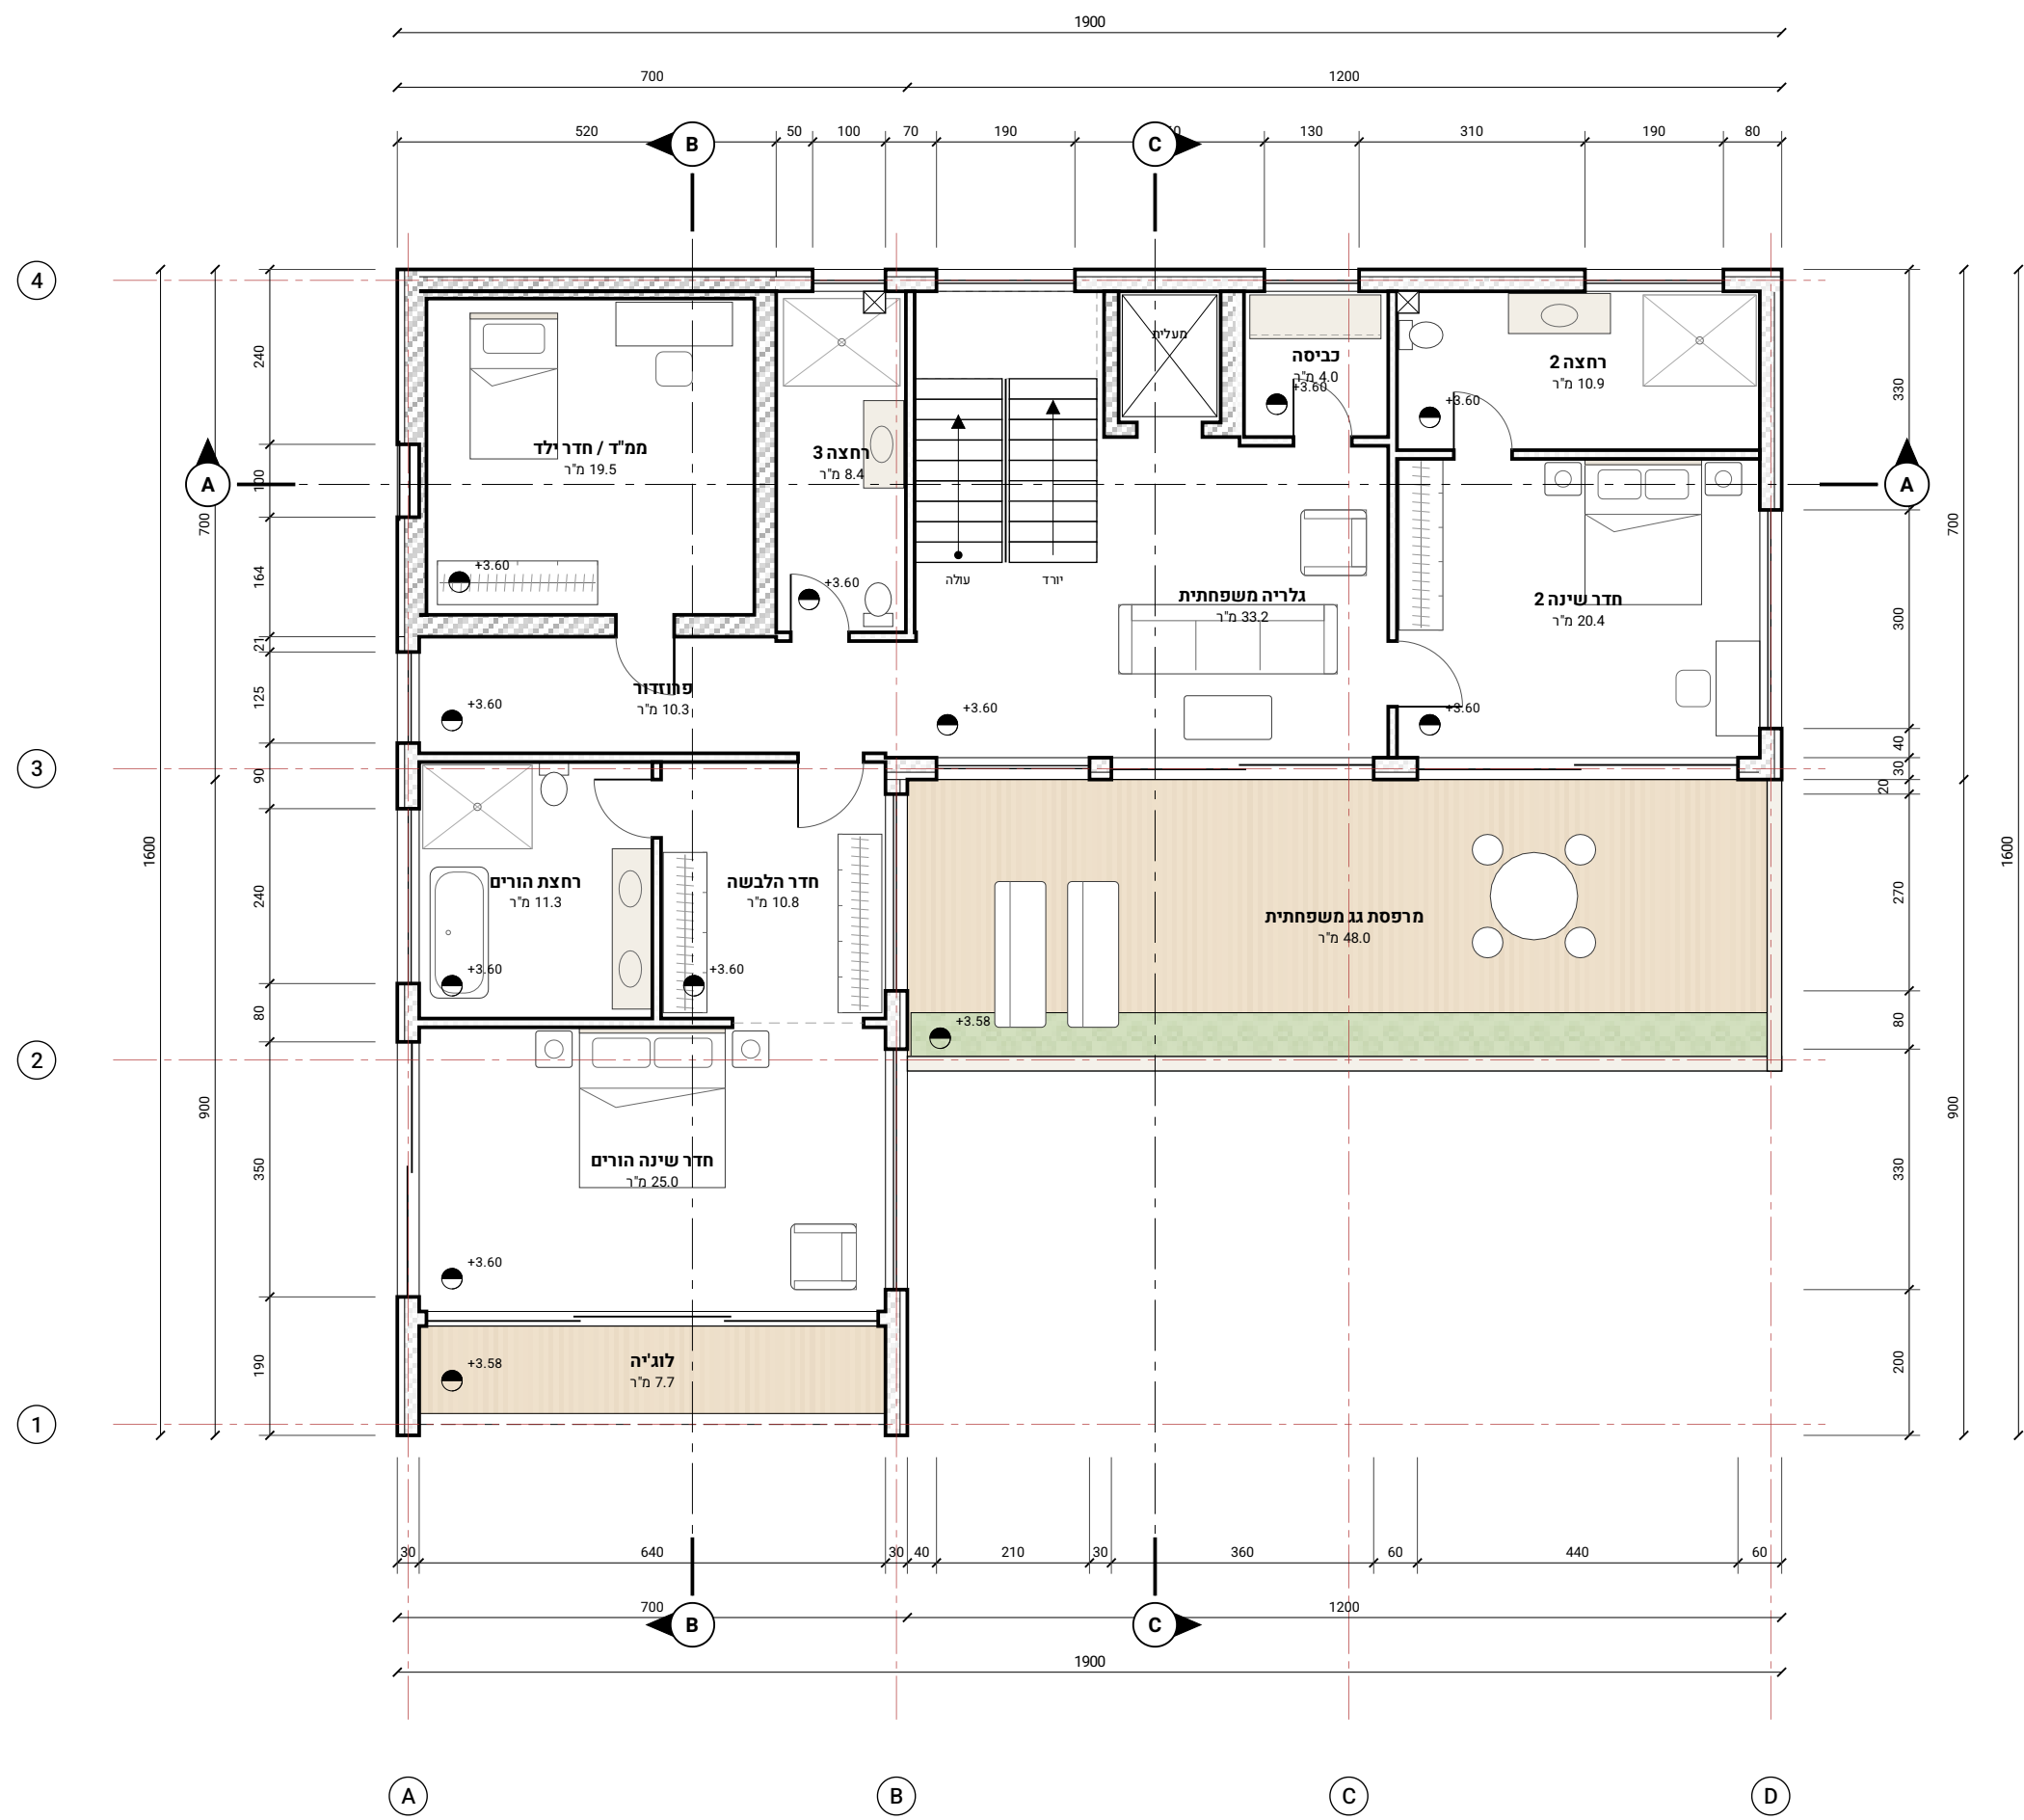

טבלת חללים - קומה א'

חלל	שטח מ"ר	ריצוף	ג. תקרה
חדר שינה	25.0	פריקט אלון	2.80
לובי	7.7	דק עץ	-
חדר שינה	11.3	אבן טבעית 60/120	2.70
חדר הלבשה	10.8	פריקט אלון	2.70
פרוזדור	10.3	פריקט אלון	2.70
מסדר / חדר ילד	19.5	פריקט אלון	2.60
חדר 3	8.4	פריקט אלון 60/120	2.60
חדר 2	33.2	פריקט אלון	2.80
חדר 1	4.0	פריקט אלון 60/60	2.60
חדר 2	20.4	פריקט אלון	2.80
חדר 2	10.9	פריקט אלון 60/120	2.60
חדר 2	48.0	דק עץ / אבן	-
סך הכל	153.8		

תכנית ג

ק"מ 1:100

תכנית קומה א'

ק"מ 1:100

