

בית כורכר



BEIT KURKAR

שם הפרויקט:

וילת בוטיק בקיסריה

מיקום הפרויקט:

קיסריה, רובע 13 (מגרש לימודי)

מנהל:

שירן שריקי

שם הבניין:

חזיתות

מס' בניין:

08

ק"מ:

1:100

רשימת ניליונות:

01 שער

02 קונסטרוקציה ומחיצה

03 ניתוח אזור וסביבה

04 תכנית העמדה וסלול שטחים

05 תכנית פיתוח שטח

06 תכנית פרקט וקרקע

07 תכנית קומה א' ונג'

08 חזיתות

09 חתכים

10 סכומות סטטיות

11 תכנית קומה א'

12 תכנית קומה א'

13 חזיתות

14 חתך A-A

15 חתך B-B

16 נילון מדרגות

17 פרטי בניין

18 רשימת אלומות ונגרות

19 עיצוב פנים - חלל המגורים

20 עיצוב ריהוט - אי המטבח

21 רחבת חצר

22 רחבת פנים

23 חזית



מנהל:

הנדסאים - אדריכלות ועיצוב פנים

שם המעשה/ת.ל.:

תאריך:

10.2026

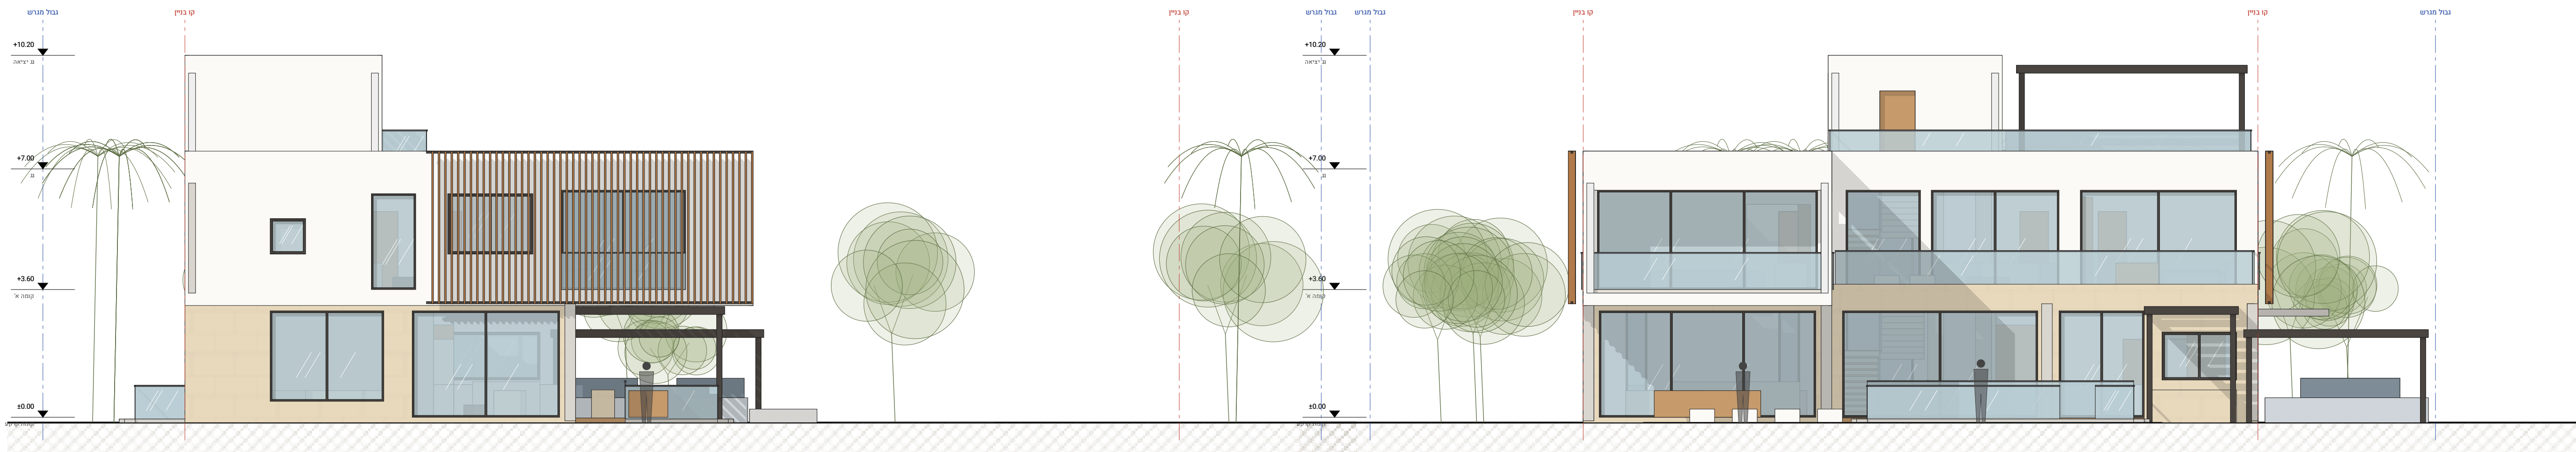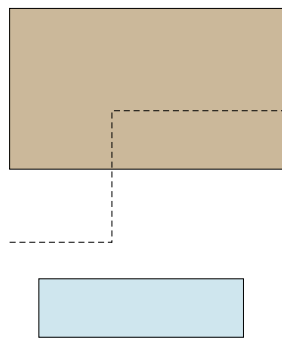

חזית מערבית

קנ"מ 1:100

חזית דרומית

קנ"מ 1:100



חזית מזרחית

קנ"מ 1:100

חזית צפונית

קנ"מ 1:100