



בית כורכר

BEIT KURKAR

שם הפרויקט:
וילת בוטיק בקיסריה

מיקום הפרויקט:
קיסריה, רובע 13 (מגרש לימודי)

שטח:
שטח שרידי

שם הבניין:
סכמה סטטית

מס' בניין:
10

מס' קטע:
1:100

רשימת ניליונות:




01	שטח
02	קונסט ומחיר
03	ניתוח אזור וסביבה
04	תכנית העמדה וסכמת שטחים
05	תכנית פיתוח שטח
06	תכנית פרקט וקרקע
07	תכנית קומה א' ונג
08	חיתות
09	חיתות
10	סכמות סטטיות
11	תכנית קומה א'
12	תכנית קומה ב'
13	חיתות
14	חיתות A-A
15	חיתות B-B
16	גיליון מדרגות
17	פרטי בניין
18	רשימת אלומיניום ונרות
19	עיצוב פנים - חלל המגורים
20	עיצוב ריהוט - אי המטבח
21	ריהוט חוץ
22	ריהוט פנים
23	חודה

מנהל:
הנדסאים - אדריכלות ועיצוב פנים

שם המעשה/ת.ד.:


תאריך:

10.2026

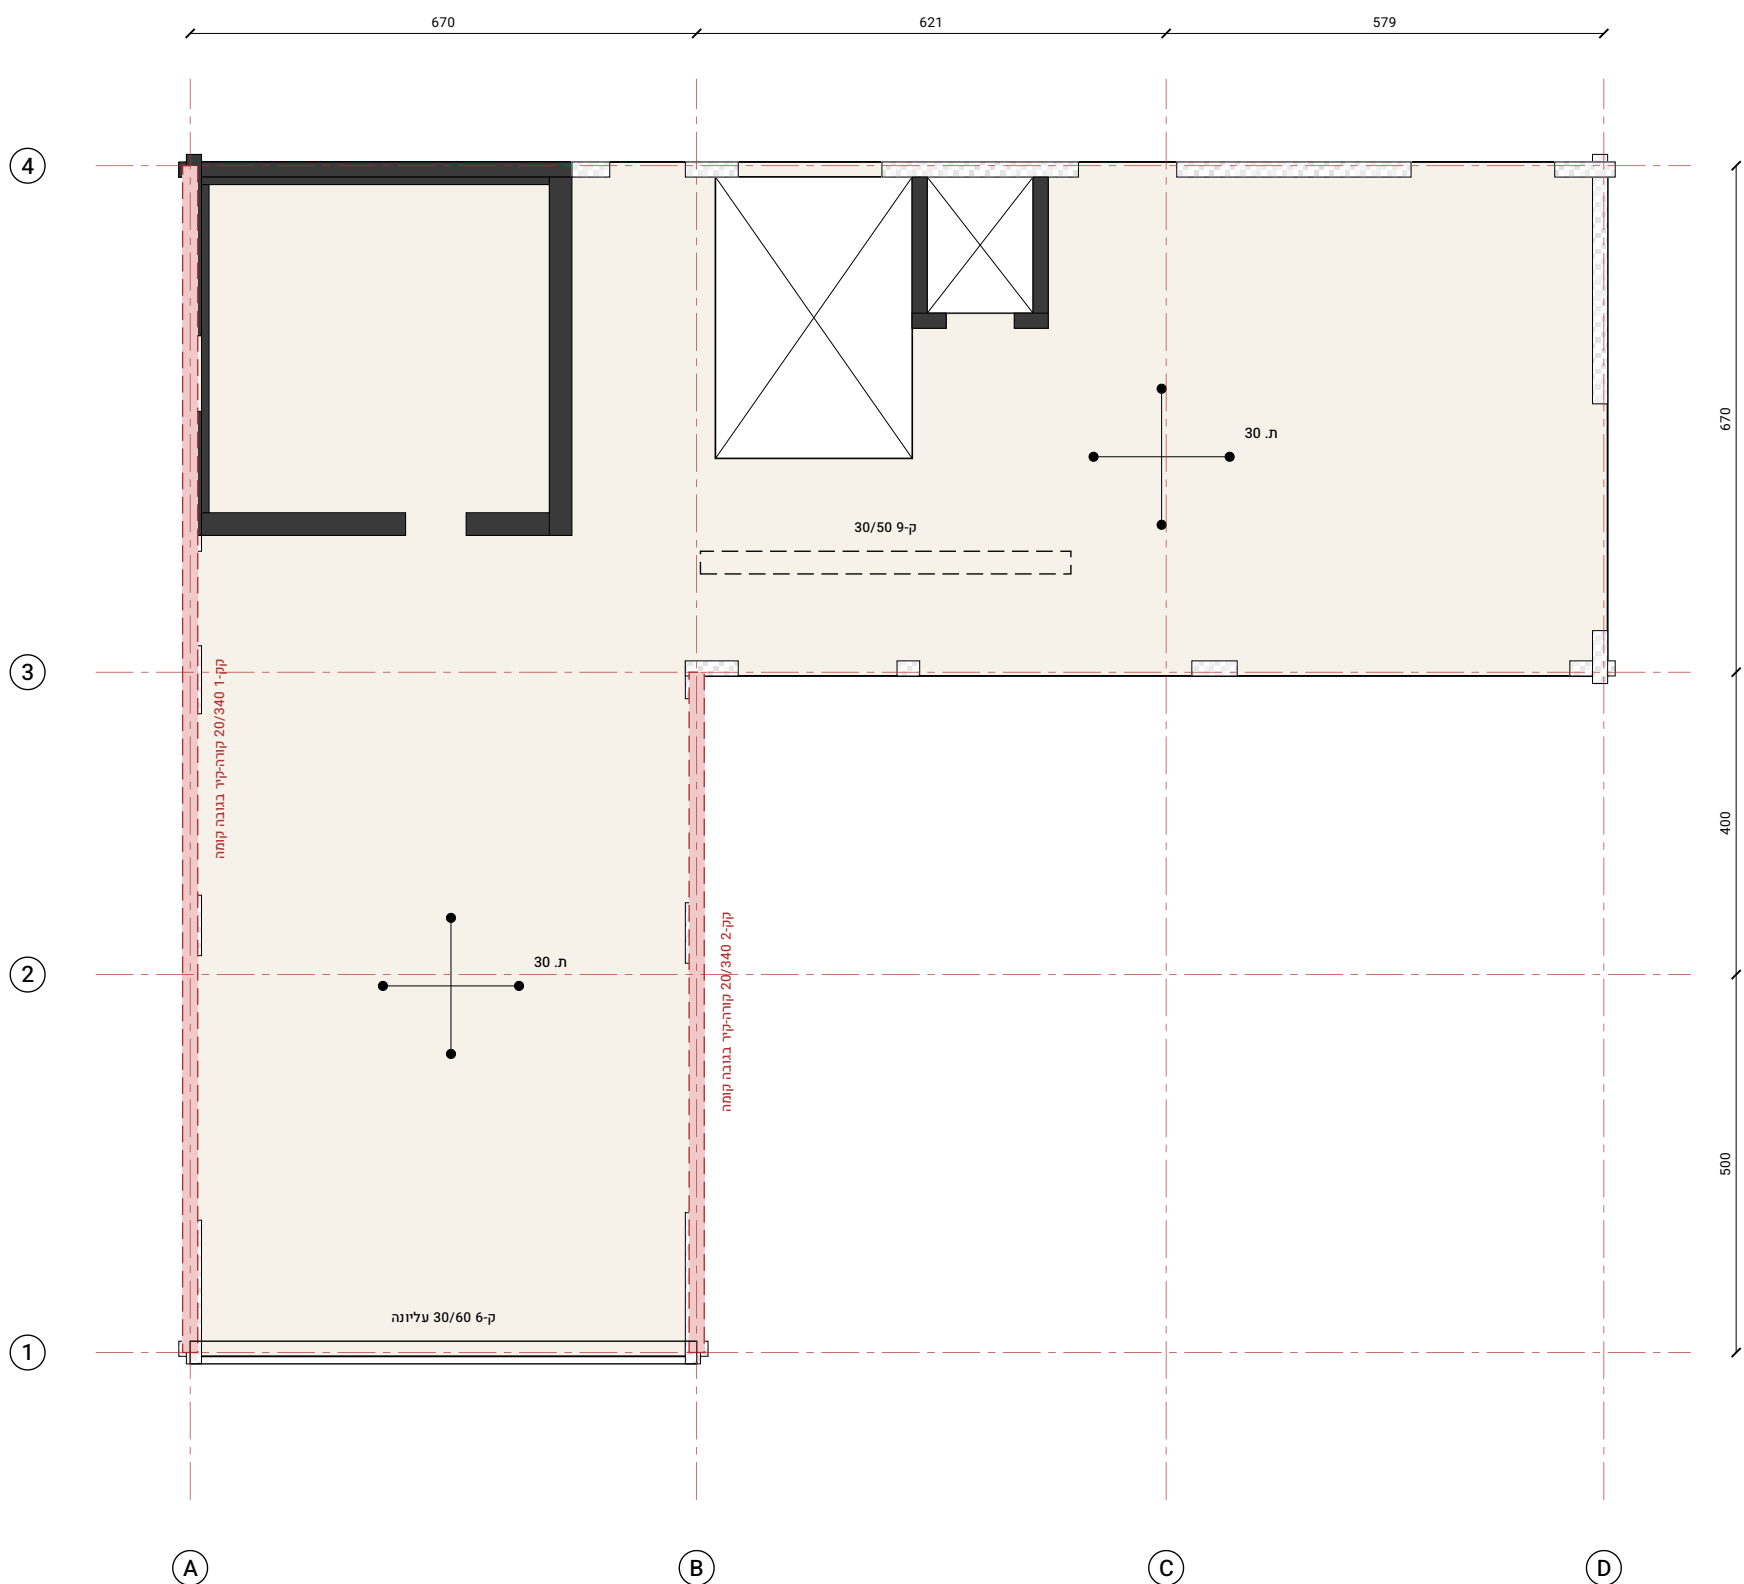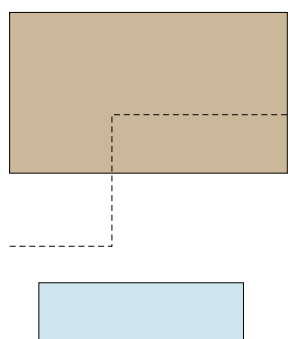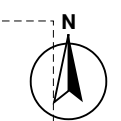


סכמה סטטית תקרה +7.00

קנ"מ 1:100

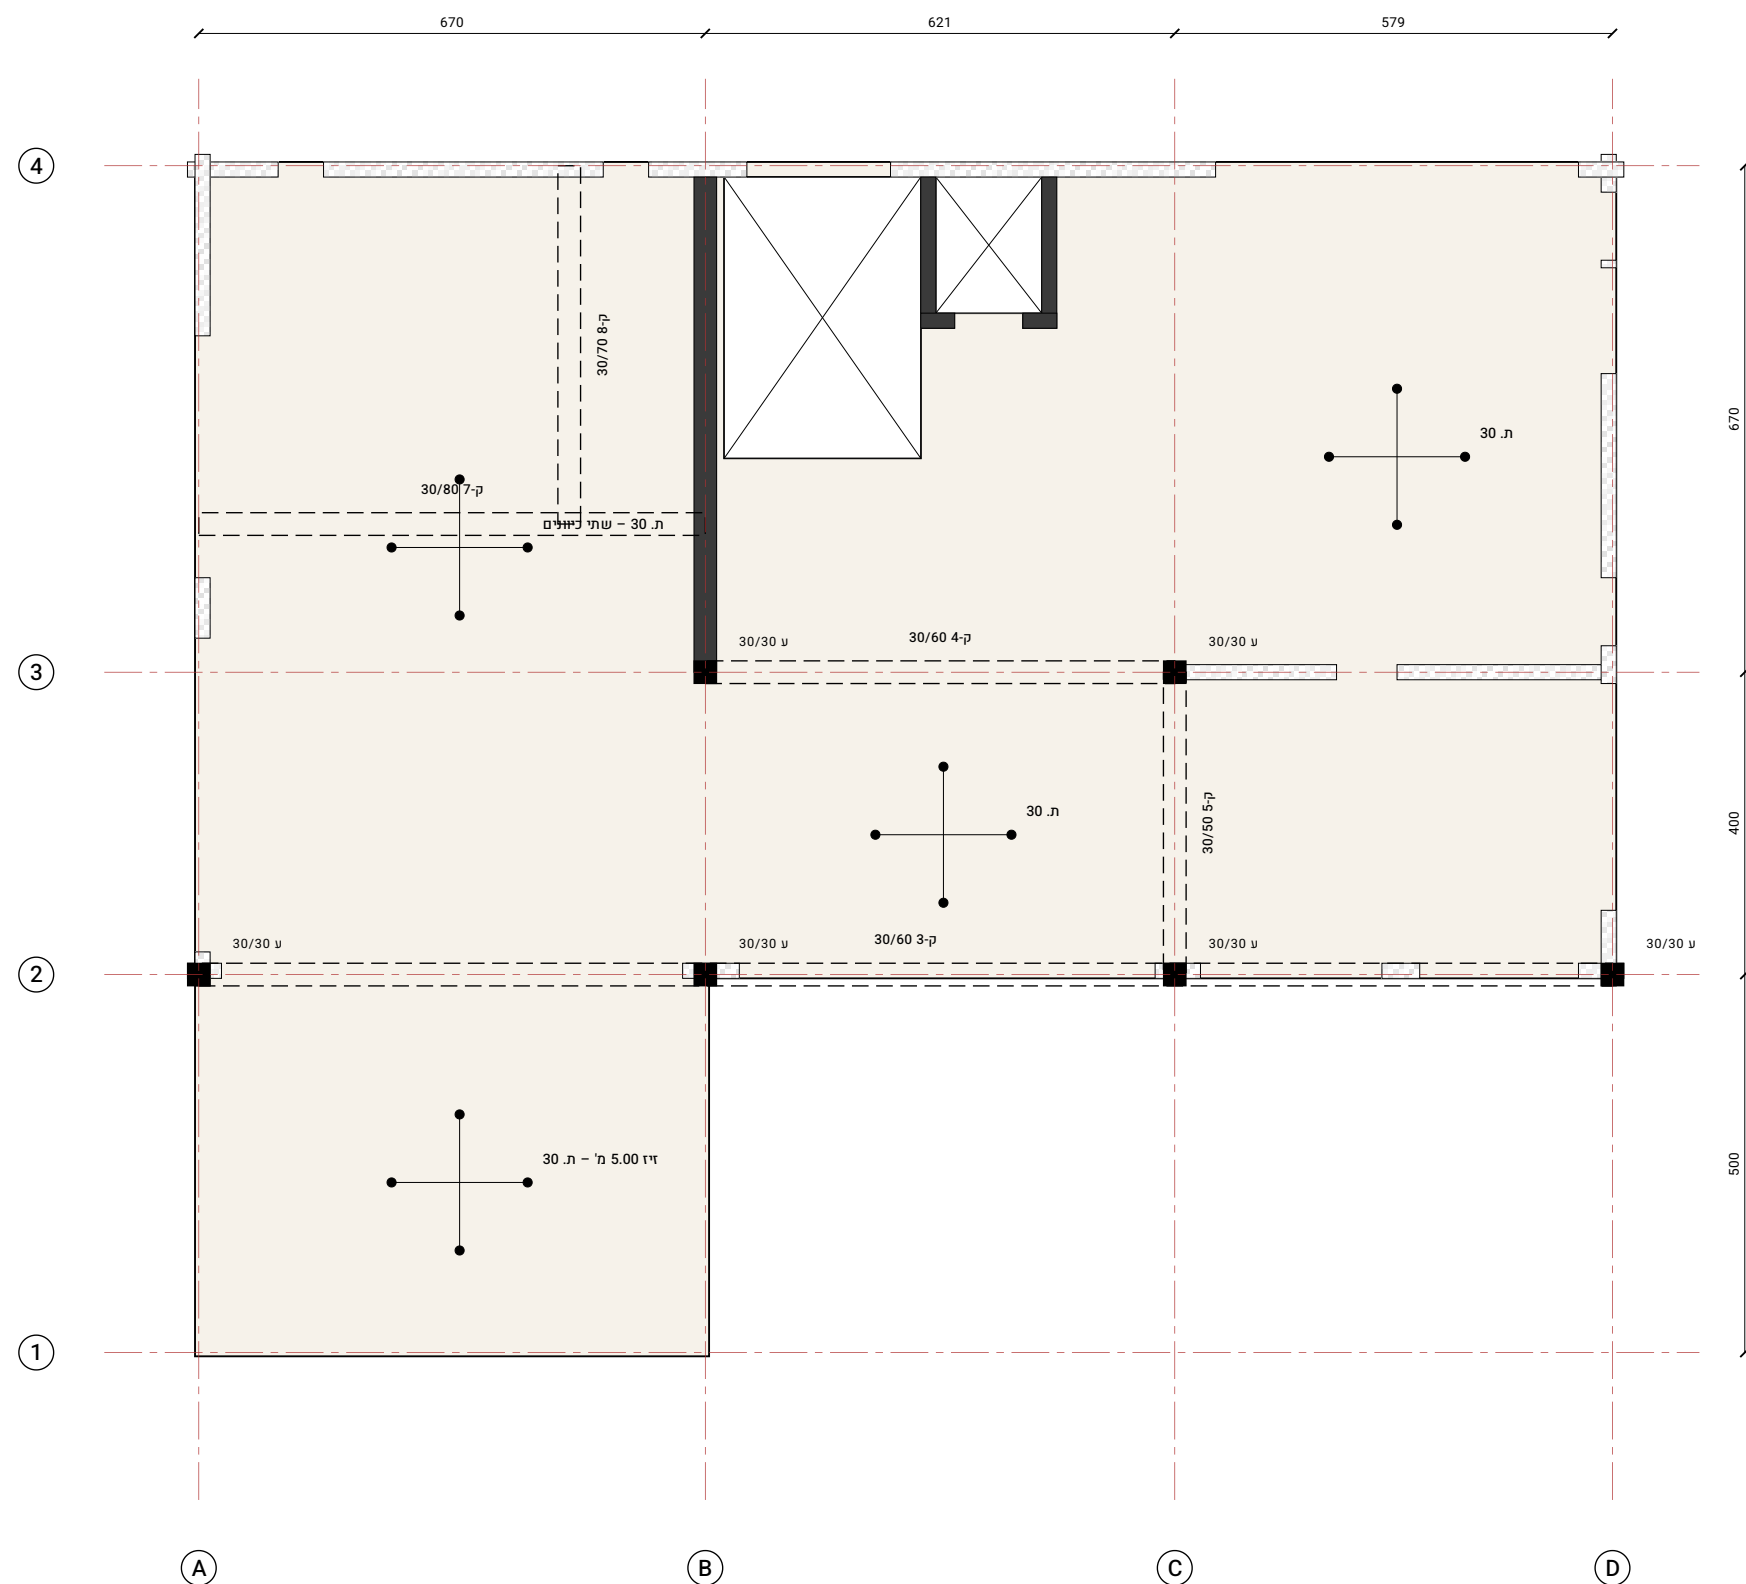

סכמה סטטית תקרה +3.60

קנ"מ 1:100

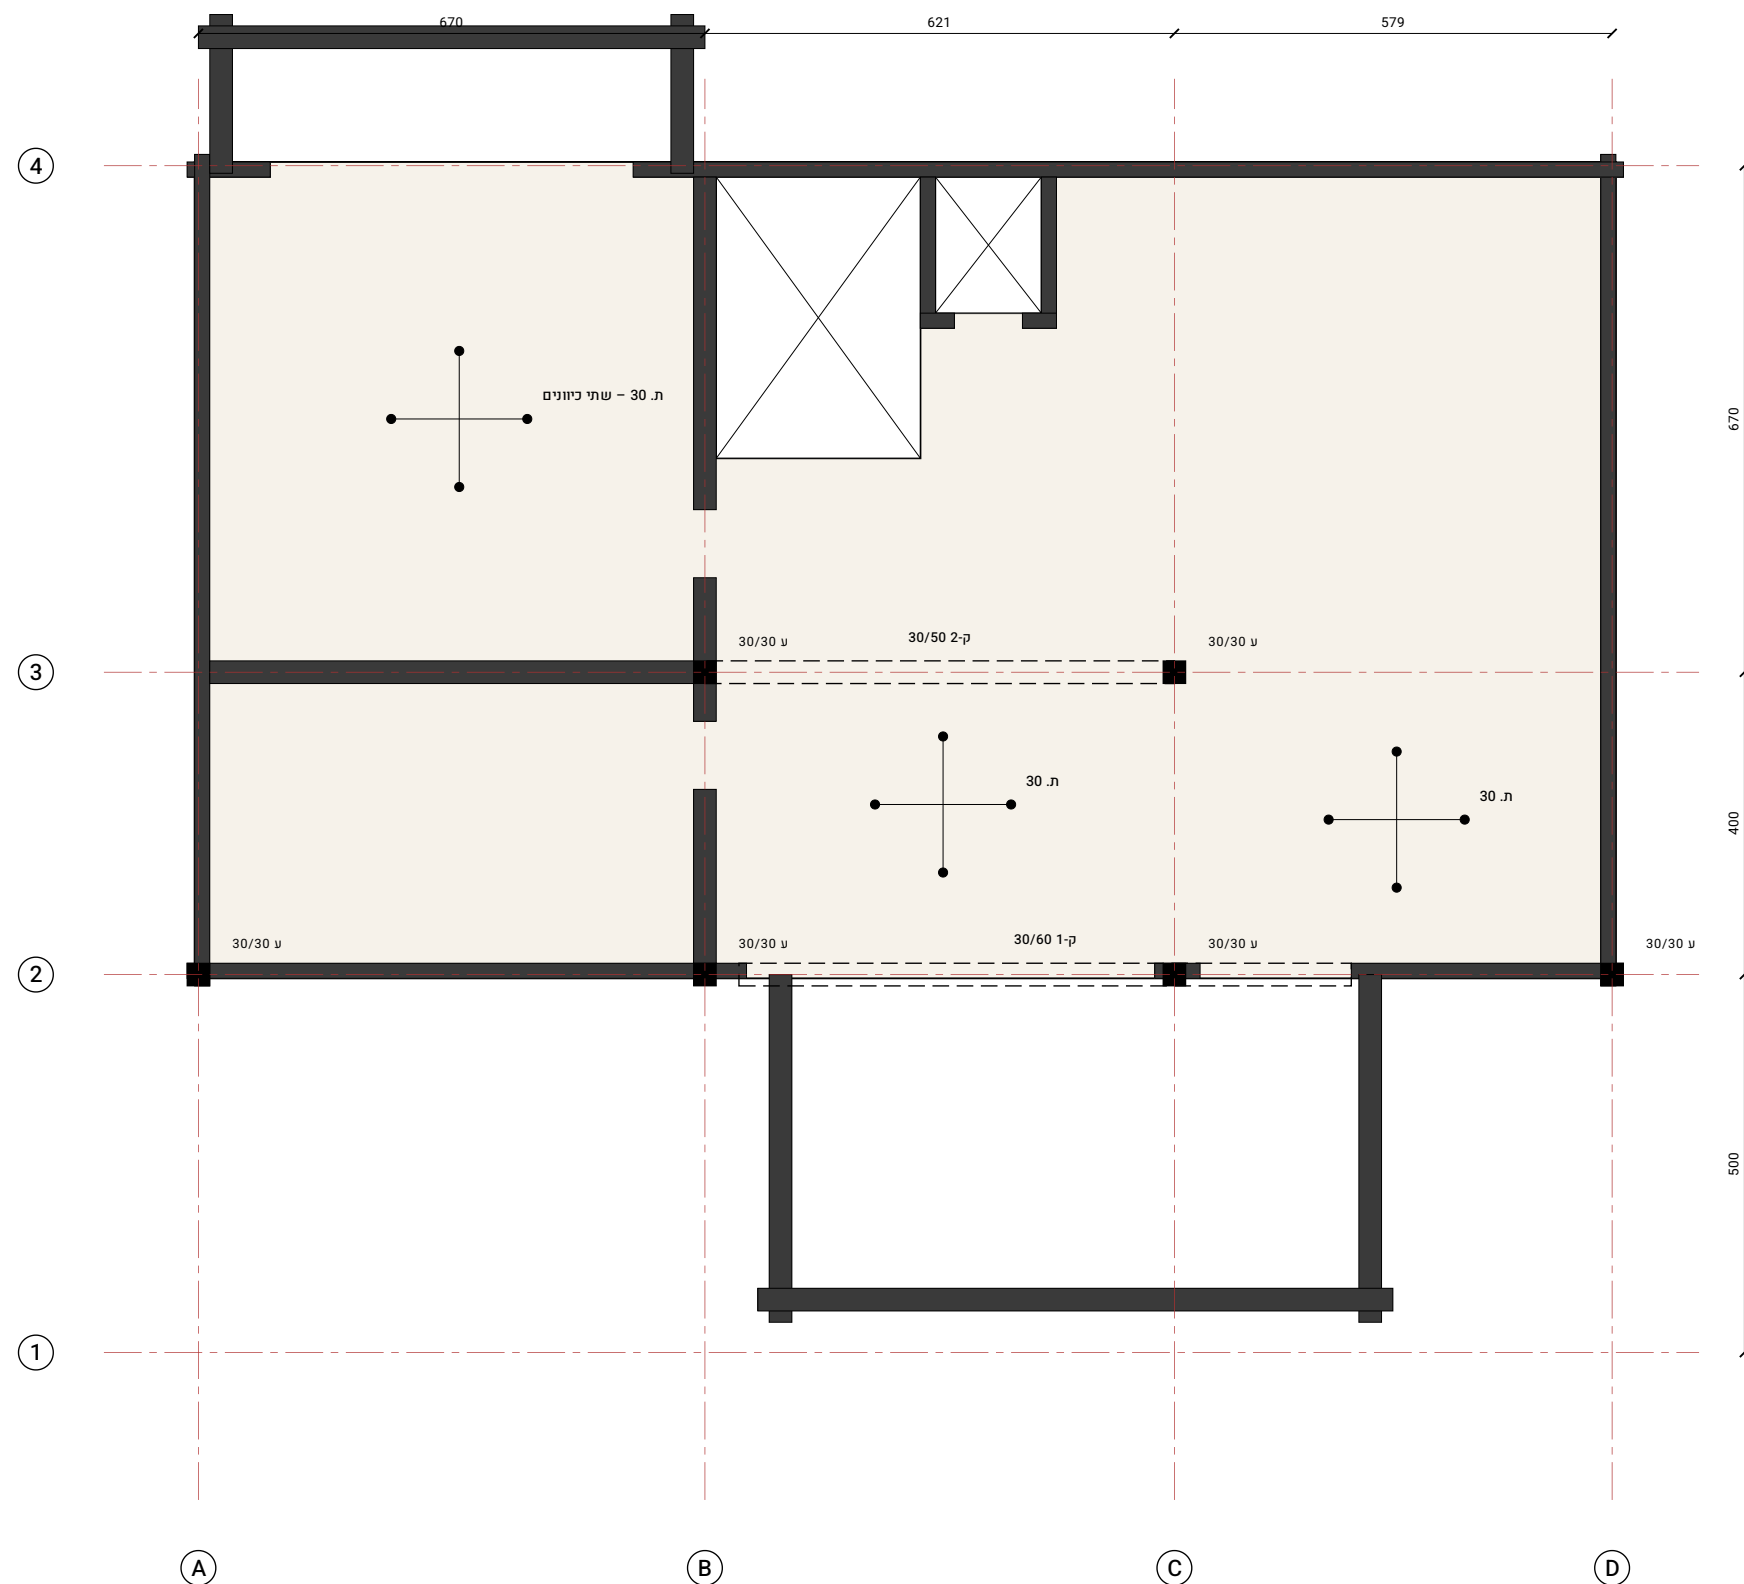

סכמה סטטית תקרה ±0.00


קנ"מ 1:100

מקרא:

- קיר בטון מזוין נושא (קירות מחך, פיר מעלית, מח"ר, קיר ג"ק)
- קיר בלוק נושא 20
- עמוד ב"מ 30/30
- קורה תחתונה (ק-אא רוחב/גובה ס"מ)
- קורה-קיר בגובה קומה - נושאת את חצי
- תקרה ב"מ מלאה ת. 30


עקרונות המערכת הקונסטרוקטיבית:

- שלד בטון מזוין וזיכ באחר: רפסודה 50, קירות תמך 30, תקרות מלאות 30.
- ריש הדומי (מ 5.00) יישא ע"י שני קירות-קורה בגובה קומה (קק-1, קק-2).
- הפועלים כקורות בגובה 3.40 מ' ומחשבים 10.7 מ' לאחר עד ציר 4 - יחס עונן 1.2.
- קיר הליבה (פיר מעלית + קיר האט) משמש קיר ביירה לנחוצות אופקיים (מ"י 413).
- יכסיו בטון מוגבר 5-4 ס"מ ובטון ב-40 לסביבה יחית (מ"י 466).
- כל המידות והיחידים לפי חישוב סטטי של מהנדס הקונסטרוקציה.

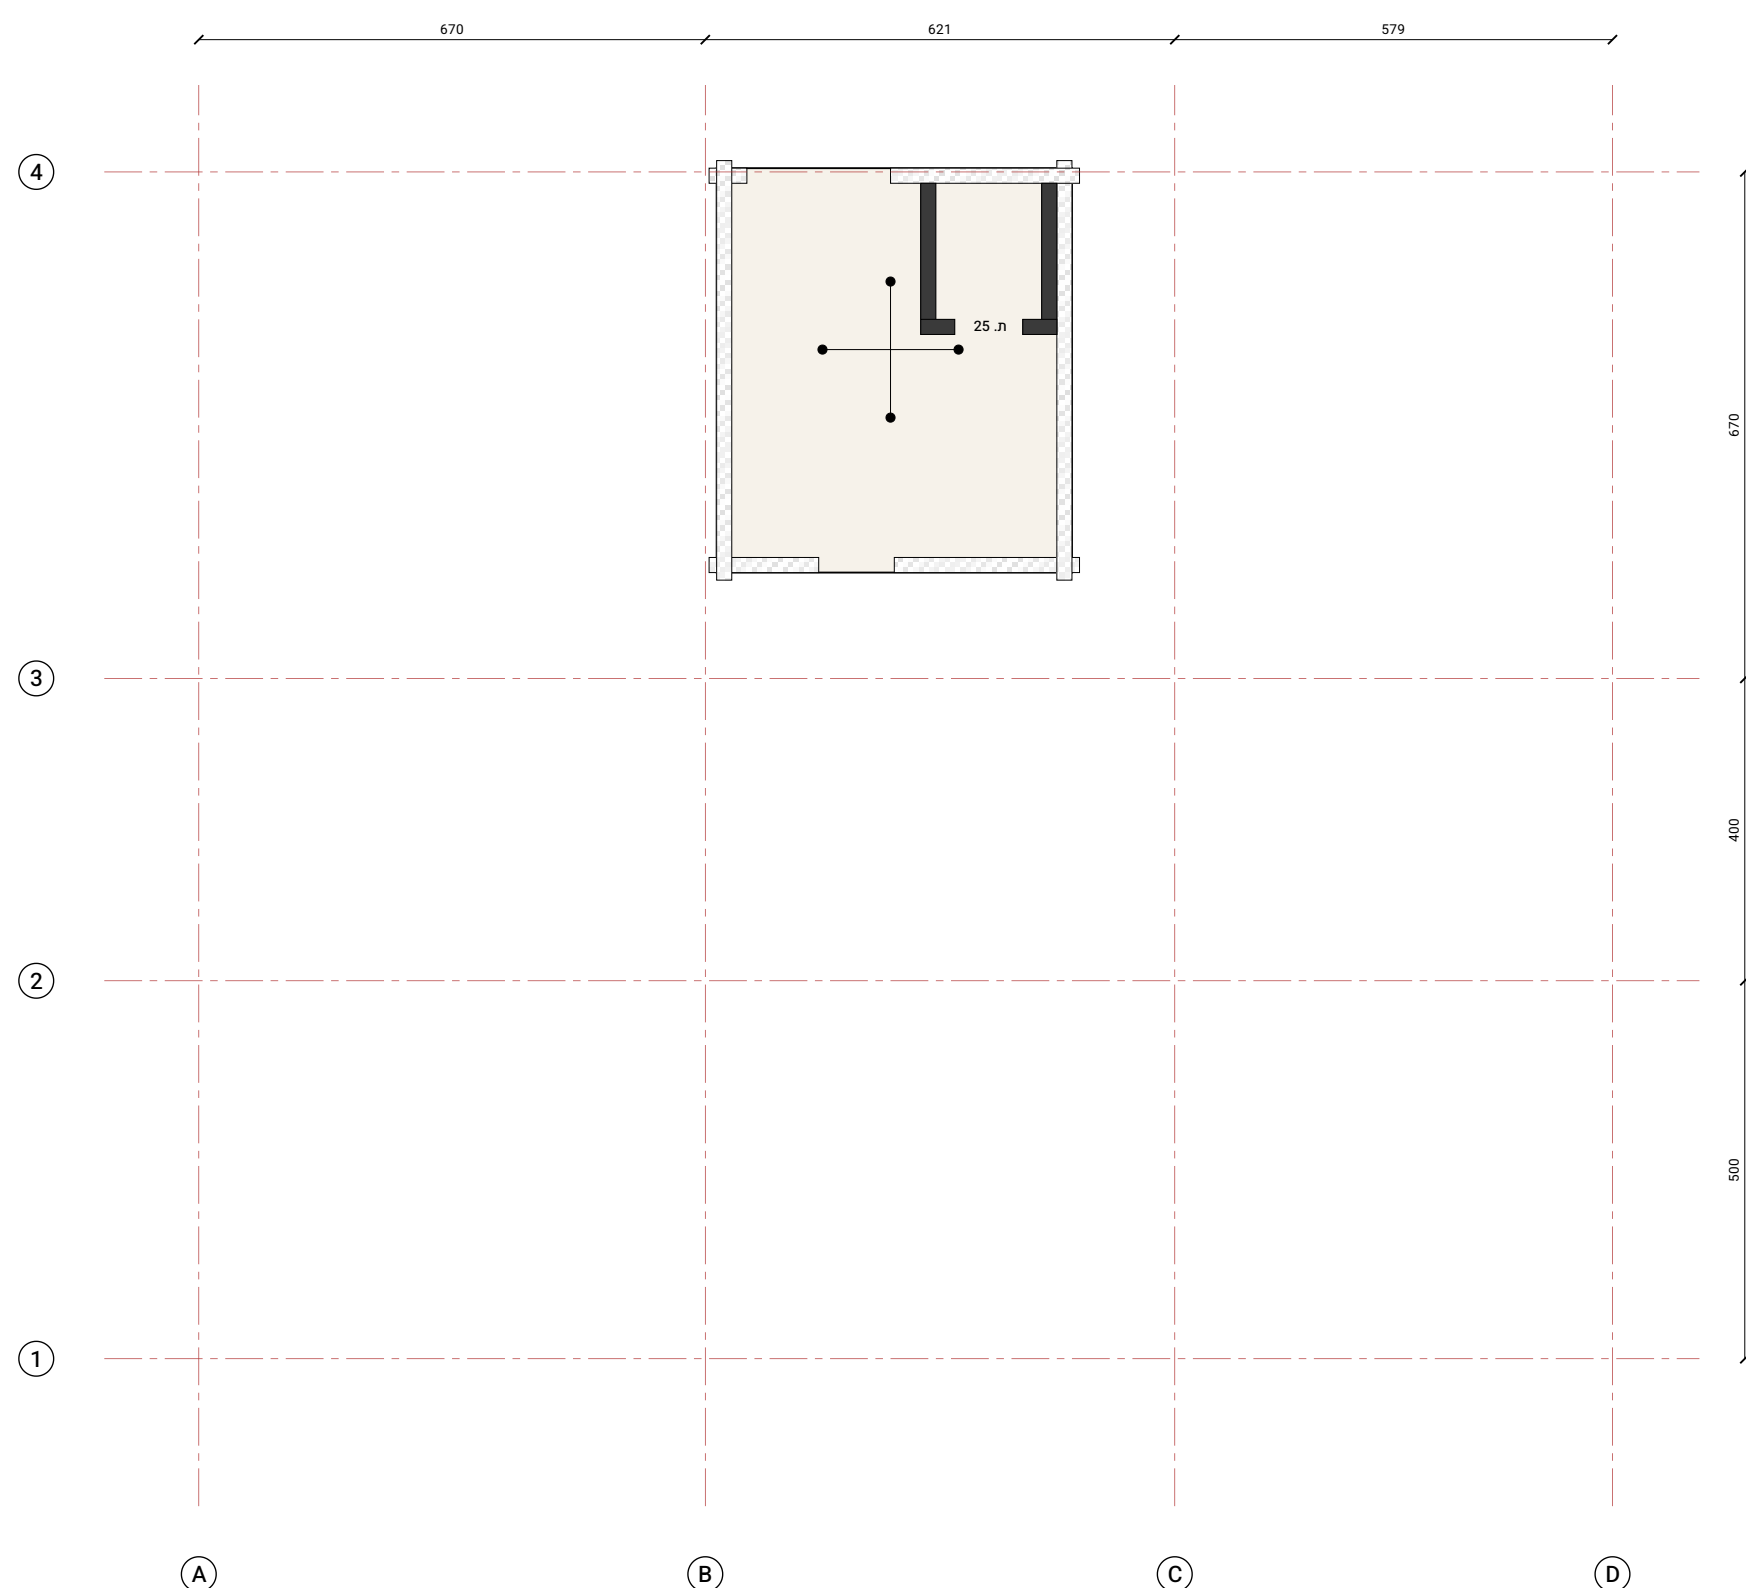

סכמה סטטית תקרה +9.80

קנ"מ 1:100

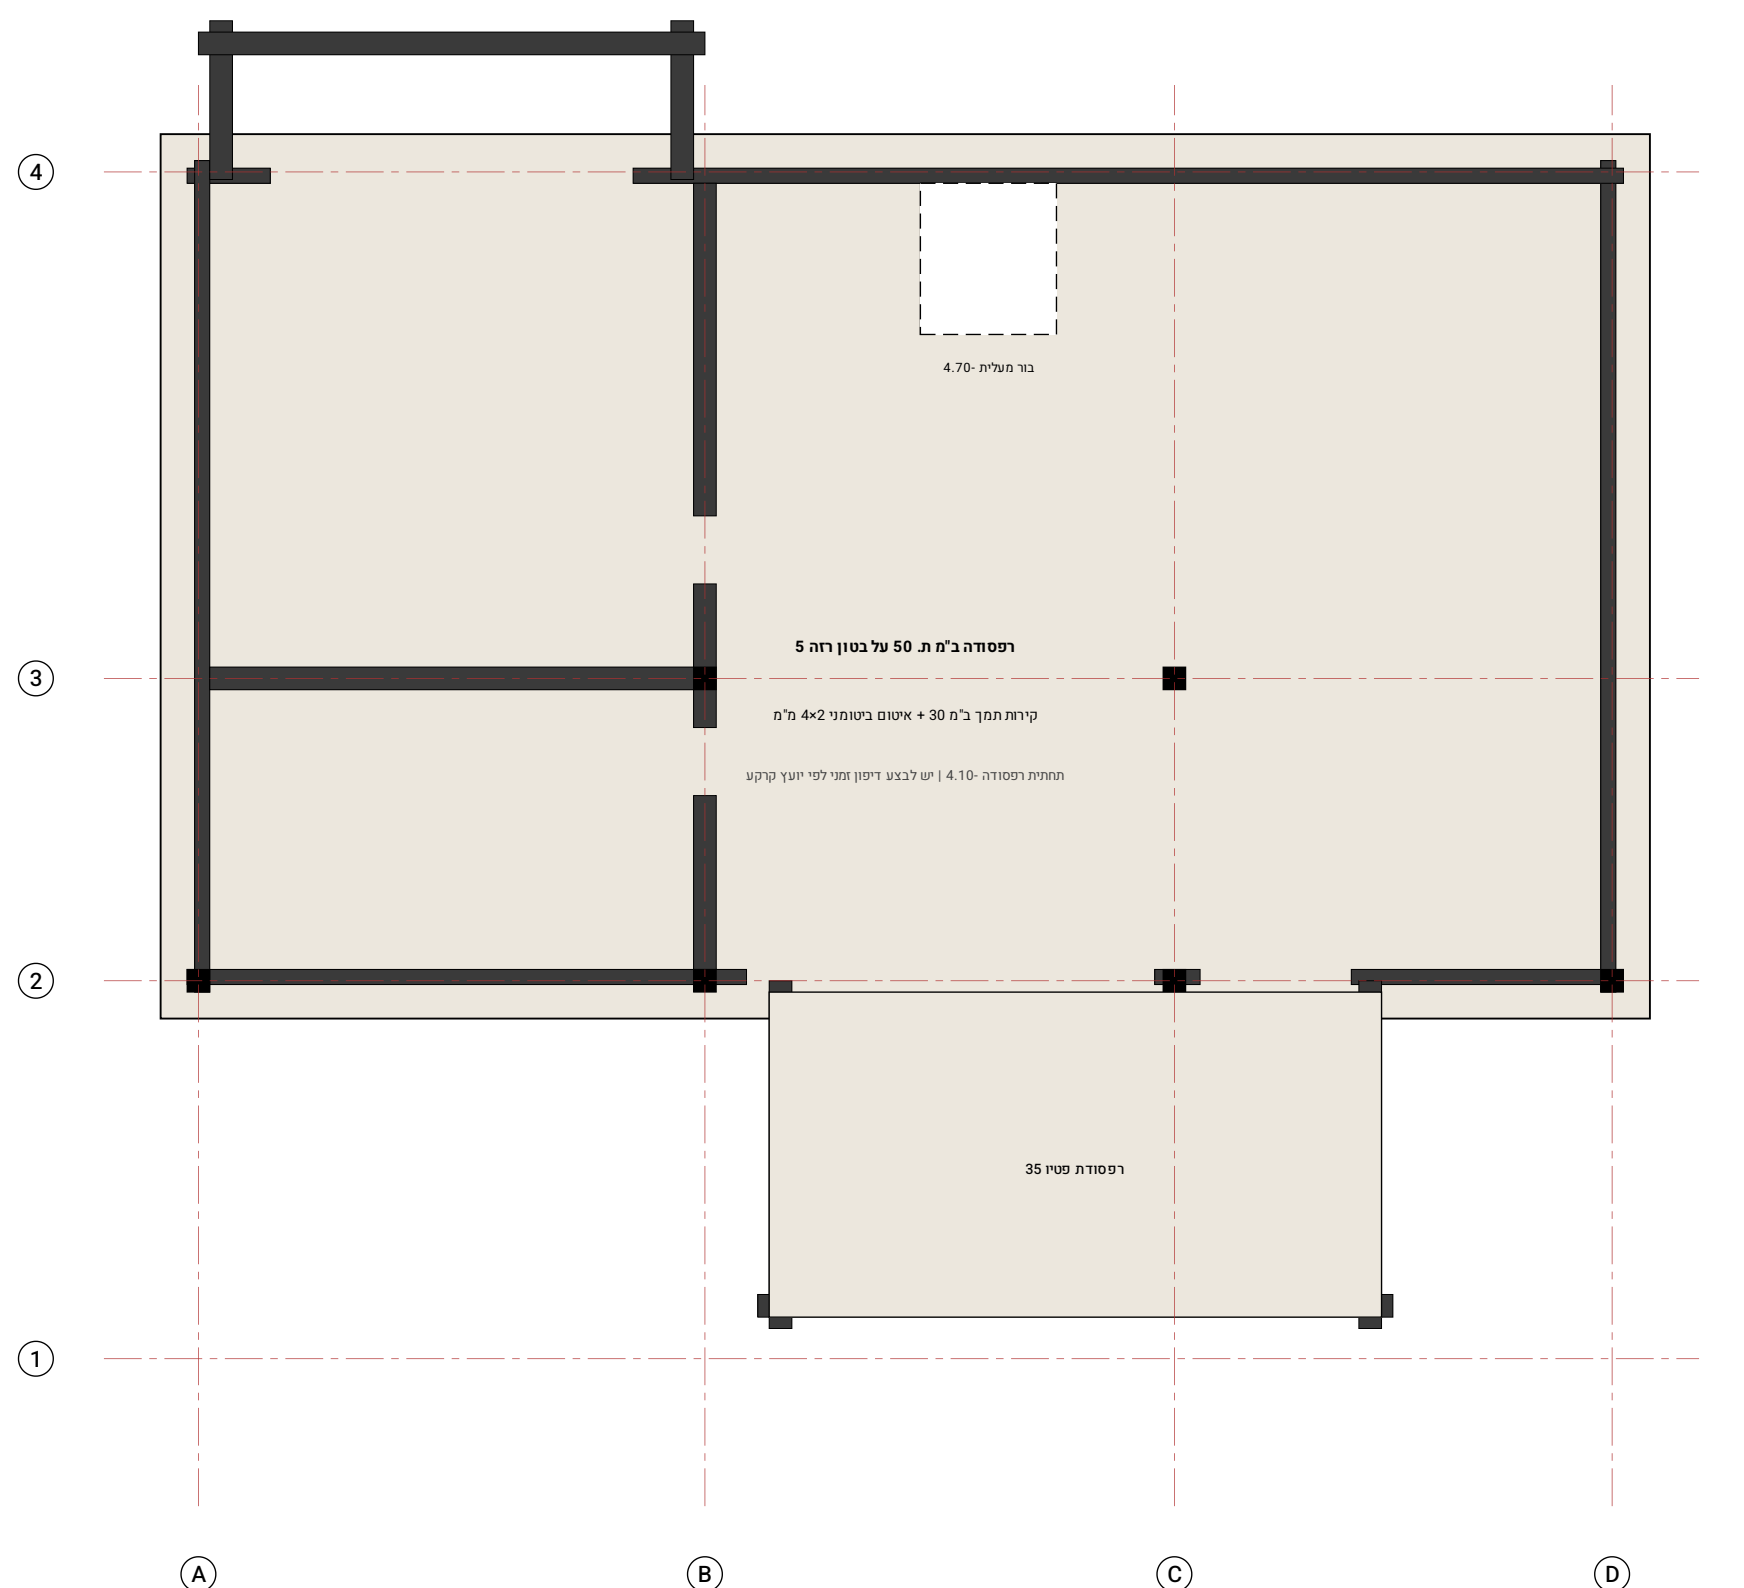

תכנית יסודות - רפסודה

קנ"מ 1:100