


בית כורכר

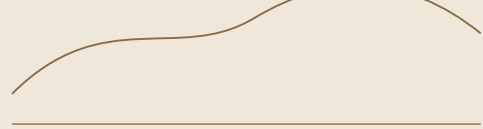

שם הפרויקט:

יולת בוטיק בקיסריה

מיקום הפרויקט:

קיסריה, רובע 13 (מגרש לימודי)

מנהל:

שירן שריקי

שם הבניין:

תכנית קומה א'

חסי גרילוק:

12

ק"מ:

1:50

רשימת נילוחות:

- | | |
|----|--------------------------|
| 01 | שער |
| 02 | קונסטרוקציה וחלקי |
| 03 | ניתוח אדריכלי וסביבה |
| 04 | תכנית העמדה וסלול שטחים |
| 05 | תכנית פיתוח שטח |
| 06 | תכנית פרקטיקה |
| 07 | תכנית קומה א' ונג |
| 08 | חיתות |
| 09 | חיתות |
| 10 | סכומות סטטיות |
| 11 | תכנית קומה א' ונג |
| 12 | תכנית קומה א' |
| 13 | חיתות |
| 14 | חיתות A-A |
| 15 | חיתות B-B |
| 16 | חיתות מדרגות |
| 17 | פרטי בניין |
| 18 | רשימת אלומיניום וגזרות |
| 19 | שיעור פנים - חלל המגורים |
| 20 | שיעור רחוב - אי המטבח |
| 21 | רשימת חוץ |
| 22 | רשימת פנים |
| 23 | חודש |

מנהל:

הנדסאים - אדריכלות ועיצוב פנים

שם המעשה/ת.ד.:

תאריך:

10.2026

תאריך:

10.2026

תכנית קומה א'

קנ"מ 1:50

הערות כלליות:

- המרחק בנ"מ, המפלגים במטרים, 18.50 +/- = 18.50 מ"מ על פני הים.
- קירות חוץ: בלוק בטון 20 + בידוד חיצוני 5 + חופי אבן/טיח חומי.
- קירות פנים: בלוק 10 חסיין / גבס דו-קושי לפי סיסטון.
- לכל מידות הפנים ולבדיקה ואישור בטוח לפני יצוא.
- מפלג לפי הנחיות פיקוד העורף - קירות ותקרה בטון מזוין 30.
- אלמנטים פורפיל חומי, צבע חגור דרומי, זיגוג בידודי Low-E.

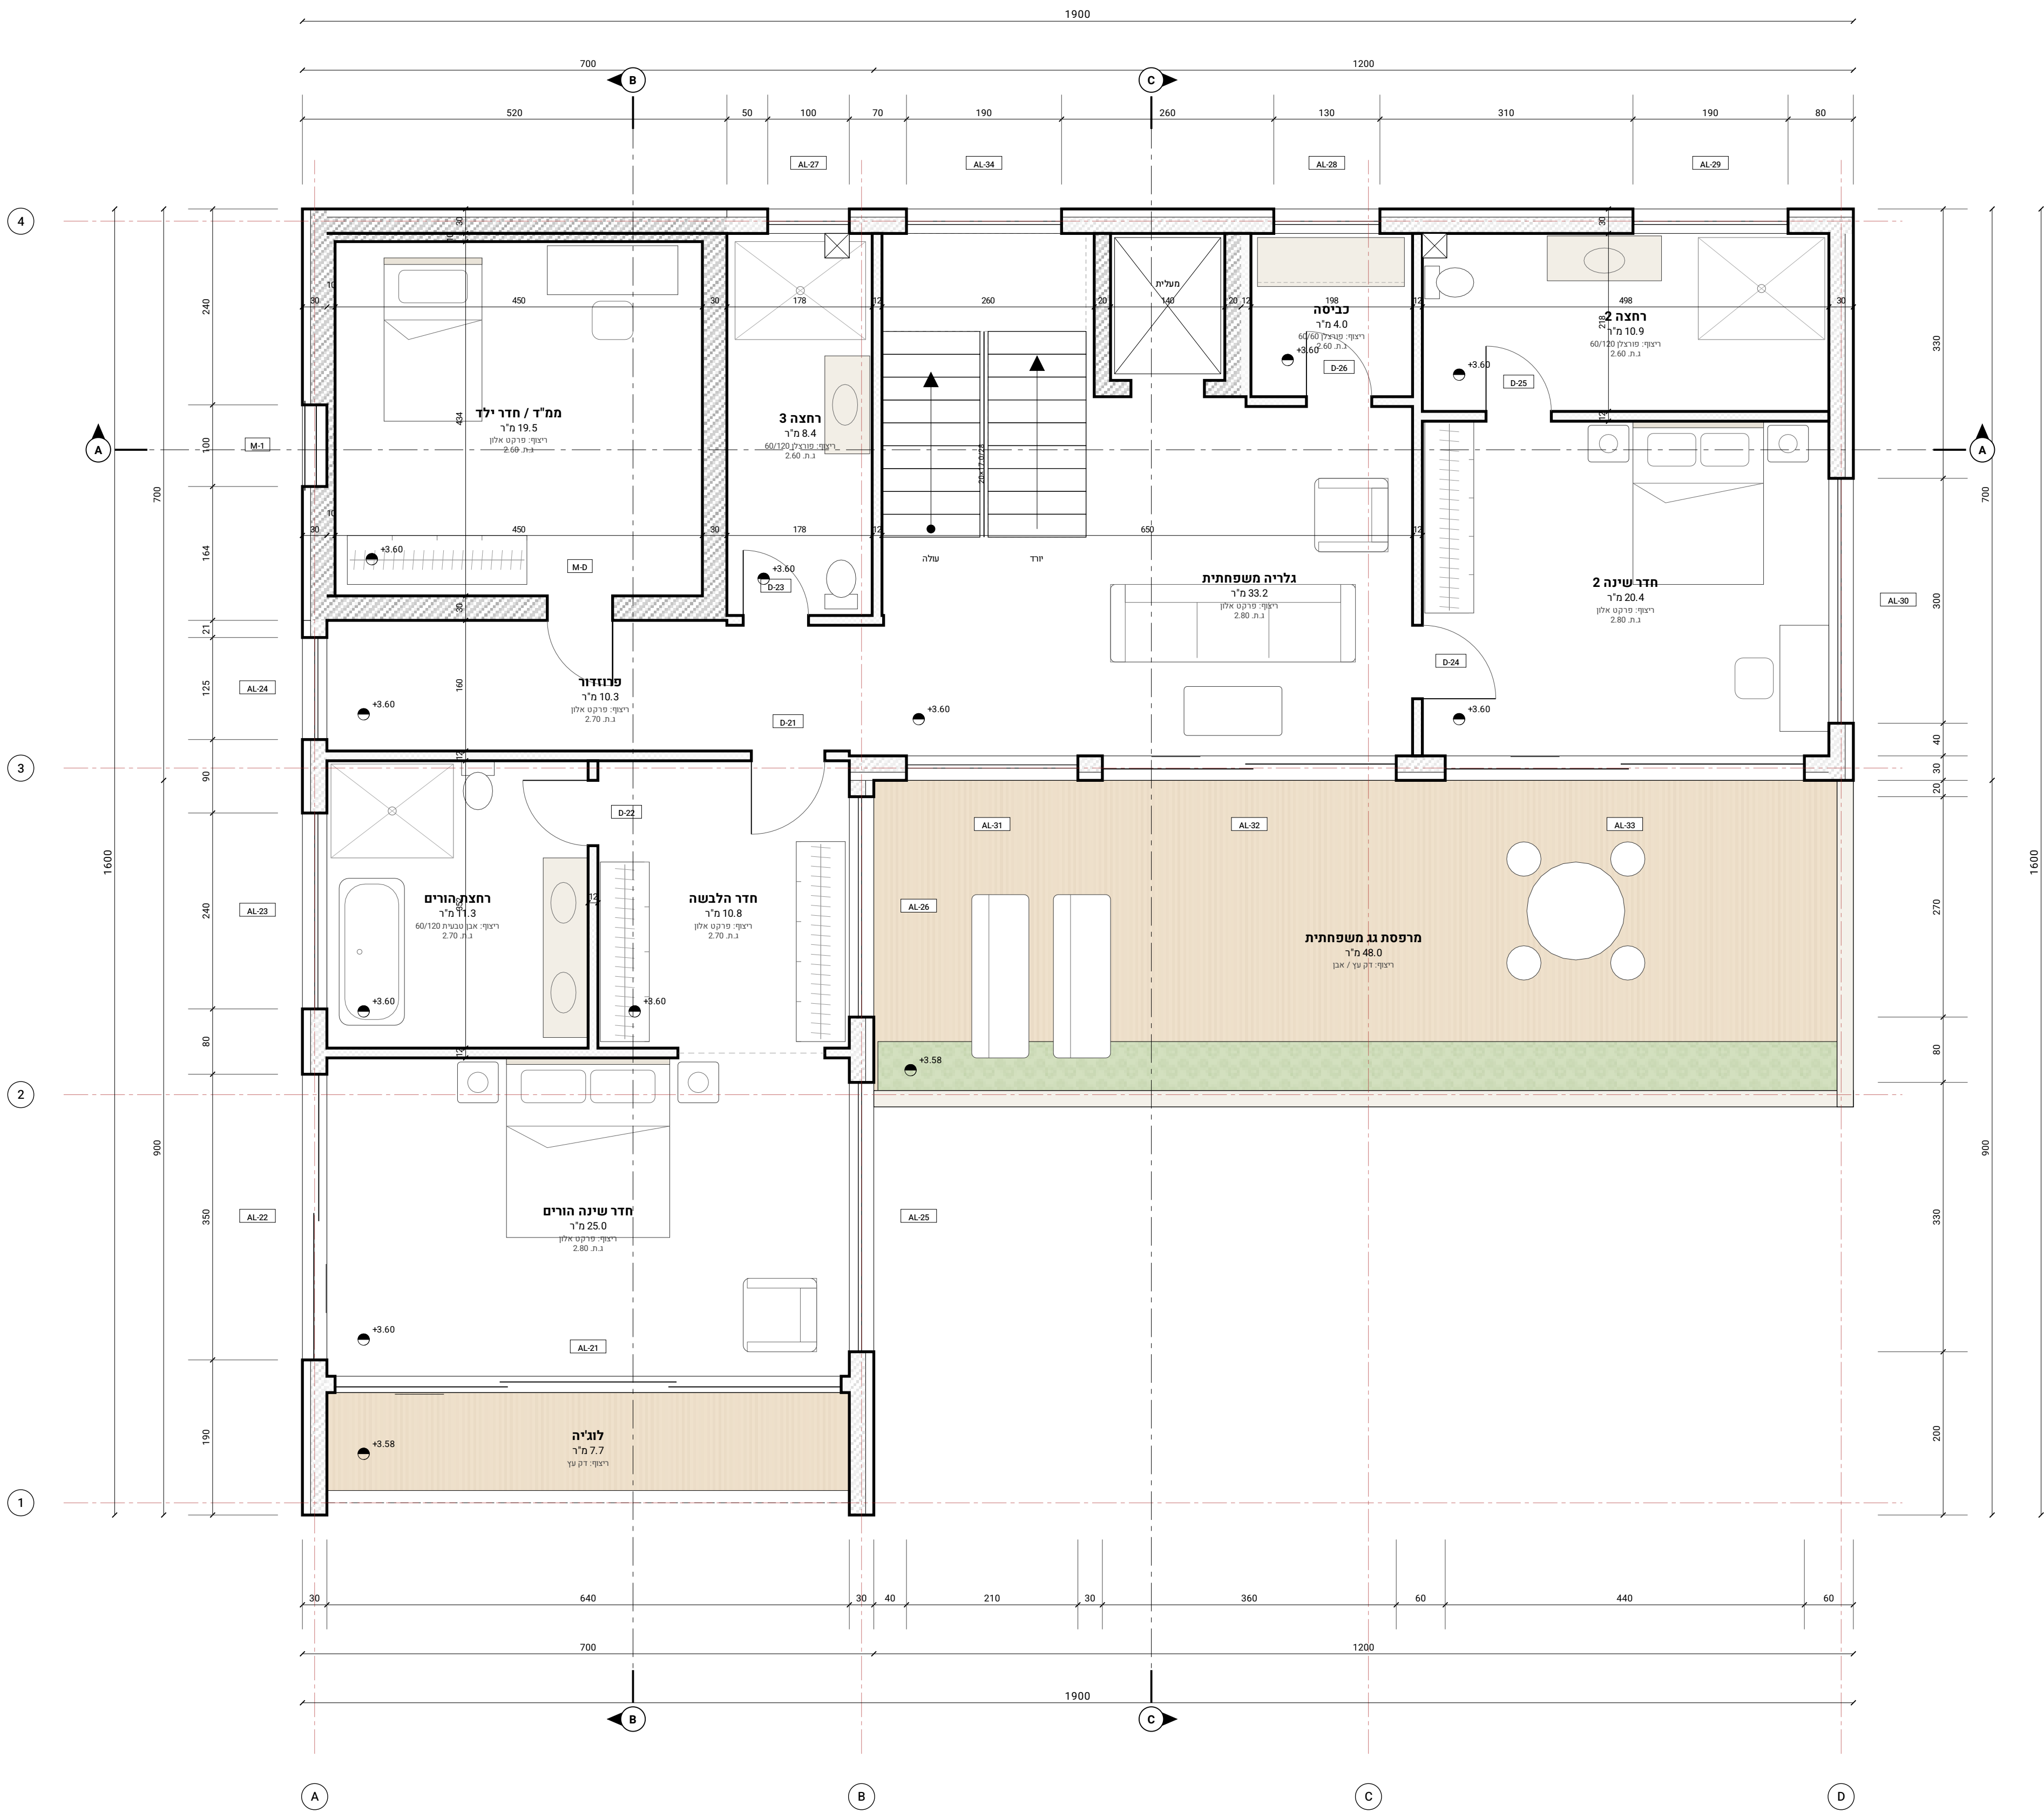

0 1 2 3 4 5 מ'