

בית כורכר

BEIT KURKAR

שם הפרויקט:

מיקום הפרויקט:

קיסריה, רובע 13 (מגרש לימודי)

מנהל:

שרית שריקי

שם הבניין:

גיליון מדרגות

חסי גיליון:

16

שער:

01

קונסט ומוחקר:

02

ניחוח אור וסביבה:

03

תכנית העבודה וכלכל שטחים:

04

תכנית פיתוח שטח:

05

תכנית פרק קרקע:

06

תכנית קומה א ונג:

07

חיתות:

08

חיתות:

09

סככות מטיטות:

10

תכנית קומת קרקע:

11

תכנית קומה א:

12

חיתות:

13

חית A-A:

14

חית B-B:

15

גיליון מדרגות:

16

סרי גיין:

17

רשימת אלומיניום וגרות:

18

ציבוב קנים - חלל המעשים:

19

ציבוב ריבוי - אי המטבח:

20

רשימת חוץ:

21

רשימת פנים:

22

חודה:

23



מנהל:

אדריכלות ועיצוב פנים

שם המיטע/ת.ת.:


תאריך:

10.2026

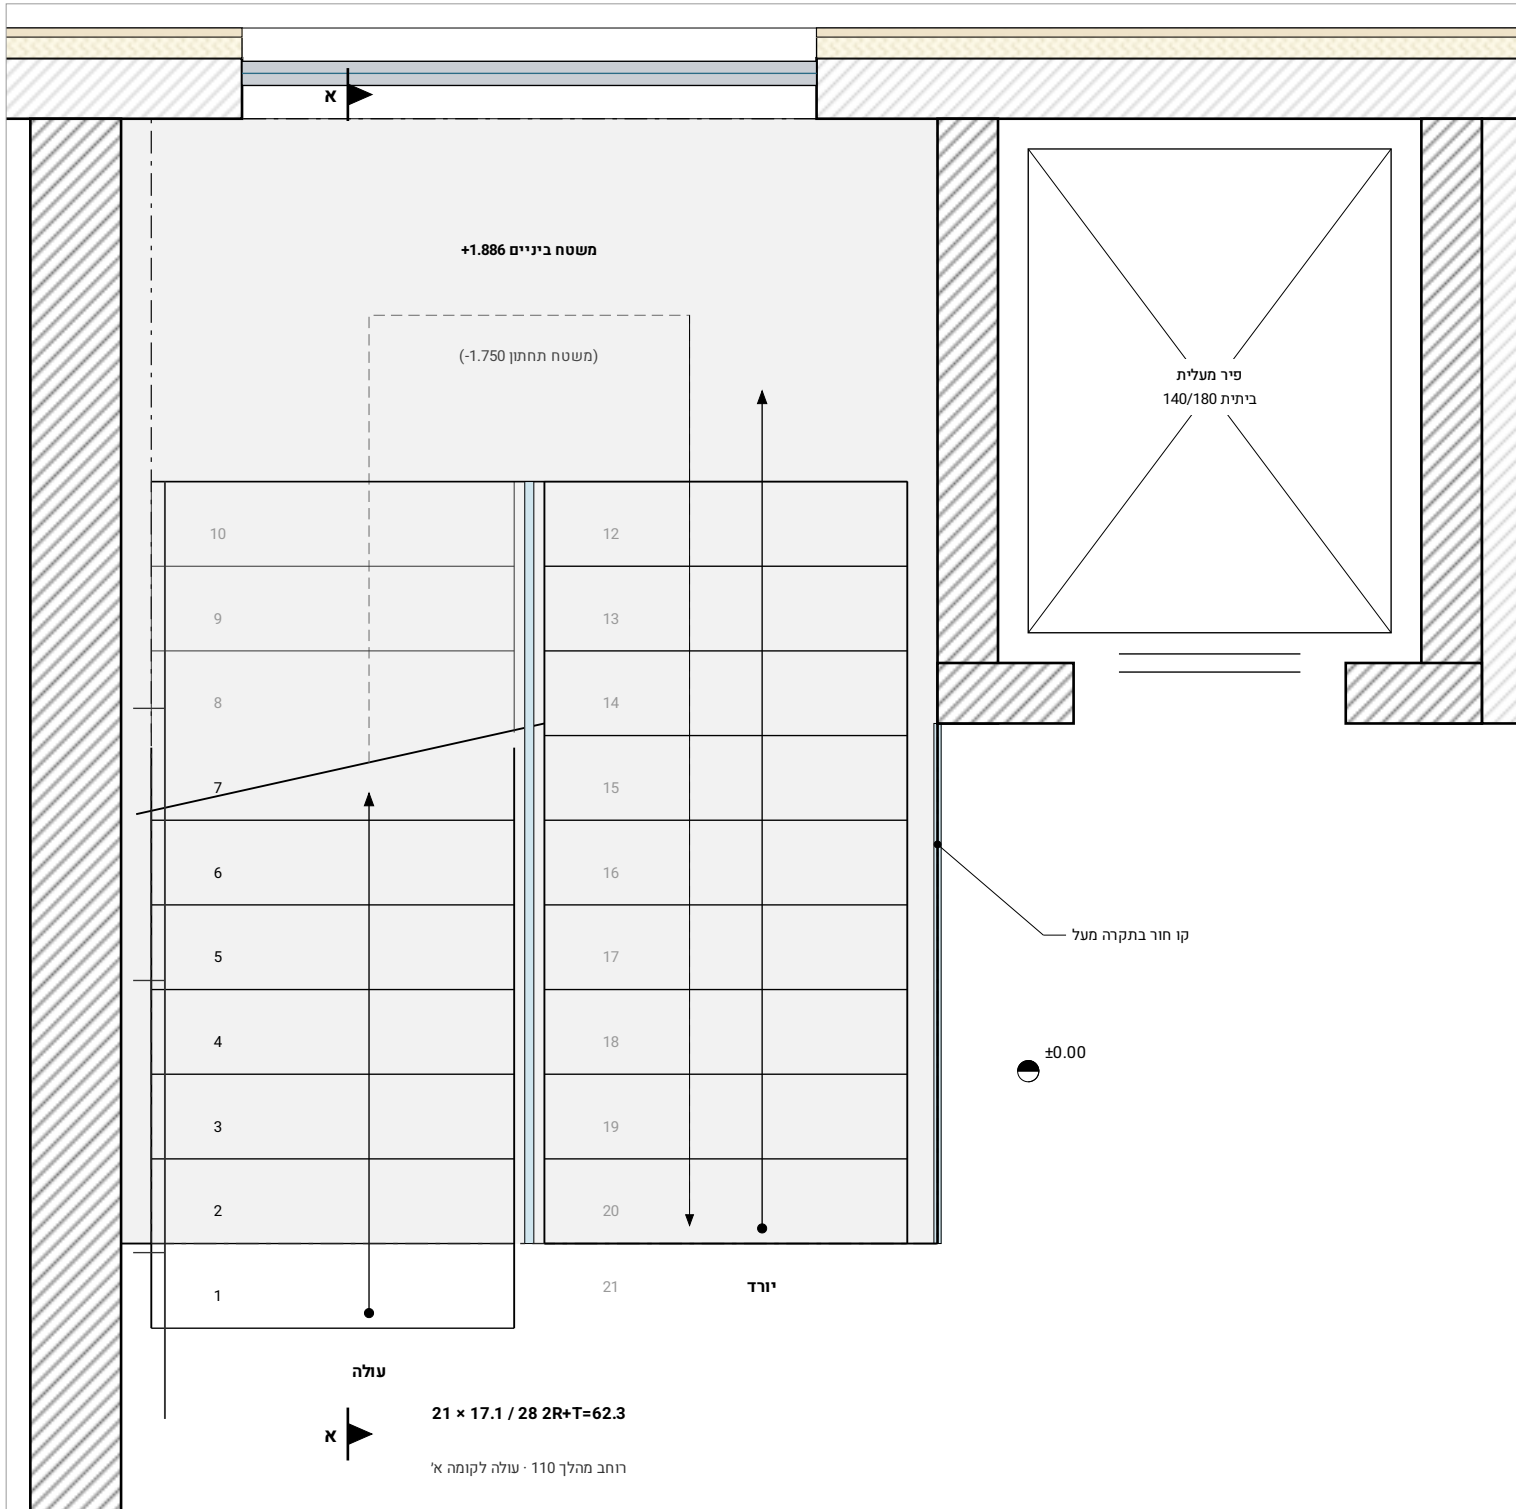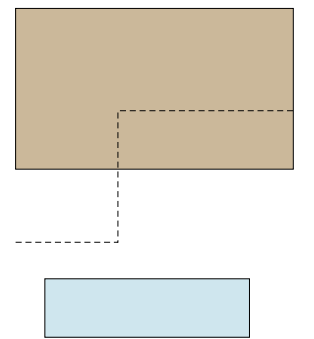


תכנית מדרגות - קומת קרקע

ק"מ 1:25

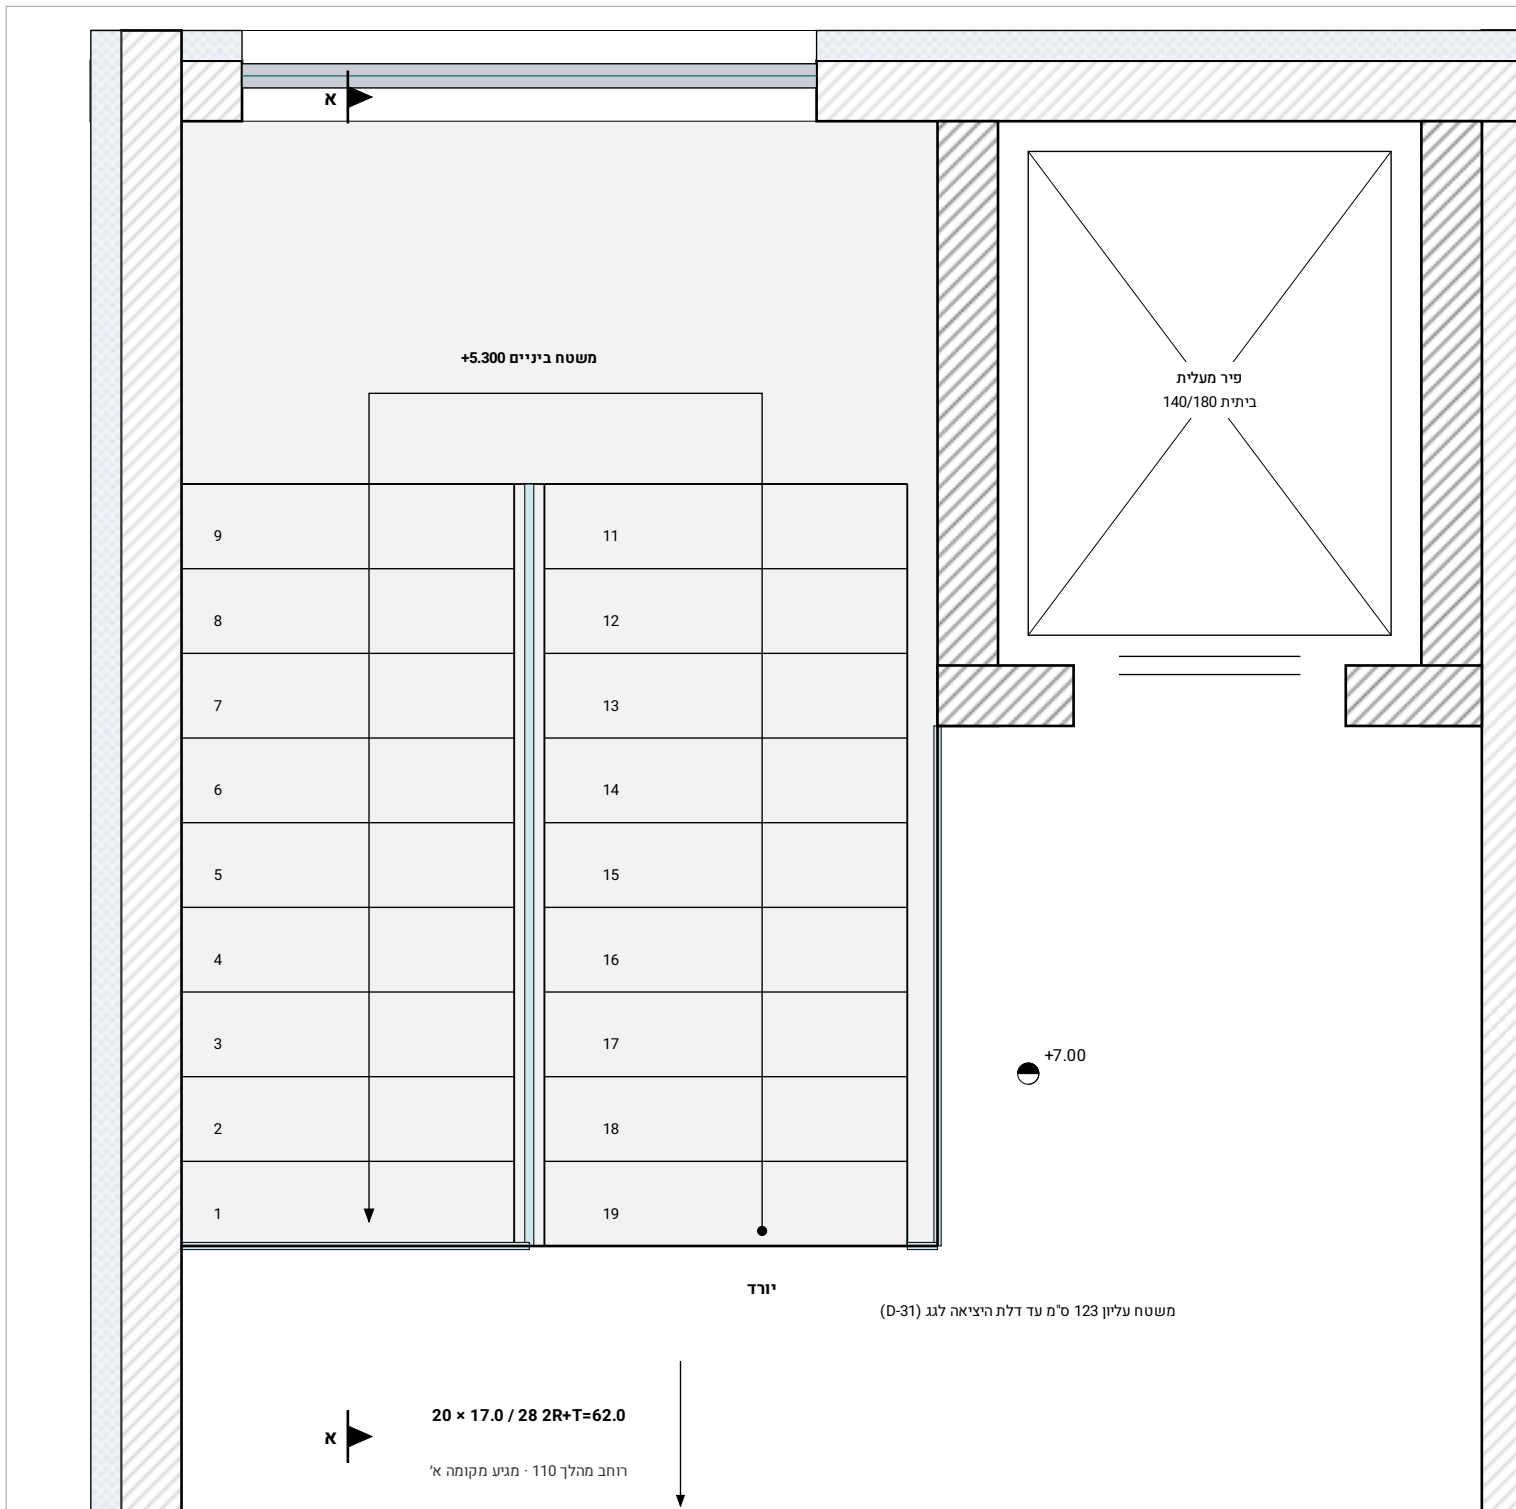


תכנית מדרגות - יציאה לגג

ק"מ 1:25

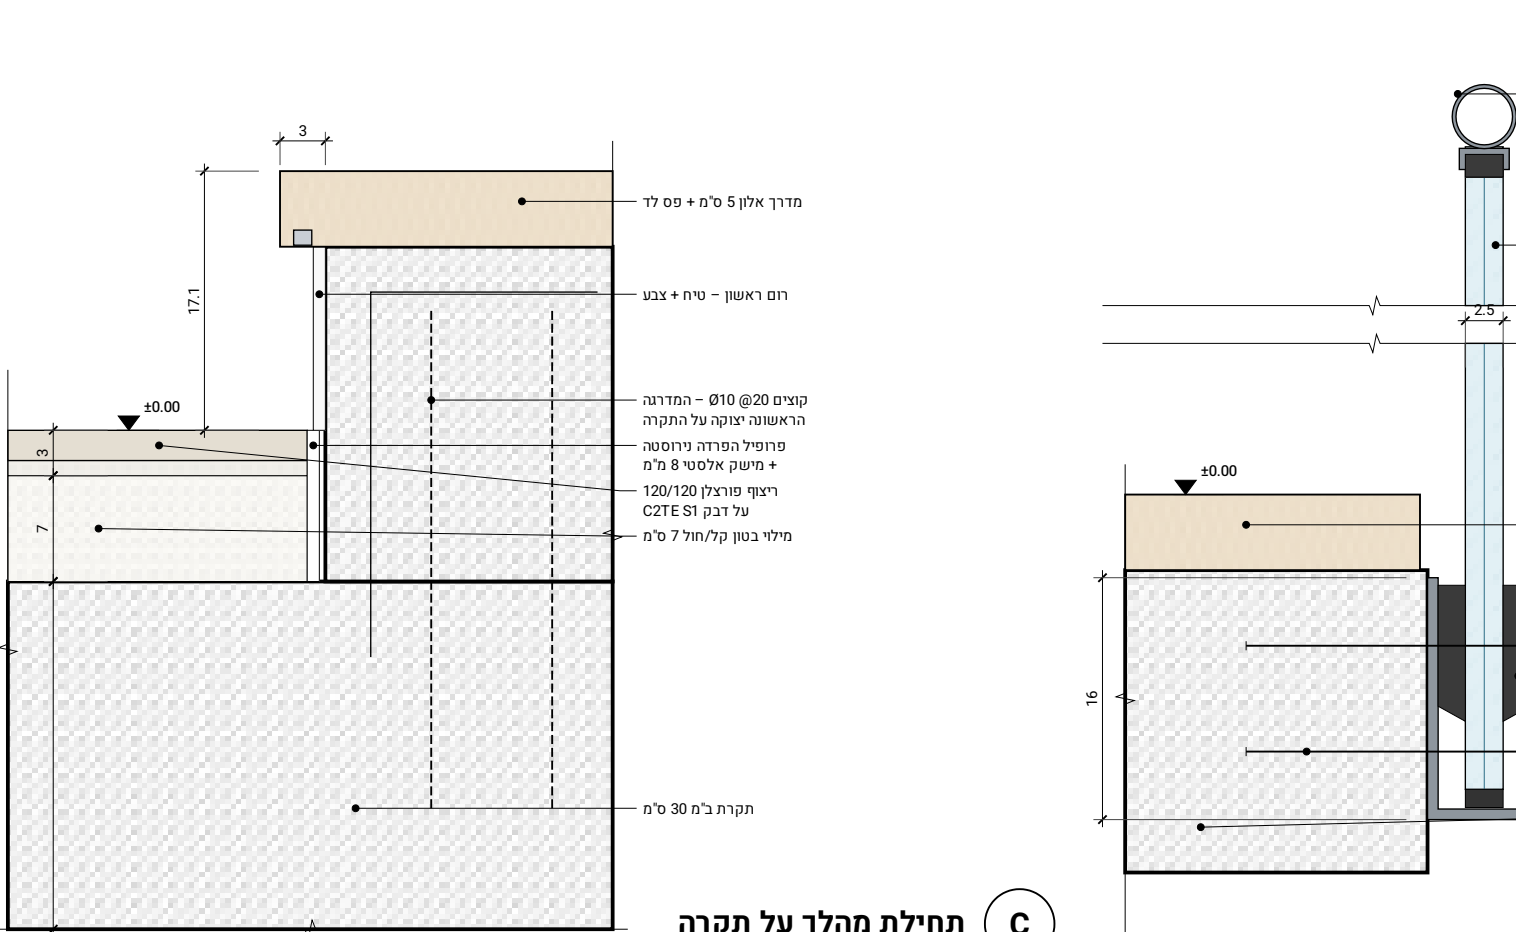


תחילת מהלך על תקרה

ק"מ 1:5

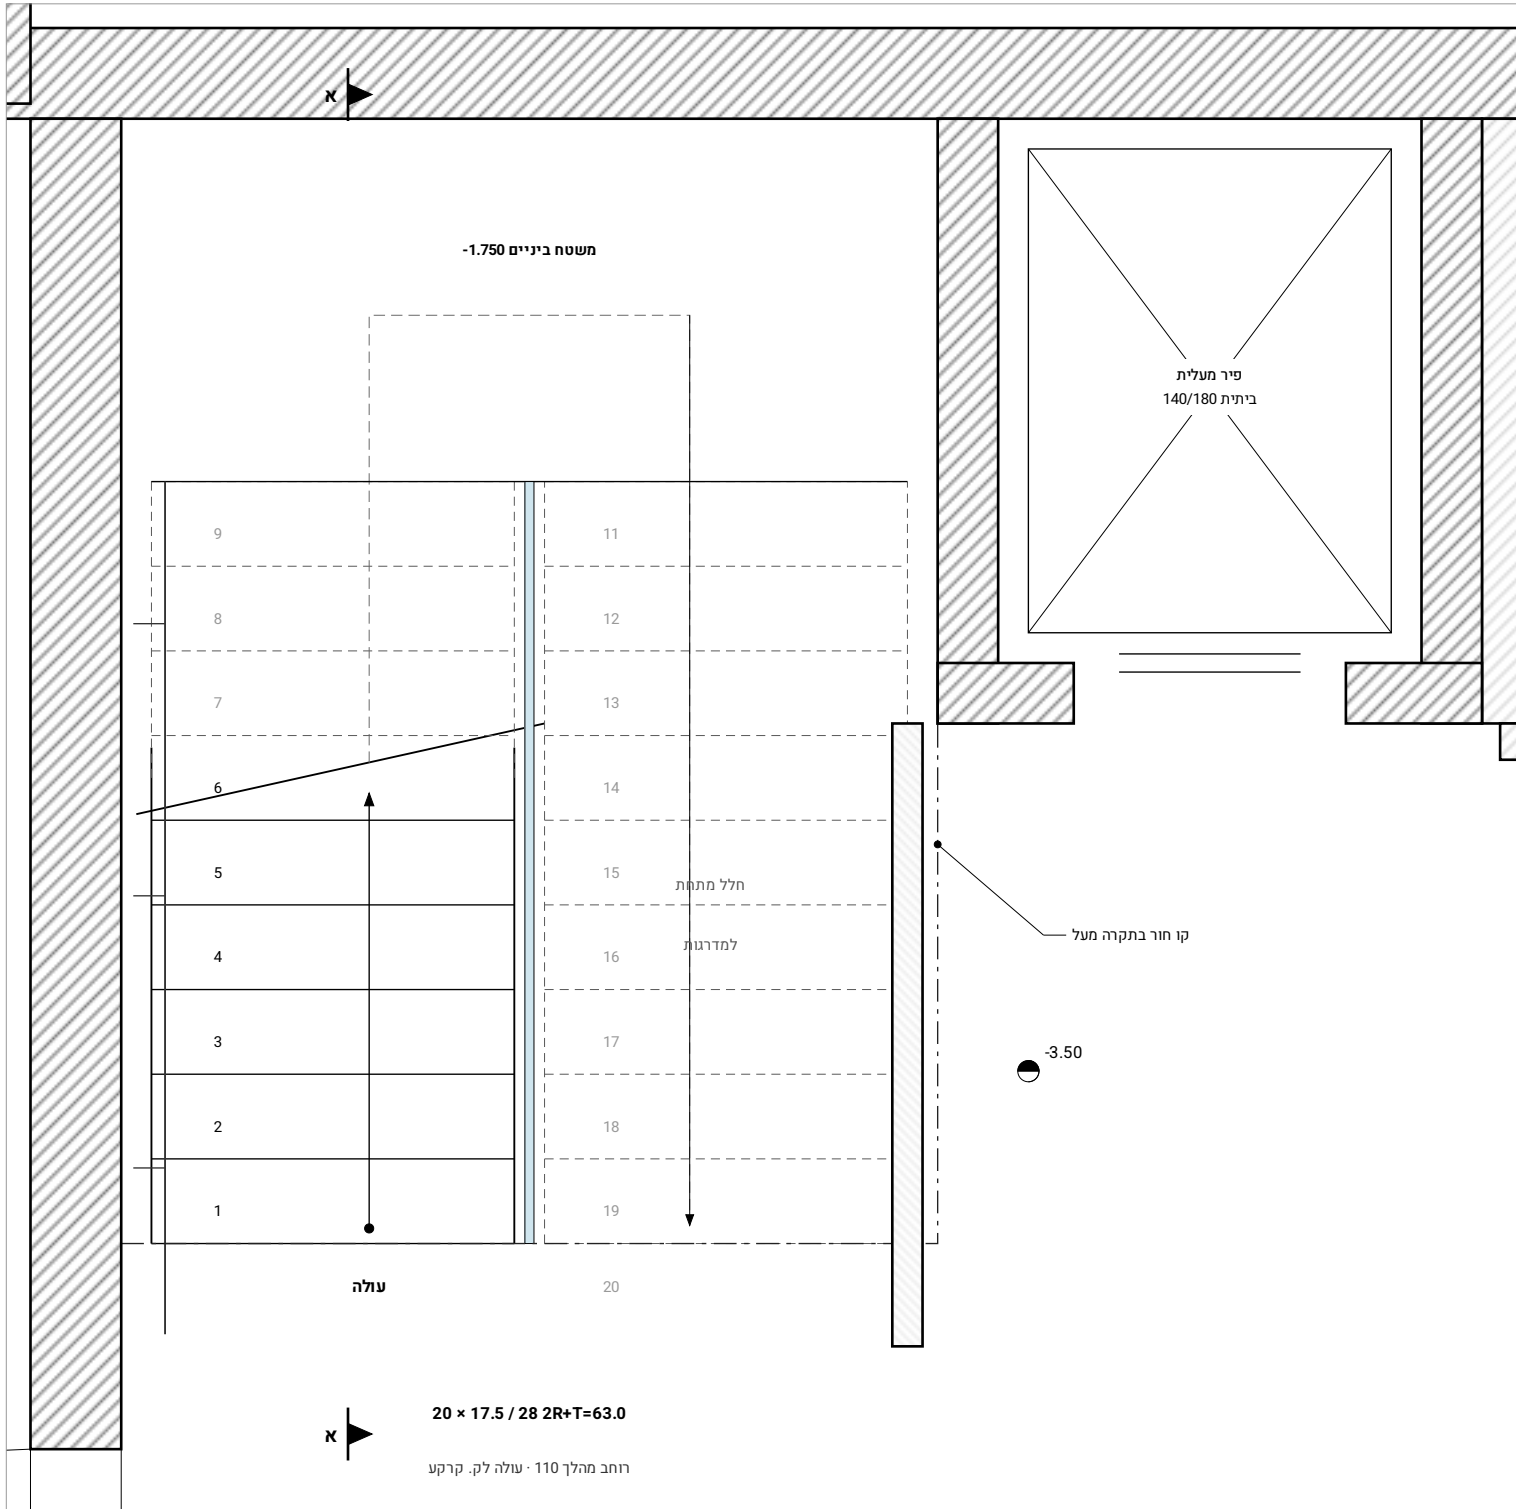


תכנית מדרגות - קומת מרתף

ק"מ 1:25

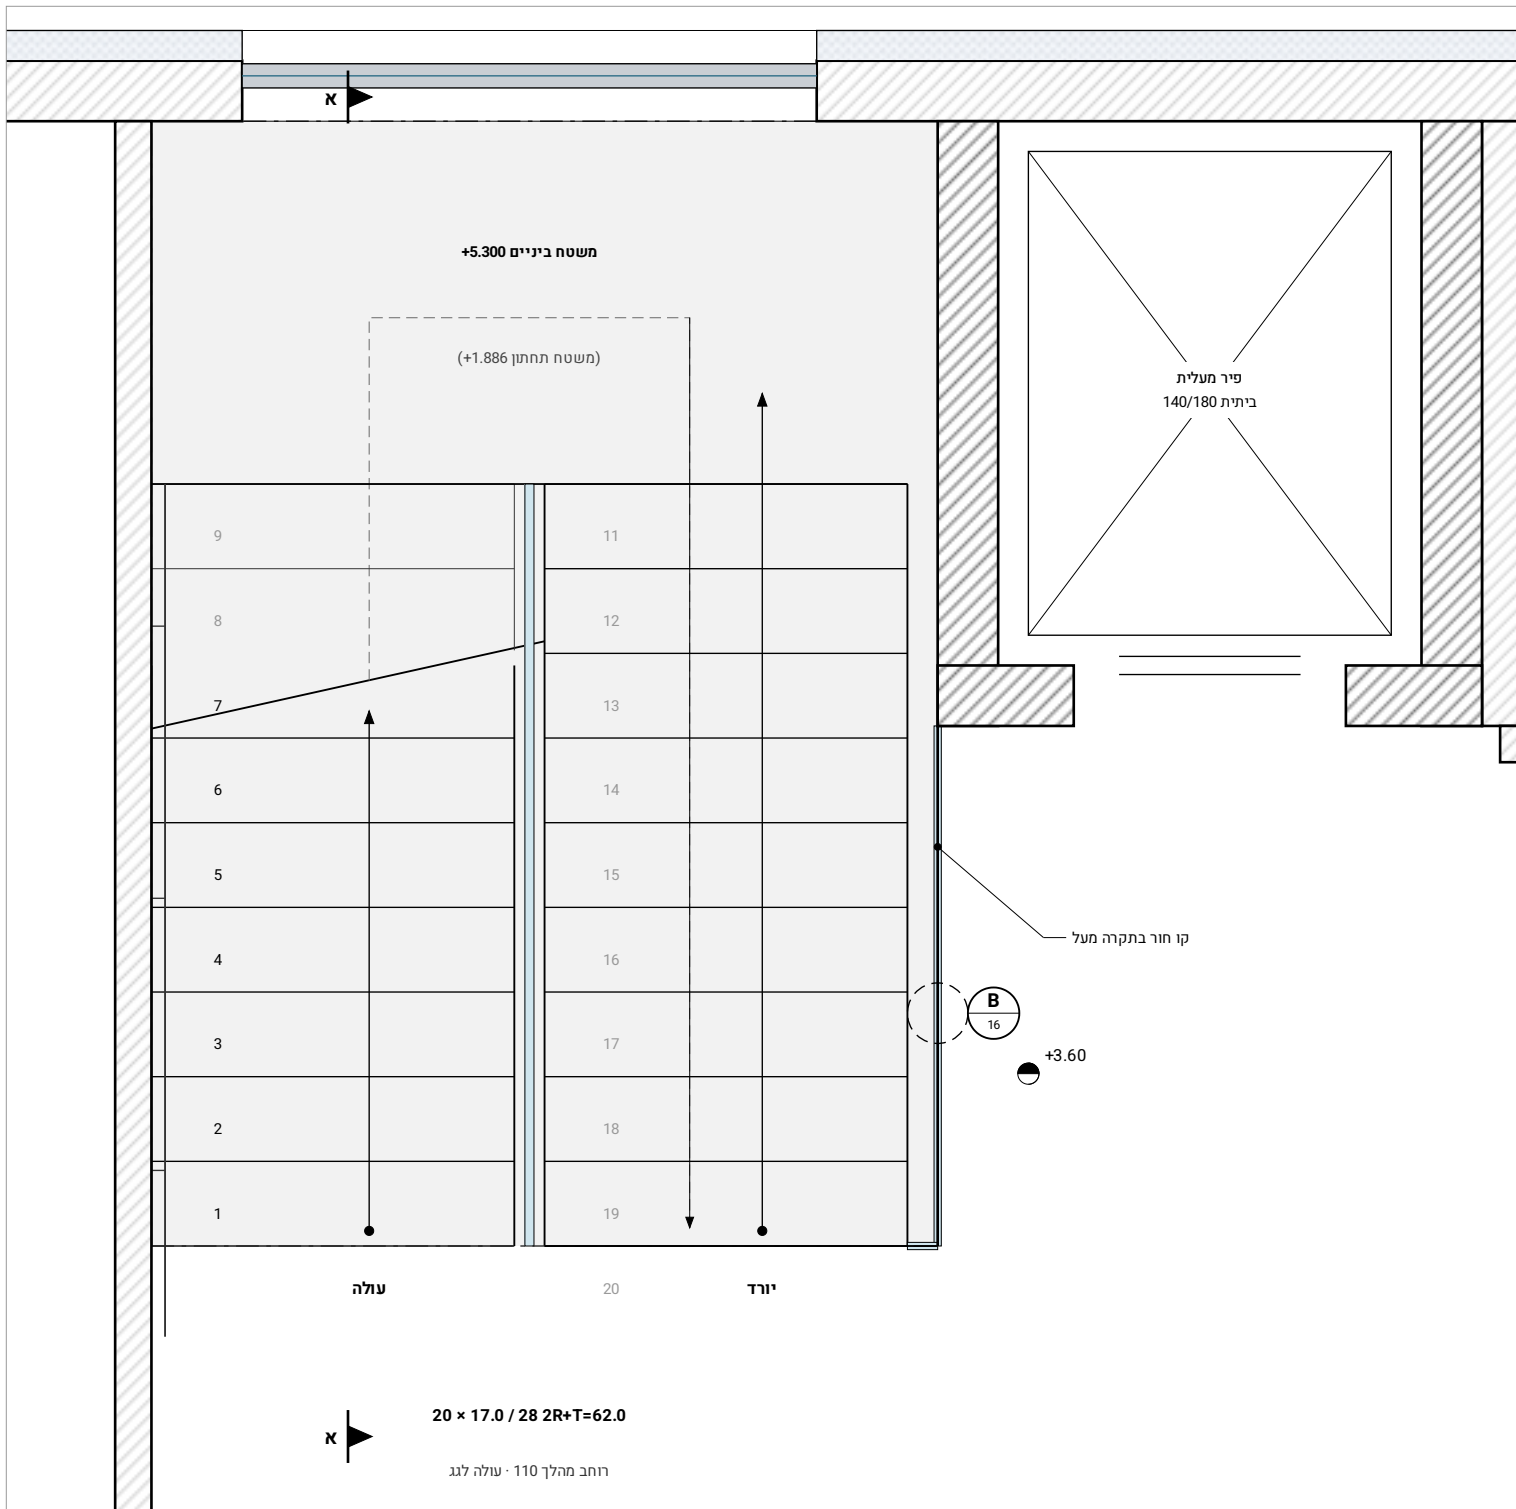


תכנית מדרגות - קומה א

ק"מ 1:25

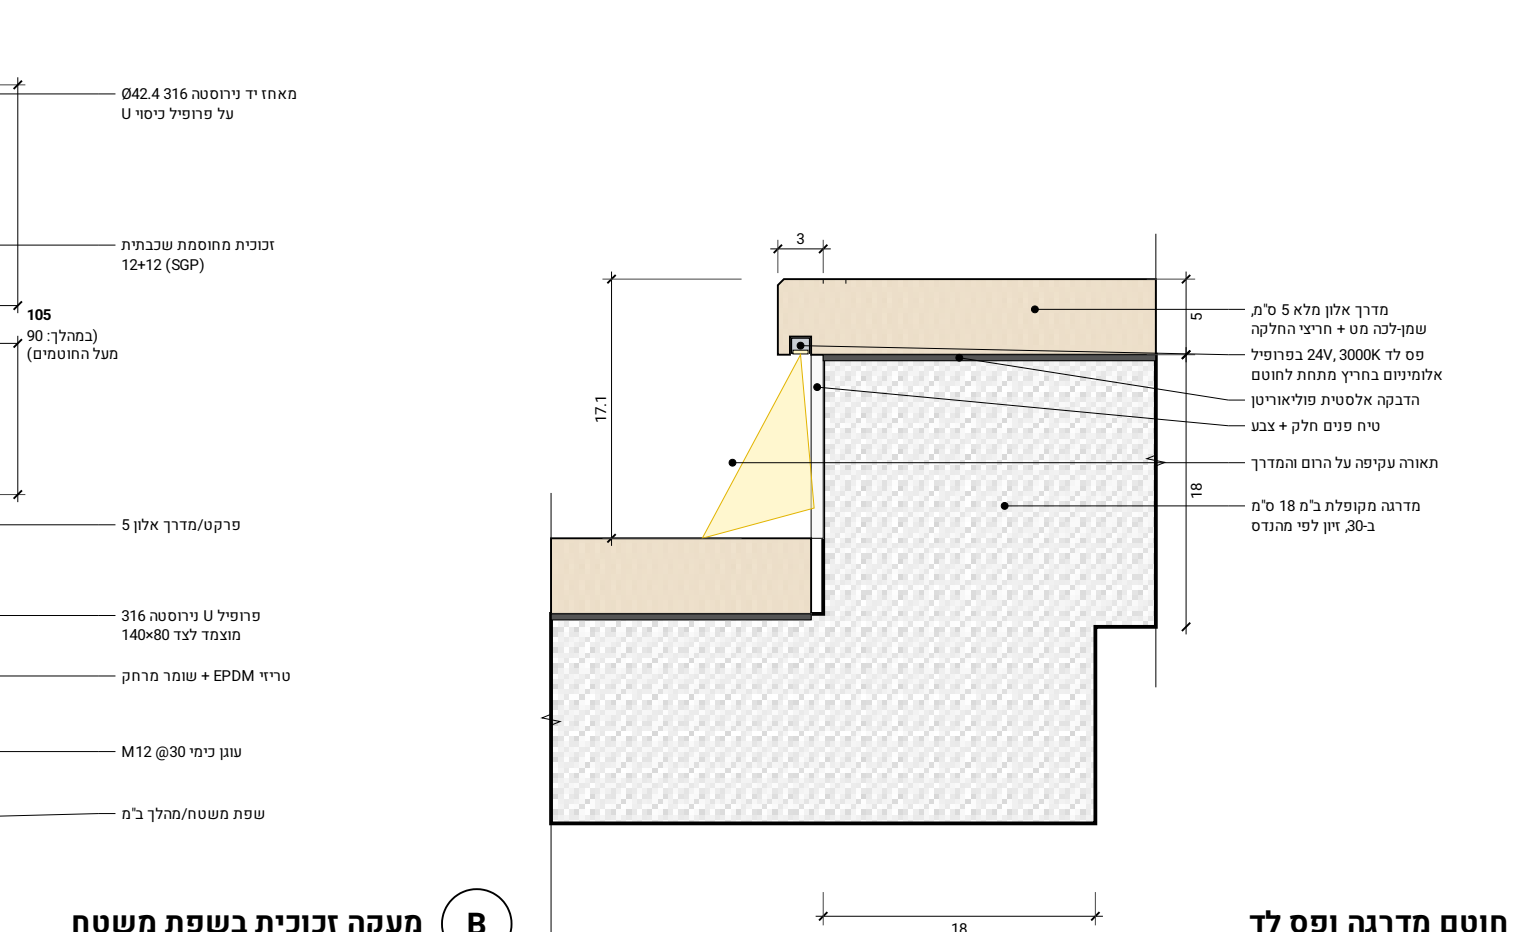

חוטם מדרגה ופס לד

ק"מ 1:5

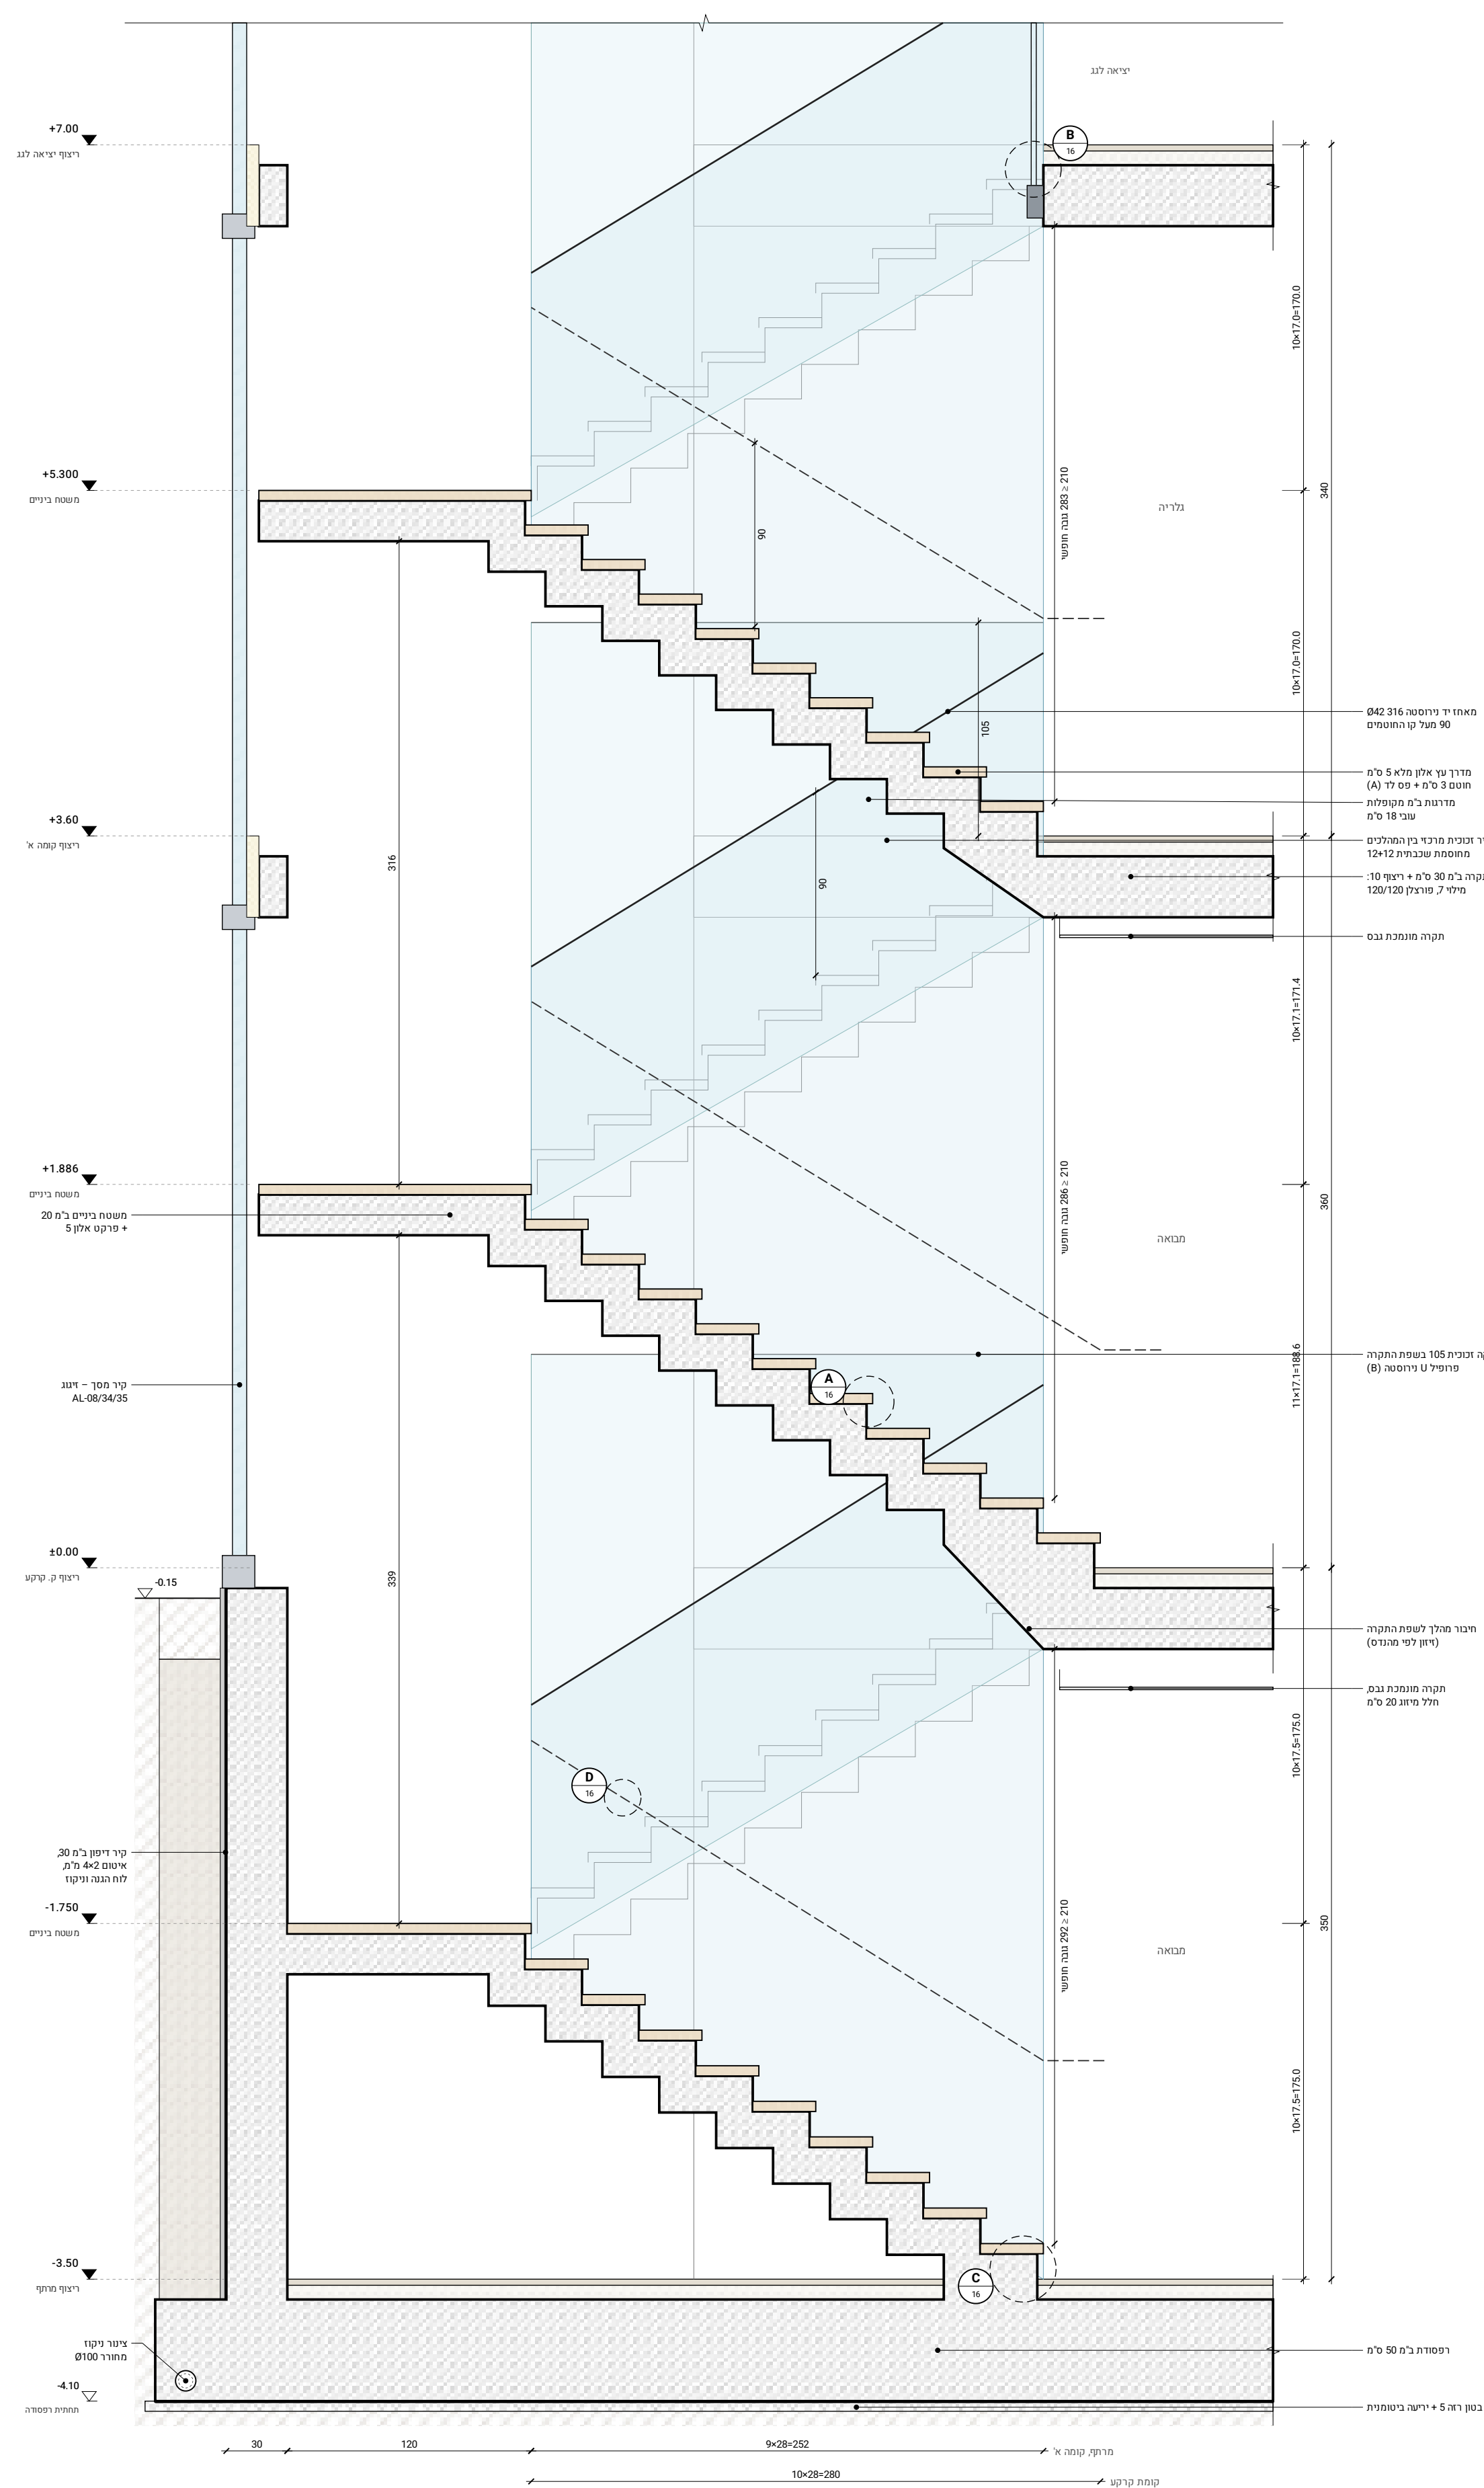

חית A-A - מדרגות

ק"מ 1:25



תושבת מאחז יד

ק"מ 1:5