רשימת אלומיניום

חזיתות מבט מבחוץ · קנ"מ 1:60 · 30 פריטים · 31 יח'

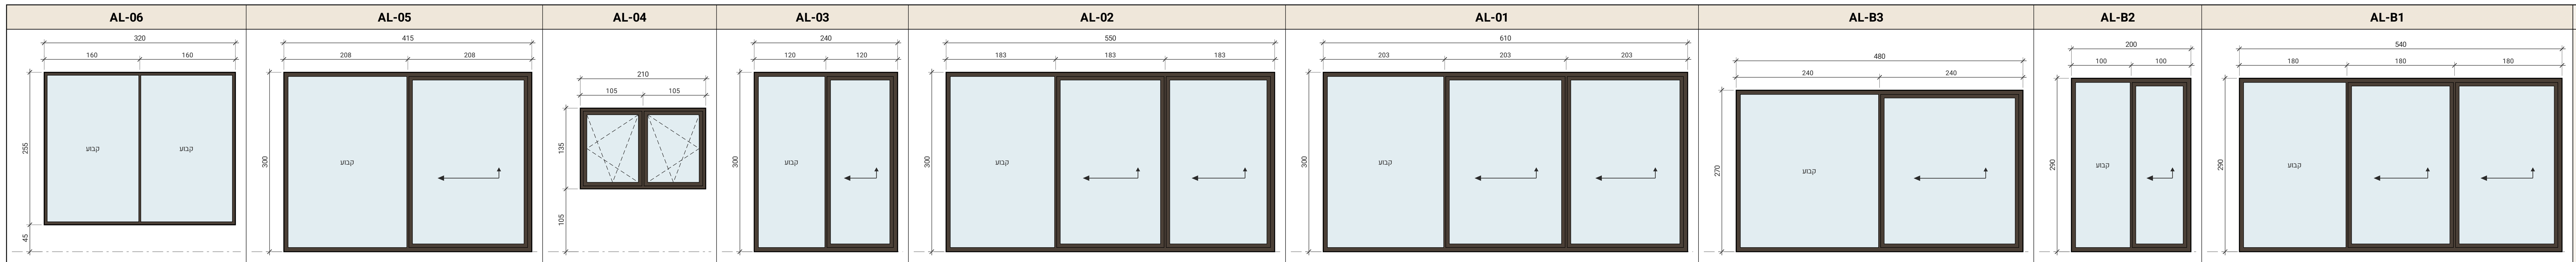

סימון	AL-B1	AL-B2	AL-B3	AL-01	AL-02	AL-03	AL-04	AL-05	AL-06
חזית מבחוץ 1:60									
סוג	דלת הרמה-הזזה תרמית, 3 כנפיים (1 קבועה)	דלת הרמה-הזזה תרמית, 2 כנפיים (1 קבועה)	דלת הרמה-הזזה תרמית, 2 כנפיים (1 קבועה)	דלת הרמה-הזזה תרמית, 3 כנפיים (1 קבועה)	דלת הרמה-הזזה תרמית, 3 כנפיים (1 קבועה)	דלת הרמה-הזזה תרמית, 2 כנפיים (1 קבועה)	חלון ציר-נטוי, 2 כנפיים	דלת הרמה-הזזה תרמית, 2 כנפיים (1 קבועה)	חלון קבוע (ויטרינה)
מערכת / גמר	פרופיל הרמה-הזזה תרמי דוגמת סדרה כבדה "160", מסילה שקועה · ברונזה כהה, מפרט ימי	פרופיל הרמה-הזזה תרמי דוגמת סדרה כבדה "160", מסילה שקועה · ברונזה כהה, מפרט ימי	פרופיל הרמה-הזזה תרמי דוגמת סדרה כבדה "160", מסילה שקועה · ברונזה כהה, מפרט ימי	פרופיל הרמה-הזזה תרמי דוגמת סדרה כבדה "160", מסילה שקועה · ברונזה כהה, מפרט ימי	פרופיל הרמה-הזזה תרמי דוגמת סדרה כבדה "160", מסילה שקועה · ברונזה כהה, מפרט ימי	פרופיל הרמה-הזזה תרמי דוגמת סדרה כבדה "160", מסילה שקועה · ברונזה כהה, מפרט ימי	פרופיל ציר-נטוי תרמי דוגמת סדרה "70", 3 אטמים · ברונזה כהה, מפרט ימי	פרופיל הרמה-הזזה תרמי דוגמת סדרה כבדה "160", מסילה שקועה · ברונזה כהה, מפרט ימי	פרופיל ויטרינה / מסך תרמי דוגמת סדרה "50", גליף נסתר · ברונזה כהה, מפרט ימי
זיגוג	בידודי 8+16A+55.2 Low-E · חוץ מחוסם, פנים שכבתי	בידודי 6+16A+44.2 Low-E · חוץ מחוסם, פנים שכבתי	בידודי 8+16A+55.2 Low-E · חוץ מחוסם, פנים שכבתי	בידודי 8+16A+55.2 Low-E · חוץ מחוסם, פנים שכבתי	בידודי 8+16A+55.2 Low-E · חוץ מחוסם, פנים שכבתי	בידודי 8+16A+55.2 Low-E · חוץ מחוסם, פנים שכבתי	בידודי 6+16A+44.2 Low-E · חוץ שקוף, פנים שכבתי	בידודי 8+16A+55.2 Low-E · חוץ מחוסם, פנים שכבתי	בידודי 8+16A+55.2 Low-E · חוץ מחוסם, פנים שכבתי
הצללה	תריס גלילה חשמלי נסתר, שלבי אלומיניום מוקצף	תריס גלילה חשמלי נסתר, שלבי אלומיניום מוקצף	תריס גלילה חשמלי נסתר, שלבי אלומיניום מוקצף	תריס גלילה חשמלי נסתר, שלבי אלומיניום מוקצף	תריס גלילה חשמלי נסתר, שלבי אלומיניום מוקצף	תריס גלילה חשמלי נסתר, שלבי אלומיניום מוקצף	תריס גלילה חשמלי נסתר, שלבי אלומיניום מוקצף	תריס גלילה חשמלי נסתר, שלבי אלומיניום מוקצף	וילון סקרין פנימי חשמלי
מידות ר/ג · אדן	540/290 · אדן ±0	200/290 · אדן ±0	480/270 · אדן ±0	610/300 · אדן ±0	550/300 · אדן ±0	240/300 · אדן ±0	210/135 · אדן +105	415/300 · אדן ±0	320/255 · אדן +45
כמות · קומה	1 יח' · מרתף	1 יח' · מרתף	1 יח' · מרתף	1 יח' · קרקע	1 יח' · קרקע	1 יח' · קרקע	1 יח' · קרקע	1 יח' · קרקע	1 יח' · קרקע
מיקום · חזית	טרקלין ובר · דרום	חדר אורחים · דרום	חדר כושר / יוגה · צפון	סלון · דרום	פינת אוכל · דרום	מטבח · דרום	מטבח · דרום	סלון · מערב	סלון · מערב
הערות	סף נגיש שקוע ברצפה, מנעול רב-נקודתי	סף נגיש שקוע ברצפה, מנעול רב-נקודתי	סף נגיש שקוע ברצפה, מנעול רב-נקודתי	סף נגיש שקוע ברצפה, מנעול רב-נקודתי	סף נגיש שקוע ברצפה, מנעול רב-נקודתי	סף נגיש שקוע ברצפה, מנעול רב-נקודתי	–	סף נגיש שקוע ברצפה, מנעול רב-נקודתי	–

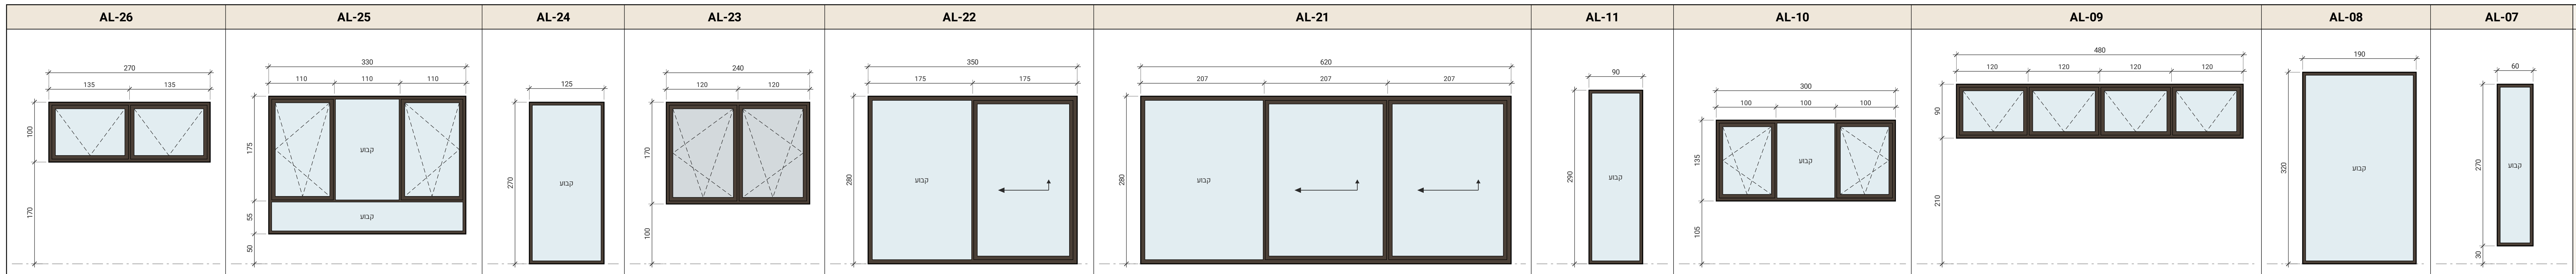

סימון	AL-07	AL-08	AL-09	AL-10	AL-11	AL-21	AL-22	AL-23	AL-24	AL-25	AL-26
חזית מבחוץ 1:60											
סוג	חריץ זיגוג קבוע	ויטרינה קבועה רציפה (קיר מסך)	חלון נטוי (קיפ) חשמלי, 4 כנפיים	חלון ציר-נטוי, 2 כנפיים + 1 קבוע	חלון קבוע (ויטרינה)	דלת הרמה-הזזה תרמית, 3 כנפיים (1 קבועה)	דלת הרמה-הזזה תרמית, 2 כנפיים (1 קבועה)	חלון ציר-נטוי, 2 כנפיים	חלון קבוע (ויטרינה)	חלון ציר-נטוי, 2 כנפיים + 1 קבוע	חלון נטוי (קיפ) חשמלי, 2 כנפיים
מערכת / גמר	פרופיל ויטרינה / מסך תרמי דוגמת סדרה "50", גליף נסתר · ברונזה כהה, מפרט ימי	פרופיל ויטרינה / מסך תרמי דוגמת סדרה "50", גליף נסתר · ברונזה כהה, מפרט ימי	פרופיל ציר-נטוי תרמי דוגמת סדרה "70", 3 אטמים · ברונזה כהה, מפרט ימי	פרופיל ציר-נטוי תרמי דוגמת סדרה "70", 3 אטמים · ברונזה כהה, מפרט ימי	פרופיל ויטרינה / מסך תרמי דוגמת סדרה "50", גליף נסתר · ברונזה כהה, מפרט ימי	פרופיל הרמה-הזזה תרמי דוגמת סדרה כבדה "160", מסילה שקועה · ברונזה כהה, מפרט ימי	פרופיל הרמה-הזזה תרמי דוגמת סדרה כבדה "160", מסילה שקועה · ברונזה כהה, מפרט ימי	פרופיל ציר-נטוי תרמי דוגמת סדרה "70", 3 אטמים · ברונזה כהה, מפרט ימי	פרופיל ויטרינה / מסך תרמי דוגמת סדרה "50", גליף נסתר · ברונזה כהה, מפרט ימי	פרופיל ציר-נטוי תרמי דוגמת סדרה "70", 3 אטמים · ברונזה כהה, מפרט ימי	פרופיל ציר-נטוי תרמי דוגמת סדרה "70", 3 אטמים · ברונזה כהה, מפרט ימי
זיגוג	בידודי 6+16A+44.2 Low-E · חוץ מחוסם, פנים שכבתי	בידודי 8+16A+55.2 Low-E · חוץ מחוסם, פנים שכבתי	בידודי 6+16A+44.2 Low-E · חוץ שקוף, פנים שכבתי	בידודי 6+16A+44.2 Low-E · חוץ שקוף, פנים שכבתי	בידודי 6+16A+44.2 Low-E · חוץ מחוסם, פנים שכבתי	בידודי 8+16A+55.2 Low-E · חוץ מחוסם, פנים שכבתי	בידודי 8+16A+55.2 Low-E · חוץ מחוסם, פנים שכבתי	בידודי 6+16A+44.2 Low-E · חוץ מחוסם, פנים שכבתי חלבי (סאטן)	בידודי 6+16A+44.2 Low-E · חוץ מחוסם, פנים שכבתי	בידודי 6+16A+44.2 Low-E · חוץ מחוסם, פנים שכבתי	בידודי 6+16A+44.2 Low-E · חוץ שקוף, פנים שכבתי
הצללה	–	–	– (חזית צפון)	תריס גלילה חשמלי נסתר, שלבי אלומיניום מוקצף	–	תריס גלילה חשמלי נסתר, שלבי אלומיניום מוקצף	רפפות אנכיות קבועות דמוי עץ 50/200 @180 + תריס חשמלי נסתר	רפפות אנכיות קבועות דמוי עץ 50/200 @180	וילון סקרין פנימי חשמלי	תריס גלילה חשמלי נסתר, שלבי אלומיניום מוקצף	תריס גלילה חשמלי נסתר, שלבי אלומיניום מוקצף
מידות ר/ג · אדן	60/270 · אדן +30	190/320 · אדן ±0	480/90 · אדן +210	300/135 · אדן +105	90/290 · אדן ±0	620/280 · אדן ±0	350/280 · אדן ±0	240/170 · אדן +100	125/270 · אדן ±0	330/230 · אדן +50	270/100 · אדן +170
כמות · קומה	2 יח' · קרקע	1 יח' · קרקע	1 יח' · קרקע	1 יח' · קרקע	1 יח' · קרקע	1 יח' · א'	1 יח' · א'	1 יח' · א'	1 יח' · א'	1 יח' · א'	1 יח' · א'
מיקום · חזית	סלון · צפון	מבואה ומדרגות · צפון	לובי כניסה · צפון	מטבח · מזרח	לובי כניסה · מזרח	חדר שינה הורים · דרום	חדר שינה הורים · מערב	רחצת הורים · מערב	פרוזדור · מערב	חדר שינה הורים · מזרח	חדר הלבשה · מזרח
הערות	2 חריצים זהים	זיגוג בטיחותי עד רצפה	מנוע פתיחה + חיישן גשם, אוורור לילה	–	זיגוג בטיחותי עד רצפה · חלון צד לדלת הכניסה D-01	סף נגיש שקוע ברצפה, מנעול רב-נקודתי	סף נגיש שקוע ברצפה, מנעול רב-נקודתי · מאחורי מסך רפפות אנכיות	זכוכית חלבית לפרטיות · מאחורי מסך רפפות אנכיות	זיגוג בטיחותי עד רצפה	מקטע תחתון קבוע שכבתי עד 105 ס"מ (מניעת נפילה)	מנוע פתיחה + חיישן גשם, אוורור לילה

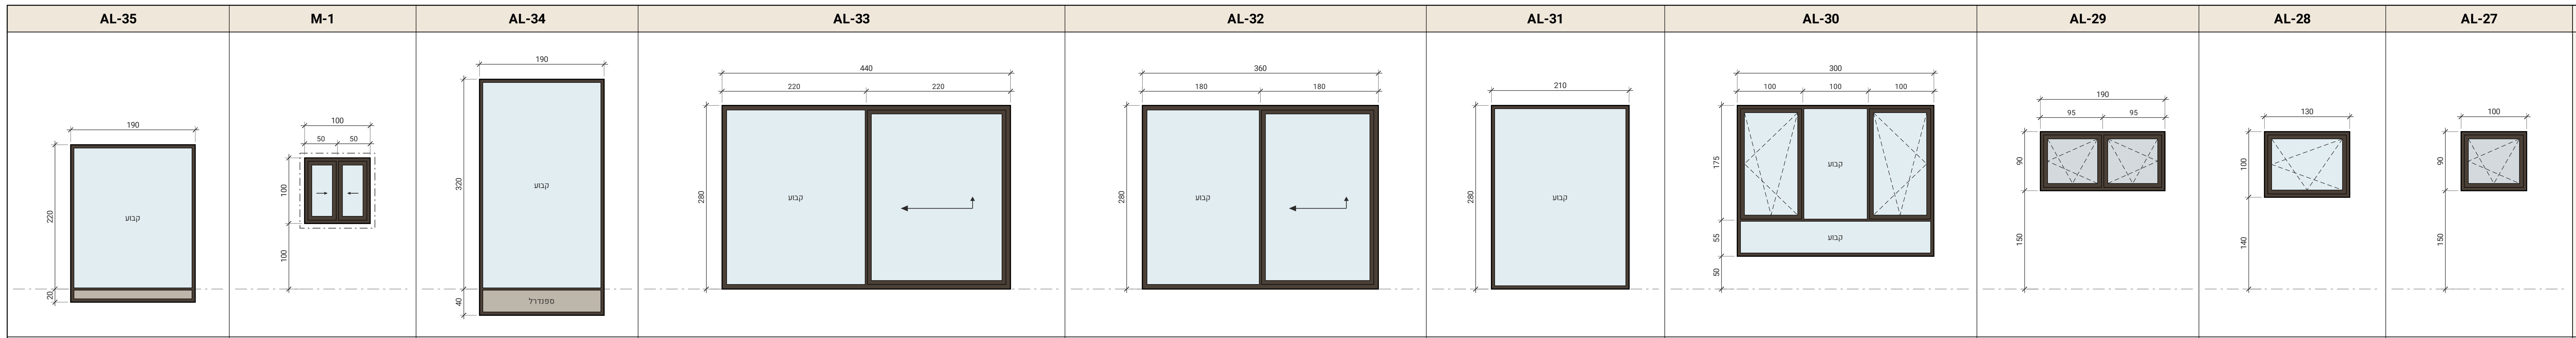

סימון	AL-27	AL-28	AL-29	AL-30	AL-31	AL-32	AL-33	AL-34	M-1	AL-35
חזית מבחוץ 1:60										
סוג	חלון ציר-נטוי, כנף אחת	חלון ציר-נטוי, כנף אחת	חלון ציר-נטוי, 2 כנפיים	חלון ציר-נטוי, 2 כנפיים + 1 קבוע	חלון קבוע (ויטרינה)	דלת הרמה-הזזה תרמית, 2 כנפיים (1 קבועה)	דלת הרמה-הזזה תרמית, 2 כנפיים (1 קבועה)	ויטרינה קבועה רציפה (קיר מסך)	חלון ממ"ד: הזזה + חלון הדף פלדה	ויטרינה קבועה רציפה (קיר מסך)
מערכת / גמר	פרופיל ציר-נטוי תרמי דוגמת סדרה "70", 3 אטמים · ברונזה כהה, מפרט ימי	פרופיל ציר-נטוי תרמי דוגמת סדרה "70", 3 אטמים · ברונזה כהה, מפרט ימי	פרופיל ציר-נטוי תרמי דוגמת סדרה "70", 3 אטמים · ברונזה כהה, מפרט ימי	פרופיל ציר-נטוי תרמי דוגמת סדרה "70", 3 אטמים · ברונזה כהה, מפרט ימי	פרופיל ויטרינה / מסך תרמי דוגמת סדרה "50", גליף נסתר · ברונזה כהה, מפרט ימי	פרופיל הרמה-הזזה תרמי דוגמת סדרה כבדה "160", מסילה שקועה · ברונזה כהה, מפרט ימי	פרופיל הרמה-הזזה תרמי דוגמת סדרה כבדה "160", מסילה שקועה · ברונזה כהה, מפרט ימי	פרופיל ויטרינה / מסך תרמי דוגמת סדרה "50", גליף נסתר · ברונזה כהה, מפרט ימי	פרופיל הזזה תרמי דוגמת סדרה "70" + חלון הדף פלדה מאושר · ברונזה כהה, מפרט ימי	פרופיל ויטרינה / מסך תרמי דוגמת סדרה "50", גליף נסתר · ברונזה כהה, מפרט ימי
זיגוג	בידודי 6+16A+44.2 Low-E · חוץ שקוף, פנים שכבתי חלבי (סאטן)	בידודי 6+16A+44.2 Low-E · חוץ שקוף, פנים שכבתי	בידודי 6+16A+44.2 Low-E · חוץ שקוף, פנים שכבתי חלבי (סאטן)	בידודי 6+16A+44.2 Low-E · חוץ מחוסם, פנים שכבתי	בידודי 8+16A+55.2 Low-E · חוץ מחוסם, פנים שכבתי	בידודי 8+16A+55.2 Low-E · חוץ מחוסם, פנים שכבתי	בידודי 8+16A+55.2 Low-E · חוץ מחוסם, פנים שכבתי	בידודי 8+16A+55.2 Low-E · חוץ מחוסם, פנים שכבתי	בידודי 6+12A+6 Low-E (חלון האלומיניום); מיגון: חלון הדף פלדה	בידודי 8+16A+55.2 Low-E · חוץ מחוסם, פנים שכבתי
הצללה	– (זכוכית חלבית)	תריס גלילה חשמלי נסתר, שלבי אלומיניום מוקצף	– (זכוכית חלבית)	רפפות אנכיות קבועות דמוי עץ 50/200 @180 + תריס חשמלי נסתר	וילון סקרין פנימי חשמלי	תריס גלילה חשמלי נסתר, שלבי אלומיניום מוקצף	תריס גלילה חשמלי נסתר, שלבי אלומיניום מוקצף	–	תריס פלדה נגלל/הזזה (פקע"ר)	–
מידות ר/ג · אדן	100/90 · אדן +150	130/100 · אדן +140	190/90 · אדן +150	300/230 · אדן +50	210/280 · אדן ±0	360/280 · אדן ±0	440/280 · אדן ±0	190/360 · אדן -40	100/100 · אדן +100	190/240 · אדן -20
כמות · קומה	1 יח' · א'	1 יח' · א'	1 יח' · א'	1 יח' · א'	1 יח' · א'	1 יח' · א'	1 יח' · א'	1 יח' · א'	1 יח' · א'	1 יח' · גג
מיקום · חזית	רחצה 3 · צפון	כביסה · צפון	רחצה 2 · צפון	חדר שינה 2 · מזרח	גלריה משפחתית · דרום	גלריה משפחתית · דרום	חדר שינה 2 · דרום	גלריה משפחתית · צפון	ממ"ד / חדר ילד · מערב	יציאה לגג · צפון
הערות	זכוכית חלבית לפרטיות	–	זכוכית חלבית לפרטיות	מקטע תחתון קבוע שכבתי עד 105 ס"מ (מניעת נפילה) · מאחורי מסך רפפות אנכיות	זיגוג בטיחותי עד רצפה	סף נגיש שקוע ברצפה, מנעול רב-נקודתי	סף נגיש שקוע ברצפה, מנעול רב-נקודתי	ספנדרל אטום מבודד מול התקרה, רציף בין הקומות	חלון הדף + תריס פלדה נגלל/הזזה לפי הנחיות פקע"ר · מידה מרבית 100/100, בקיר בטון מזוין	ספנדרל אטום מבודד מול התקרה, רציף בין הקומות

רשימת דלתות ונגרות

מבט מצד הפתיחה · קנ"מ 1:60 · 10 סוגים · 20 דלתות

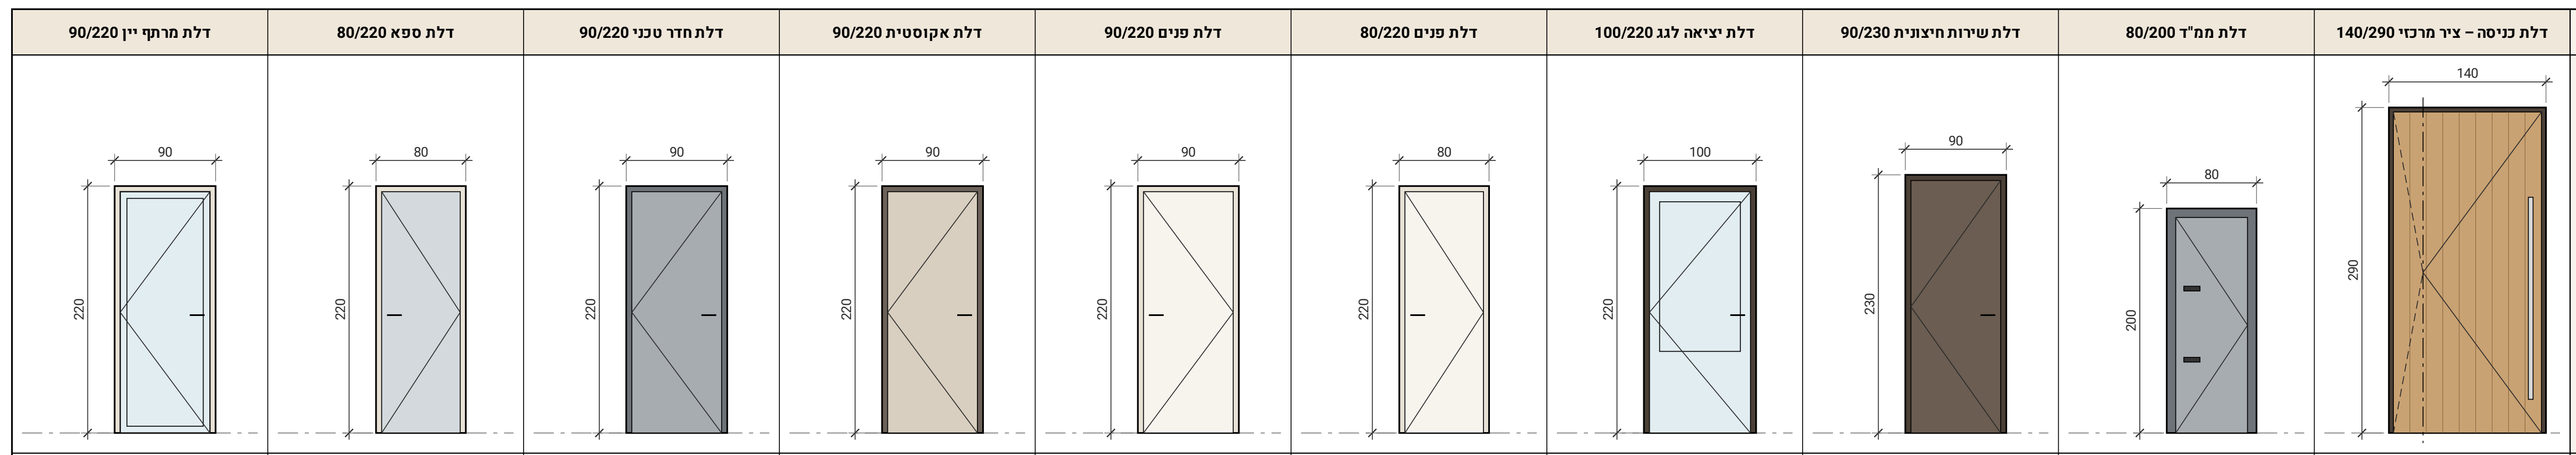

סימון	דלת כניסה – ציר מרכזי 140/290	דלת ממ"ד 80/200	דלת שירות חיצונית 90/230	דלת יציאה לגג 100/220	דלת פנים 80/220	דלת פנים 90/220	דלת אקוסטית 90/220	דלת חדר טכני 90/220	דלת ספא 80/220	דלת מרתף יין 90/220
מבט 1:60										
סימונים	D-01	M-D	D-02	D-31	D-B4, D-03, D-04, D-22, D-23, D-25, D-26	D-B2, D-B3, D-B6, D-21, D-24	D-B1	D-B7	D-B5	D-B8
סוג	דלת ציר מרכזי (Pivot)	דלת הדף ואטימה לממ"ד	דלת אלומיניום חיצונית	דלת אלומיניום חיצונית מזוגגת	דלת פנים לבודה	דלת פנים לבודה	דלת אקוסטית	דלת פלדה עמידת אש	דלת זכוכית	דלת זכוכית מבודדת
כנף וגמר	כנף מבודדת 100 מ"מ, חיפוי לוחות אלון מלא אנכיים, לכה ימית UV	פלדה, מאושרת ע"י פיקוד העורף	פנל אלומיניום תרמי מבודד, ברונזה כהה, מפרט ימי	אלומיניום תרמי + זיגוג בידודי מחוסם, ברונזה כהה	כנף לבודה 45 מ"מ, לכה לבנה מט / פורניר אלון	כנף לבודה 45 מ"מ, לכה לבנה מט / פורניר אלון	כנף מלאה 60 מ"מ, Rw≥40dB, חיפוי בד אקוסטי	פלדה מבודדת, עמידות אש 30 דק'	זכוכית מחוסמת 10 מ"מ חלבית	מסגרת פלדה שחורה + זיגוג בידודי
משקוף	משקוף אלומיניום סמוי, ציר רצפתי הידראולי	משקוף פלדה יצוק בקיר בטון מזוין	משקוף אלומיניום תרמי, סף אטימה	סף מוגבה 5 ס"מ + אטימה למים	משקוף עץ סמוי (Flush) בגובה הכנף	משקוף עץ סמוי (Flush) בגובה הכנף	משקוף פלדה, אטמים כפולים + סף נשמט	משקוף פלדה, אטם עשן	צירי נירוסטה 316, אטם לחות	אטם תרמי היקפי
פרזול	מנעול חכם (טביעת אצבע + אפליקציה), נעילה רב-נקודתית, ידית משיכה נירוסטה 316 L=180	ידיות נעילה (בריחים), אטם גומי היקפי	מנעול רב-בריחי, צילינדר מאסטר, מחזיר	מנעול רב-נקודתי, מחזיר הידראולי	ידית נירוסטה מוברשת, מנעול מגנטי שקט	ידית נירוסטה מוברשת, מנעול מגנטי שקט	ידית נירוסטה, מחזיר שקט	מחזיר הידראולי, ידית + צילינדר	ידית משיכה נירוסטה	ידית משיכה, מנעול
מידות ר/ג	140/290	80/200	90/230	100/220	80/220	90/220	90/220	90/220	80/220	90/220
כמות · קומה	1 יח' · קרקע	1 יח' · א'	1 יח' · קרקע	1 יח' · גג	7 יח' · מרתף + קרקע + א'	5 יח' · מרתף + א'	1 יח' · מרתף	1 יח' · מרתף	1 יח' · מרתף	1 יח' · מרתף
הערות	סף נגיש, אטימה היקפית, מתחת לגגון בטון	פתיחה החוצה מהממ"ד · לפי הנחיות פקע"ר העדכניות	כניסת שירות למזווה	יציאה למרפסת הגג	חדרי רחצה: נעילת פנוי/תפוס + מרווח אוורור תחתון	–	קולנוע ביתי	חדר טכני	ספא – אזור רטוב	מרתף יין מבוקר טמפרטורה

טבלת דלתות

מס'	חדר	גישה מ-	קומה	ר/ג	כיוון	סוג
D-B1	קולנוע ביתי	טרקלין ובר	מרתף	90/220	שמאל	דלת אקוסטית
D-B2	חדר כושר / יוגה	טרקלין ובר	מרתף	90/220	ימין	דלת פנים
D-B3	חדר אורחים	טרקלין ובר	מרתף	90/220	שמאל	דלת פנים
D-B4	רחצה אורחים	חדר אורחים	מרתף	80/220	ימין	דלת פנים
D-B5	ספא – סאונה ומקלחת	טרקלין ובר	מרתף	80/220	ימין	דלת ספא
D-B6	מחסן	מבואה ומדרגות	מרתף	90/220	ימין	דלת פנים
D-B7	חדר טכני	מחסן	מרתף	90/220	שמאל	דלת חדר טכני
D-B8	מרתף יין	מבואה ומדרגות	מרתף	90/220	שמאל	דלת מרתף יין
D-01	לובי כניסה	חוץ	קרקע	140/290	–	דלת כניסה – ציר מרכזי
D-02	מזווה / מטבח אחורי	חוץ	קרקע	90/230	שמאל	דלת שירות חיצונית
D-03	שירותי אורחים	מבואה ומדרגות	קרקע	80/220	שמאל	דלת פנים
D-04	מזווה / מטבח אחורי	מטבח	קרקע	80/220	ימין	דלת פנים
D-21	חדר הלבשה	פרוזדור	א'	90/220	שמאל	דלת פנים
D-22	רחצת הורים	חדר הלבשה	א'	80/220	שמאל	דלת פנים
D-23	רחצה 3	פרוזדור	א'	80/220	ימין	דלת פנים
D-24	חדר שינה 2	גלריה משפחתית	א'	90/220	שמאל	דלת פנים
D-25	רחצה 2	חדר שינה 2	א'	80/220	ימין	דלת פנים
D-26	כביסה	גלריה משפחתית	א'	80/220	ימין	דלת פנים
M-D	ממ"ד / חדר ילד	פרוזדור	א'	80/200	ימין	דלת ממ"ד
D-31	יציאה לגג	שביל גג	גג	100/220	שמאל	דלת יציאה לגג

כיוון: ימין/שמאל = צד הצירים במבט מצד הפתיחה

מקרא סימנים

סימן	הסבר
↵	הרמה-הזזה – חץ בכיוון הפתיחה
→	הזזה
▨	ציר-נטוי – קודקוד המשולש בצד הצירים
▨	נטוי (קיפ) – צירים בתחתית הכנף
– – – –	קו מקווקו – נפתח פנימה (הרחק מהצופה)
——	קו רציף – נפתח לכיוון הצופה
קבוע	קבוע – זיגוג ללא כנף
▨	ציר מרכזי – קו ציר נקודה-קו
▨	ספנדרל – פנל אטום מול תקרה
— - —	קו רצפה גמורה של הקומה (ר.ג.)

הערות כלליות

1. כל המידות בס"מ. מידות הפתחים לפי המודל; מידות ייצור – לפי מדידה באתר ואישור דוגמאות.
2. אלומיניום: פרופילים תרמיים עם גשר תרמי (Thermal Break), צבע אבקה אלקטרוסטטי בגוון ברונזה כהה, מפרט ימי (Seaside) – טיפול מקדים מוגבר לסביבה ימית. הסדרות המצוינות הן 'דוגמת' בלבד.
3. פרזול, ברגים ועוגנים – נירוסטה 316; אטמי EPDM; משקוף עיוור ואיטום היקפי בכל הפתחים החיצוניים.
4. זיגוג: Low-E בצד הפנימי של הזכוכית החיצונית, מרווח ארגון; זכוכית בטיחותית (מחוסמת/שכבתית) בכל זיגוג עד רצפה, בדלתות ובמקטעים נמוכים – לפי התקנים הישראליים.
5. תריסי גלילה חשמליים נסתרים – ארגז בשקע בתקרה/בקורה מעל המשקוף; רפפות אנכיות מאלומיניום דמוי עץ 50/200 @180 בחזיתות מערב ומזרח של קומה א'.
6. חלון ודלת ממ"ד – לפי הנחיות פיקוד העורף העדכניות; האלומיניום אינו חלק ממערך המיגון.
7. הרשימה מופקת אוטומטית מהמודל הפרמטרי – סימונים, כמויות ומידות לפי מצב המודל.

בית כורכר

BEIT KURKAR

שם הפרויקט:
וילת בוטיק בקיסריה

מיקום הפרויקט:
קיסריה, רובע 13 (מגרש לימודי)

מנחה:
שירן שריקי

שם הגיליון:
רשימת אלומיניום ונגרות

מס' גיליון:
18

קנ"מ:
1:50

רשימת גיליונות:

01	שער	
02	קונספט ומחקר	
03	ניתוח אתר וסביבה	
04	תכנית העמדה וטבלת שטחים	1:200
05	תכנית פיתוח שטח	1:100
06	תכניות מרתף וקרקע	1:100
07	תכניות קומה א' וגג	1:100
08	חזיתות	1:100
09	חתכים	1:100
10	סכמות סטטיות	1:100
11	תכנית קומת קרקע	1:50
12	תכנית קומה א'	1:50
13	חזיתות	1:50
14	חתך A-A	1:50
15	חתך B-B	1:50
16	גיליון מדרגות	1:25, 1:5
17	פרטי בניין	1:20, 1:5
18	**רשימת אלומיניום ונגרות**	1:50
19	עיצוב פנים – חלל המגורים	1:50
20	עיצוב ריהוט – אי המטבח	1:25, 1:10, 1:2
21	הדמיות חוץ	
22	הדמיות פנים	
23	תודה	

מגמה:
הנדסאים – אדריכלות ועיצוב פנים

שם המגיש/ה ות.ז.:
__________ __________

תאריך:
10.2026