בית כורכר

BEIT KURKAR

שם הפרויקט:
וילת בוטיק בקיסריה

מיקום הפרויקט:
קיסריה, רובע 13 (מגרש לימודי)

מנחה:
שירן שריקי

שם הגיליון:
עיצוב פנים – חלל המגורים

מס' גיליון: **19**
קנ"מ: 1:50

רשימת גיליונות:
01 שער
02 קונספט ומחקר
03 ניתוח אתר וסביבה
04 תכנית העמדה וטבלת שטחים 1:200
05 תכנית פיתוח שטח 1:100
06 תכניות מרתף וקרקע 1:100
07 תכניות קומה א' וגג 1:100
08 חזיתות 1:100
09 חתכים 1:100
10 סכמות סטטיות 1:100
11 תכנית קומת קרקע 1:50
12 תכנית קומה א' 1:50
13 חזיתות 1:50
14 חתך A-A 1:50
15 חתך B-B 1:50
16 גיליון מדרגות 1:25, 1:5
17 פרטי בניין 1:20, 1:5
18 רשימת אלומיניום ונגרות 1:50
19 עיצוב פנים – חלל המגורים 1:50
20 עיצוב ריהוט – אי המטבח 1:25, 1:10, 1:2
21 הדמיות חוץ
22 הדמיות פנים
23 תודה

מגמה:
הנדסאים – אדריכלות ועיצוב פנים

שם המגיש/ה ות.ז.:
__________ __________

תאריך:
10.2026

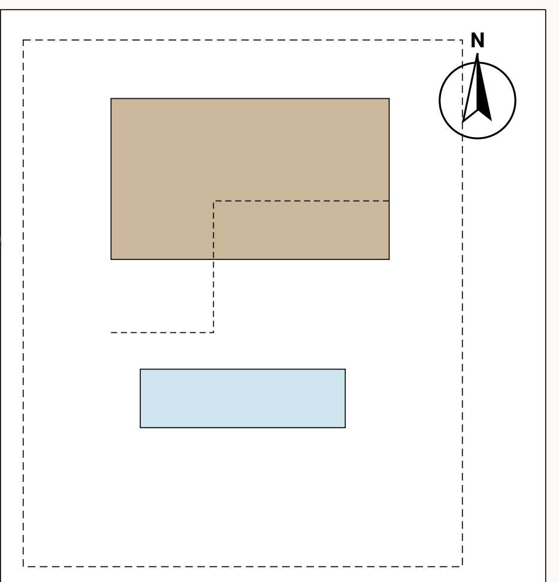

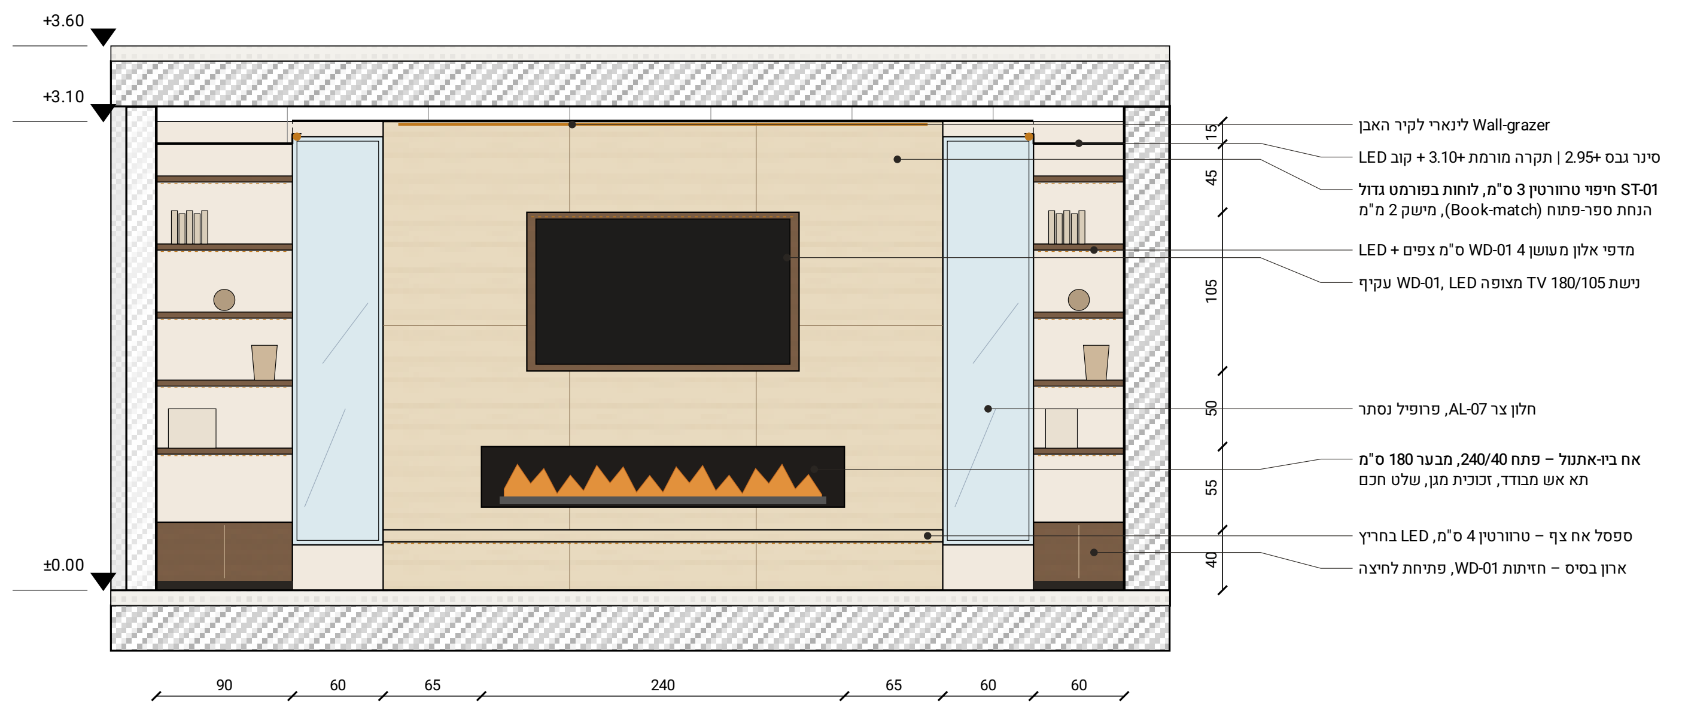

לינארי לקיר האבן Wall-grazer
סינר גבס +2.95 | תקרה מורמת +3.10 + קוב LED
ST-01 חיפוי טרוורטין 3 ס"מ, לוחות בפורמט גדול
הנחת ספר-פתוח (Book-match), מישק 2 מ"מ
מדפי אלון מעושן WD-01 4 ס"מ צפים + LED
נישת TV 180/105 מצופה WD-01, LED עקיף
חלון צר AL-07, פרופיל נסתר
אח ביו-אתנול – פתח 240/40, מבער 180 ס"מ
תא אש מבודד, זכוכית מגן, שלט חכם
ספסל אח צף – טרוורטין 4 ס"מ, LED בחריץ
ארון בסיס – חזיתות WD-01, פתיחת לחיצה

חתך-חזית 1-1 – קיר האח

קנ"מ 1:50

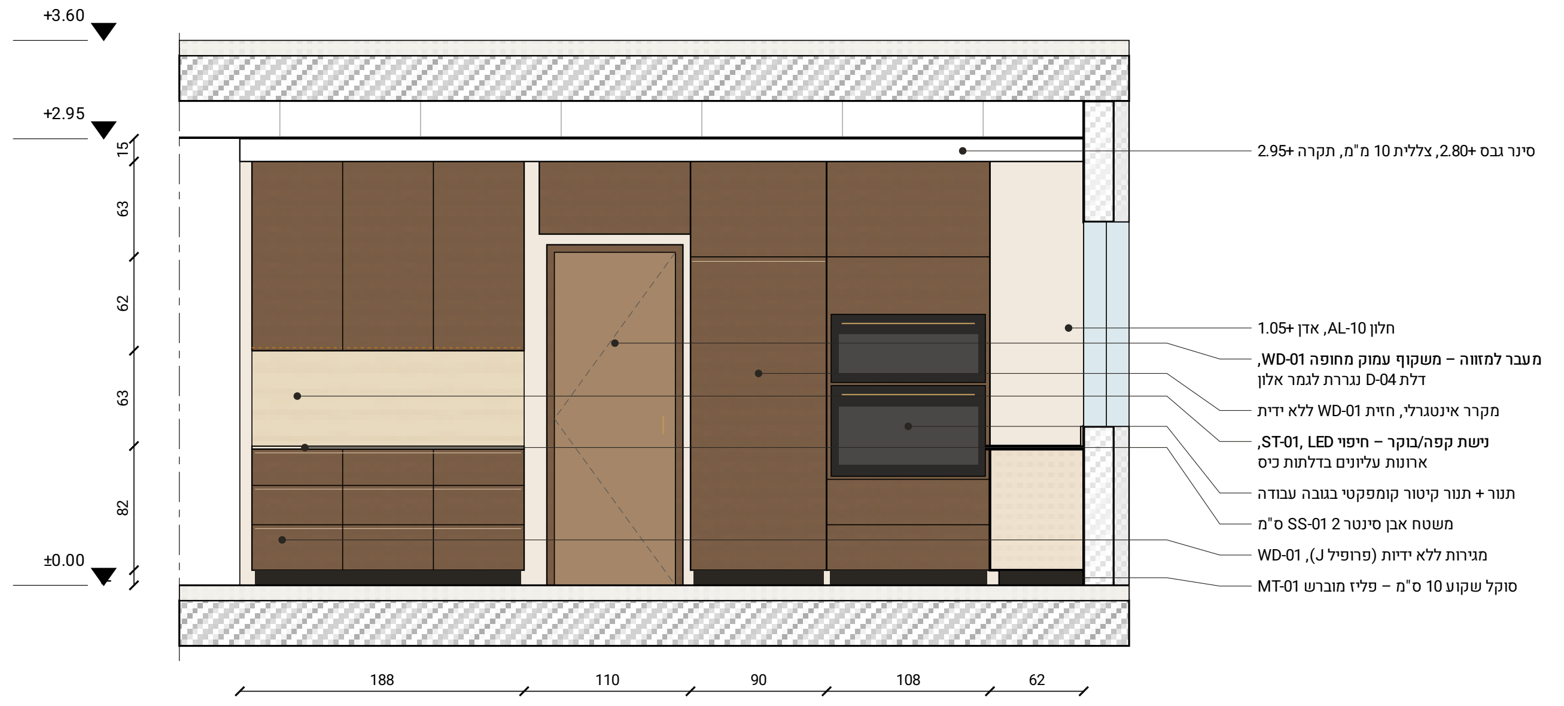

סינר גבס +2.80, צללית 10 מ"מ, תקרה +2.95
חלון AL-10, אדן +1.05
מעבר למזווה – משקוף עמוק מחופה WD-01,
דלת D-04 נגררת לגמר אלון
מקרר אינטגרלי, חזית WD-01 ללא ידית
נישת קפה/בוקר – חיפוי ST-01, LED,
ארונות עליונים בדלתות כיס
תנור + תנור קיטור קומפקטי בגובה עבודה
משטח אבן סינטר SS-01 2 ס"מ
מגירות ללא ידיות (פרופיל J), WD-01
סוקל שקוע 10 ס"מ – פליז מוברש MT-01

חתך-חזית 2-2 – קיר המטבח

קנ"מ 1:50

סמל	קוד	תיאור
▭	FL-01	פורצלן 120/120/0.9 מט R10, מישק 2 מ"מ
▭	FL-02	פורצלן 120/120/2.0 R11 חוץ – המשך המישקים
▭	ST-02	אבן גיר כורכר 60/120 מוברשת, חצי-קשר
▭	FL-03	פורצלן 60/120 – שירותי אורחים
▭	FL-04	פורצלן 60/60 – מזווה
—	TH-01	פס מעבר פליז מוברש T-12, מפלס אחיד
-------	DR-01	ספ שטוח + תעלת ניקוז לינארית (חוץ)
◉	SP	נקודת התחלה – אריח שלם בויטרינה

פרט סף ויטרינה שטוח (פנים-חוץ)

קנ"מ 1:10

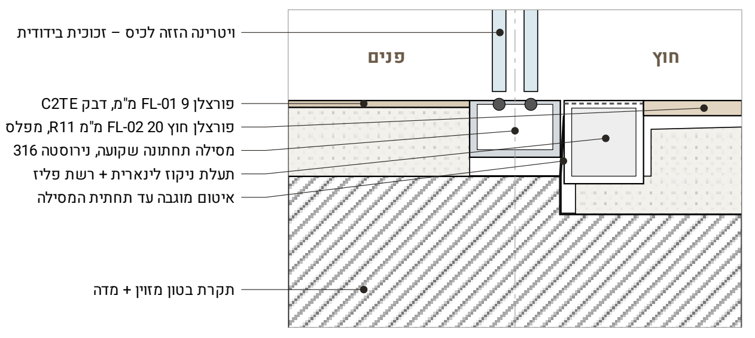

ויטרינה הזזה לכיס – זכוכית בידודית
פורצלן FL-01 9 מ"מ, דבק C2TE
פורצלן חוץ FL-02 20 מ"מ R11, מפלס זהה
מסילה תחתונה שקועה, נירוסטה 316
תעלת ניקוז לינארית + רשת פליז
איטום מוגבה עד תחתית המסילה
תקרת בטון מזוין + מדה

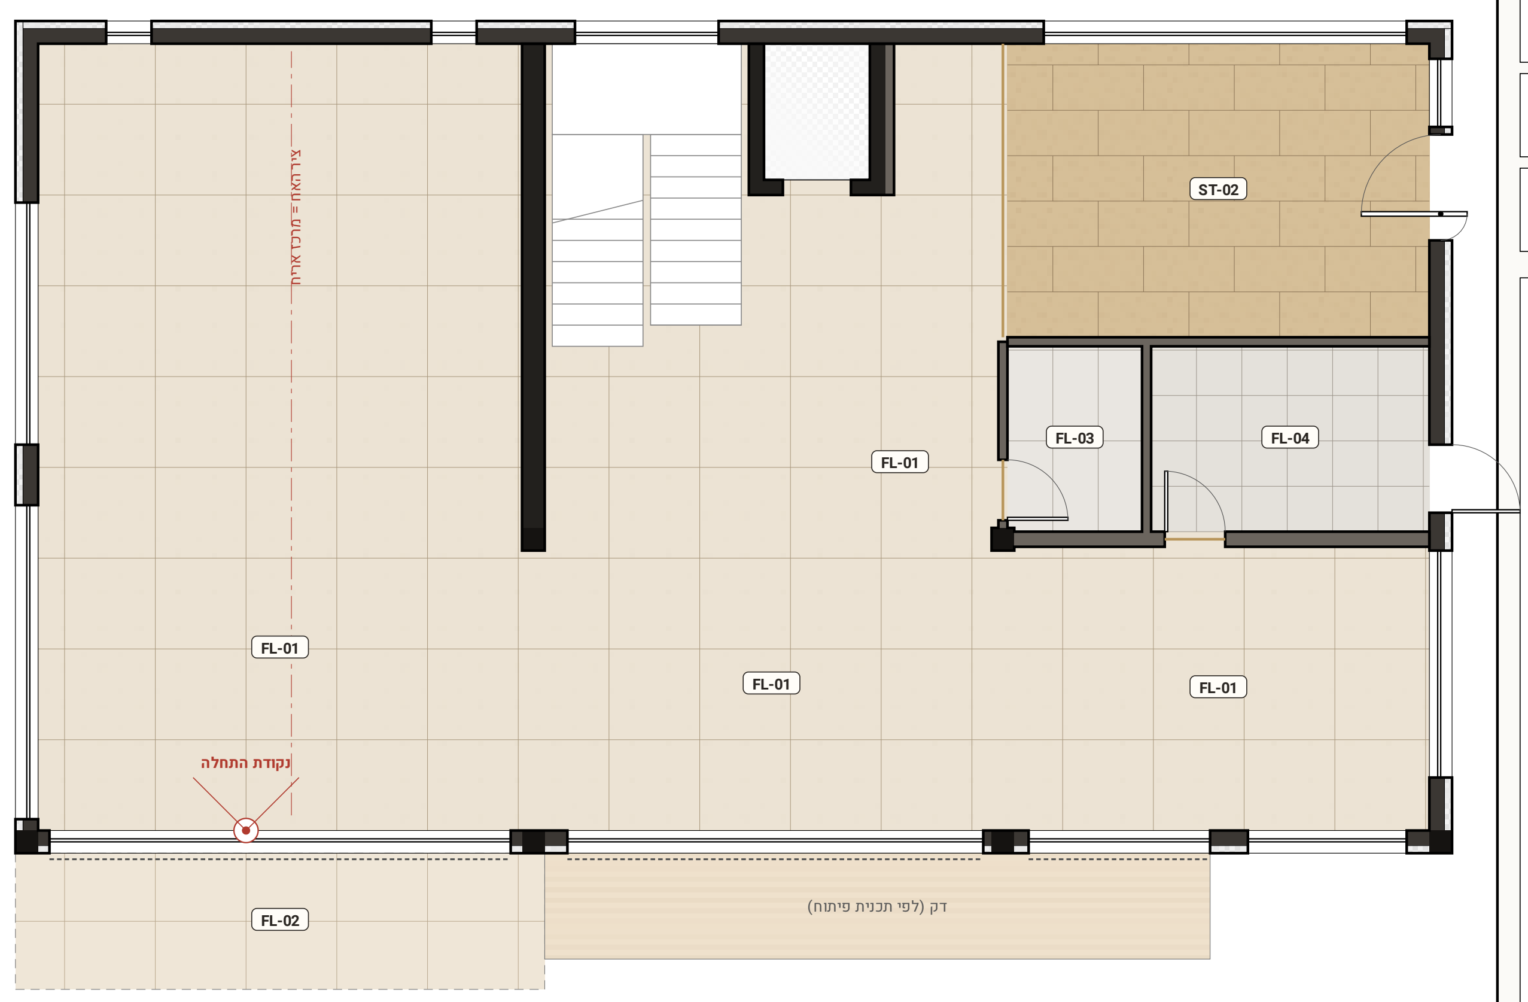

תכנית ריצוף

קנ"מ 1:100

* קנ"מ מוקטן לשם התאמה לגיליון; מידות בס"מ.

סצנות תאורה חכמה

סצנה	תאורה פעילה	עוצמה / גוון
בוקר	L1 + L4 + L3 מטבח, וילונות פתוחים	70% | 3000K
ארוחה	L7 + L6 + L3 פינת אוכל, L1 נמוך	60% | 2700K
ערב רגוע	L1 + L3 + L5 + L8 כבוי אח,	35% | 2200K
קולנוע	L8 נישת TV בלבד, וילונות סגורים	10% | 1800K
יציאה	הכל כבוי, L4 לובי 10%, מיזוג Eco	—

הערות:
1. כל המידות בס"מ, מפלסים במ'. יש לאמת מידות באתר.
2. גופי תאורה עמעום DALI-2, בקרת סצנות KNX.
3. תיאום תקרות עם יועץ מיזוג וחשמל לפני ביצוע.
4. ריצוף 120/120 – ריצוף רטוב-רזה, פילוס ±1 מ"מ.

מקרא תאורה ומערכות תקרה

סמל	קוד	תיאור	מפרט	כמות
◉	L1	ספוט שקוע Trimless Ø75, מוחשך	10W 2700K CRI≥95 UGR<16, 36°	31
◉	L2	ספוט שקוע מתכוונן (wall-wash)	10W 2700K, 24°, הטיה 30°	4
– – –	L3	תאורת קוב LED בתקרה מורמת	14W/מ' 1800K→3000 Dim-to-warm	60 מ'
▭	L4	פרופיל לינארי שקוע 35 מ"מ	12W/מ' 3000K, מפזר אופל	24 מ'
⊥	L5	לינארי לקיר האבן Wall-grazer	15W/מ' 2700K, אופטיקה 10×60	4 מ'
⊕	L6	גוף תלוי מעל האי – זכוכית מעושנת/פליז	Ø25, 8W 2700K, גובה +1.65	3
▬	L7	גוף תלוי לינארי מעל שולחן האוכל	פליז מוברש, 30W, גובה +1.60	1
---------	L8	פס LED בנגרות (מדפים, נישות, סוקל)	6W/מ' 2700K, פרופיל אלומ'	14 מ'
●	L9	גוף תלוי פיסולי בחלל המדרגות	7 גופים, זכוכית + פליז	1
▭	M1	מפזר אוויר לינארי (Slot) – אספקה	2 חריצים, צבע לבן	4
▦	M2	תריס אוויר חוזר	60/30, בגוון התקרה	2
⬚	M3	יח' מיזוג מוסתרת (ת.ת. +2.60)	מעל מזווה, גישה 50/50	2
Ⓢ	S1	גלאי עשן אופטי	מחובר למערכת הבית החכם	3
Ⓗ	S2	גלאי חום (מטבח)		1
◎	A1	רמקול תקרה שקוע	Ø20, גריל דק בגוון התקרה	4
■	K1	לוח סצנות חכם (KNX/DALI)	גובה +1.10, זכוכית/פליז	3
— - —	C1	מסילת וילון שקועה (מנוע)	פשתן TX-01, מסילה בסינר	24 מ'
▼+2.95	–	גובה תחתית תקרה (ת.ת.) מ-±0.00		

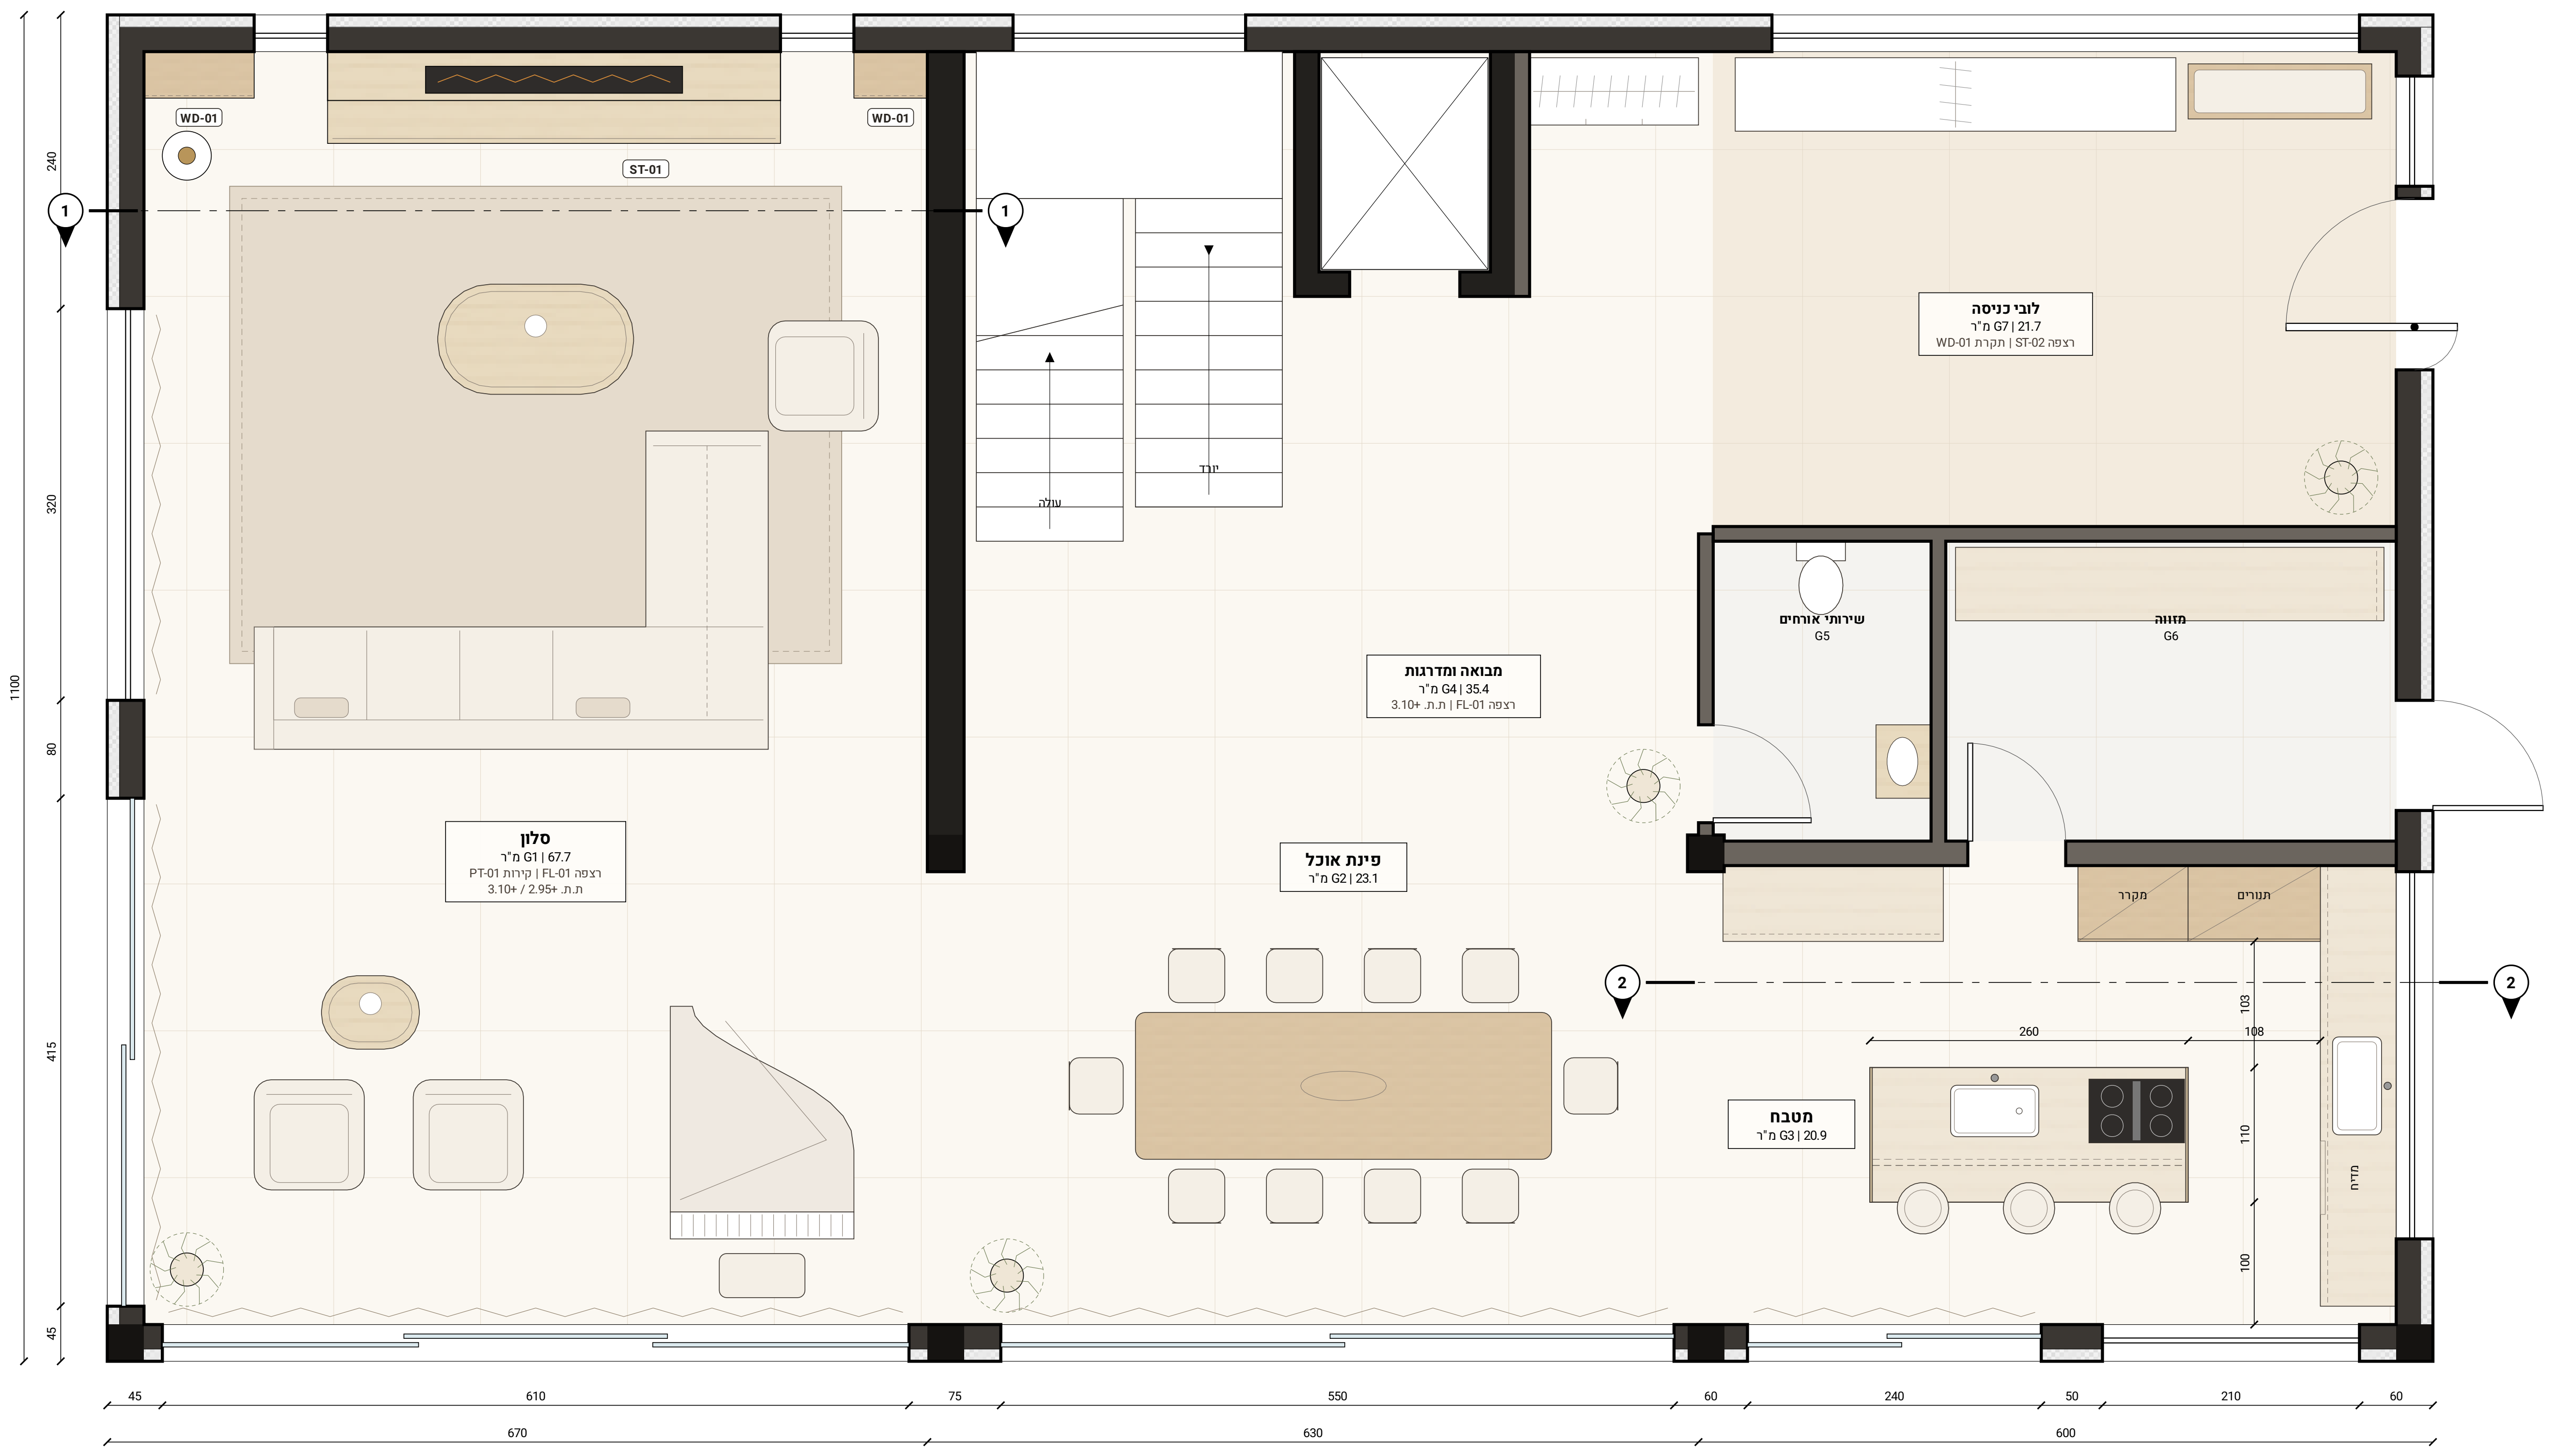

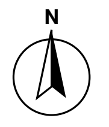

ריהוט לפי מודל; גמרים לפי פלטת החומרים.
ויטרינות הזזה לכיס נסתר, פרופיל צר, סף שטוח.

תכנית ריהוט וגמרים – חלל המגורים

קנ"מ 1:50

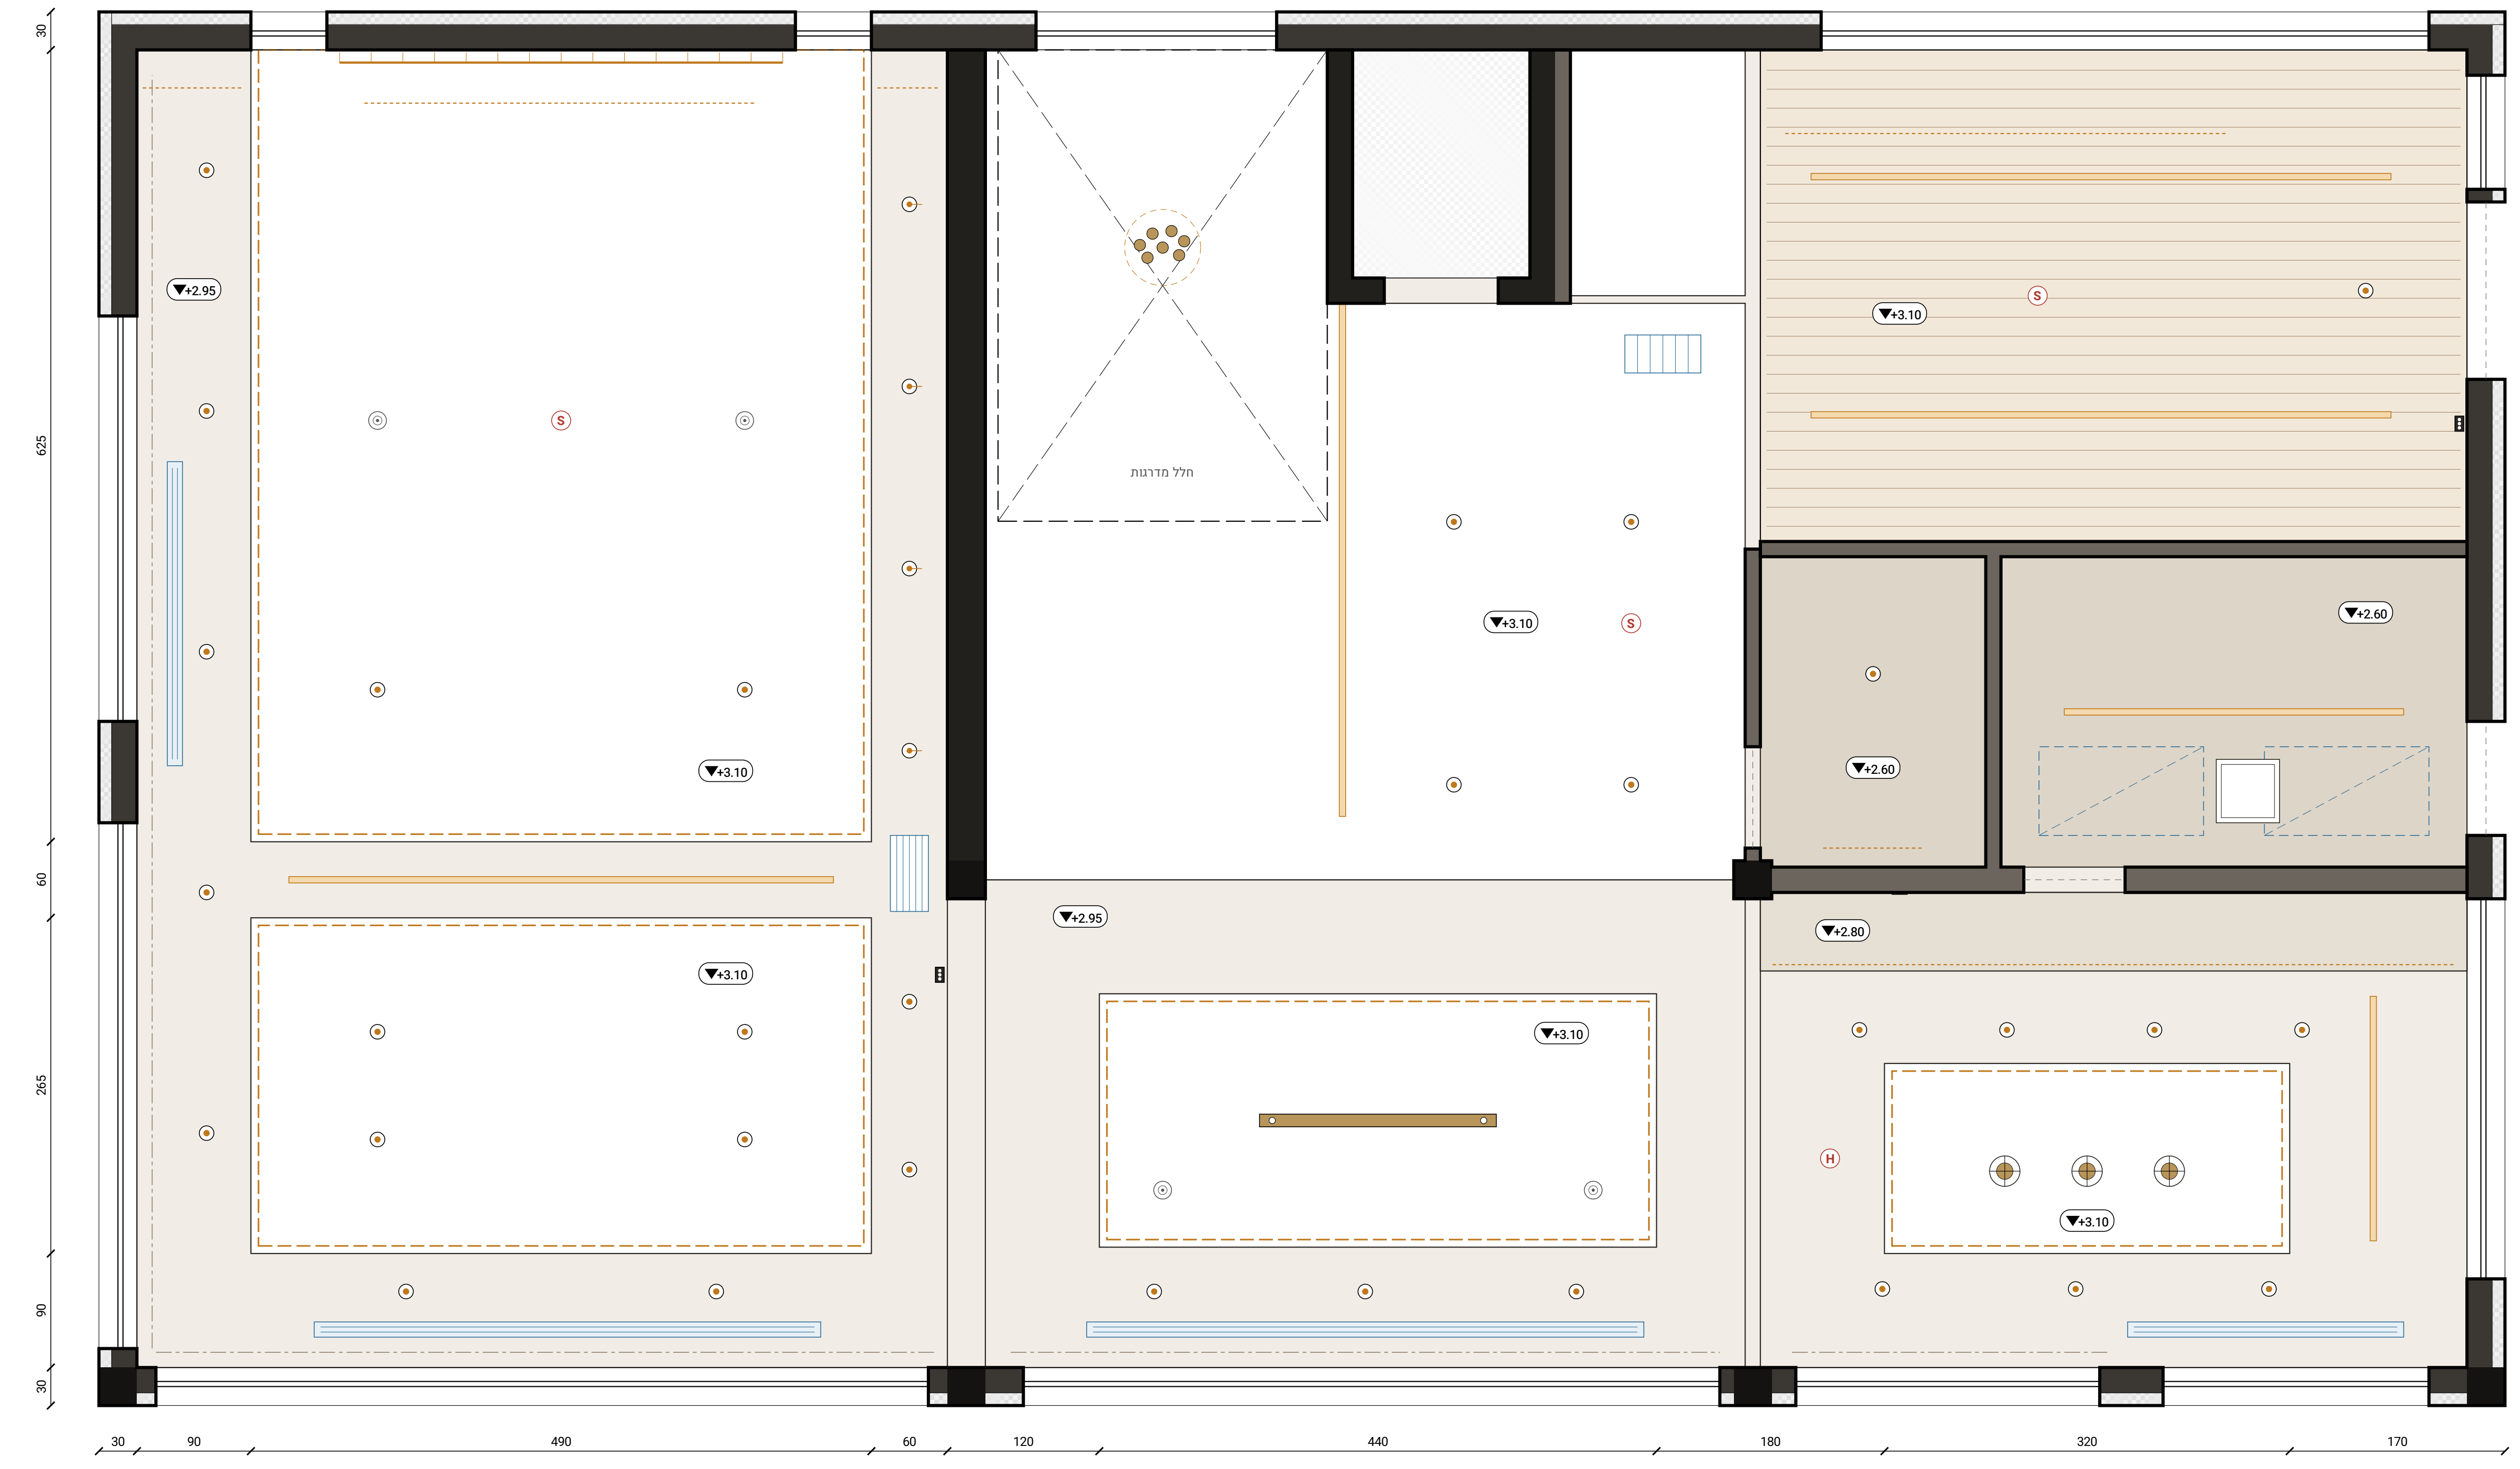

תקרות גבס: סינר +2.95 לאורך הויטרינות (מסילות וילון, מיזוג),
תקרות מורמות +3.10 עם קוב LED; מטבח – סינר +2.80 מעל הארונות.

תכנית תקרה מוחזרת ותאורה

קנ"מ 1:50

פלטת חומרים *Quiet luxury*										
	ST-01 TRV-CL-H30 טרוורטין קלאסי מושחז, ממולא | 3 ס"מ קיר האח, ספסל	**ST-02** LMS-KR-B20 אבן גיר גוון כורכר מוברש | 60/120/2 רצפת לובי	**FL-01** POR-SND-1212 פורצלן Sand Stone 120/120 מט R10 / R11 רצפות + מרפסת	**SS-01** SNT-TRV-20 אבן סינטר טרוורטין 20 מ"מ, מט משטחים, אי	**WD-01** OAK-SMK-V06 אלון מעושן פורניר, שמן-לכה מט נגרות, תקרת לובי	**WD-02** OAK-FLT-22 אלון מעושן מחורץ מלא 22 מ"מ, חריץ 20 חזית אי המטבח	**MT-01** BRS-BR-PVD פליז מוברש PVD, לכה מגינה פרופילים, סוקל	**TX-01** LIN-SND-280 פשתן טבעי – חול וילון שקוף + ריפוד וילונות, ספות	**PT-01** LMW-MCH-02 טיח סיד – מוקה בהיר Lime-wash, מט קירות	**LT-01** NAP-MCH-12 עור נאפה מוקה עובי 1.2 מ"מ כסאות, ידיות

הדמיה 1 – סלון ואח
הדמיה – בהכנה

הדמיה 2 – מטבח ופינת אוכל
הדמיה – בהכנה