בית כורכר

BEIT KURKAR

שם הפרויקט:
וילת בוטיק בקיסריה

מיקום הפרויקט:
קיסריה, רובע 13 (מגרש לימודי)

מנחה:
שירן שריקי

שם הגיליון:
עיצוב ריהוט – אי המטבח

מס' גיליון: **20**

קנ"מ: 1:25, 1:10, 1:2

רשימת גיליונות:

01	שער	
02	קונספט ומחקר	
03	ניתוח אתר וסביבה	
04	תכנית העמדה וטבלת שטחים	1:200
05	תכנית פיתוח שטח	1:100
06	תכניות מרתף וקרקע	1:100
07	תכניות קומה א' וגג	1:100
08	חזיתות	1:100
09	חתכים	1:100
10	סכמות סטטיות	1:100
11	תכנית קומת קרקע	1:50
12	תכנית קומה א'	1:50
13	חזיתות	1:50
14	חתך A-A	1:50
15	חתך B-B	1:50
16	גיליון מדרגות	1:25, 1:5
17	פרטי בניין	1:20, 1:5
18	רשימת אלומיניום ונגרות	1:50
19	עיצוב פנים – חלל המגורים	1:50
20	**עיצוב ריהוט – אי המטבח**	1:25, 1:10, 1:2
21	הדמיות חוץ	
22	הדמיות פנים	
23	תודה	

מגמה:
הנדסאים – אדריכלות ועיצוב פנים

שם המגיש/ה ות.ז.:
__________ __________

תאריך:
10.2026

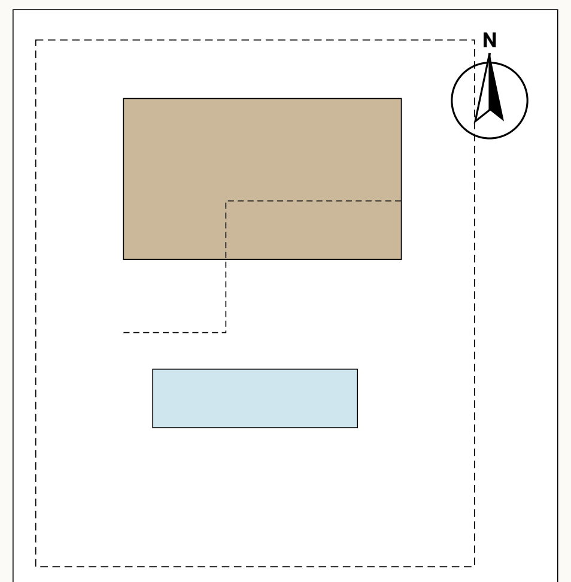

חתך A-A דרך מודול המגירות

קנ"מ 1:10

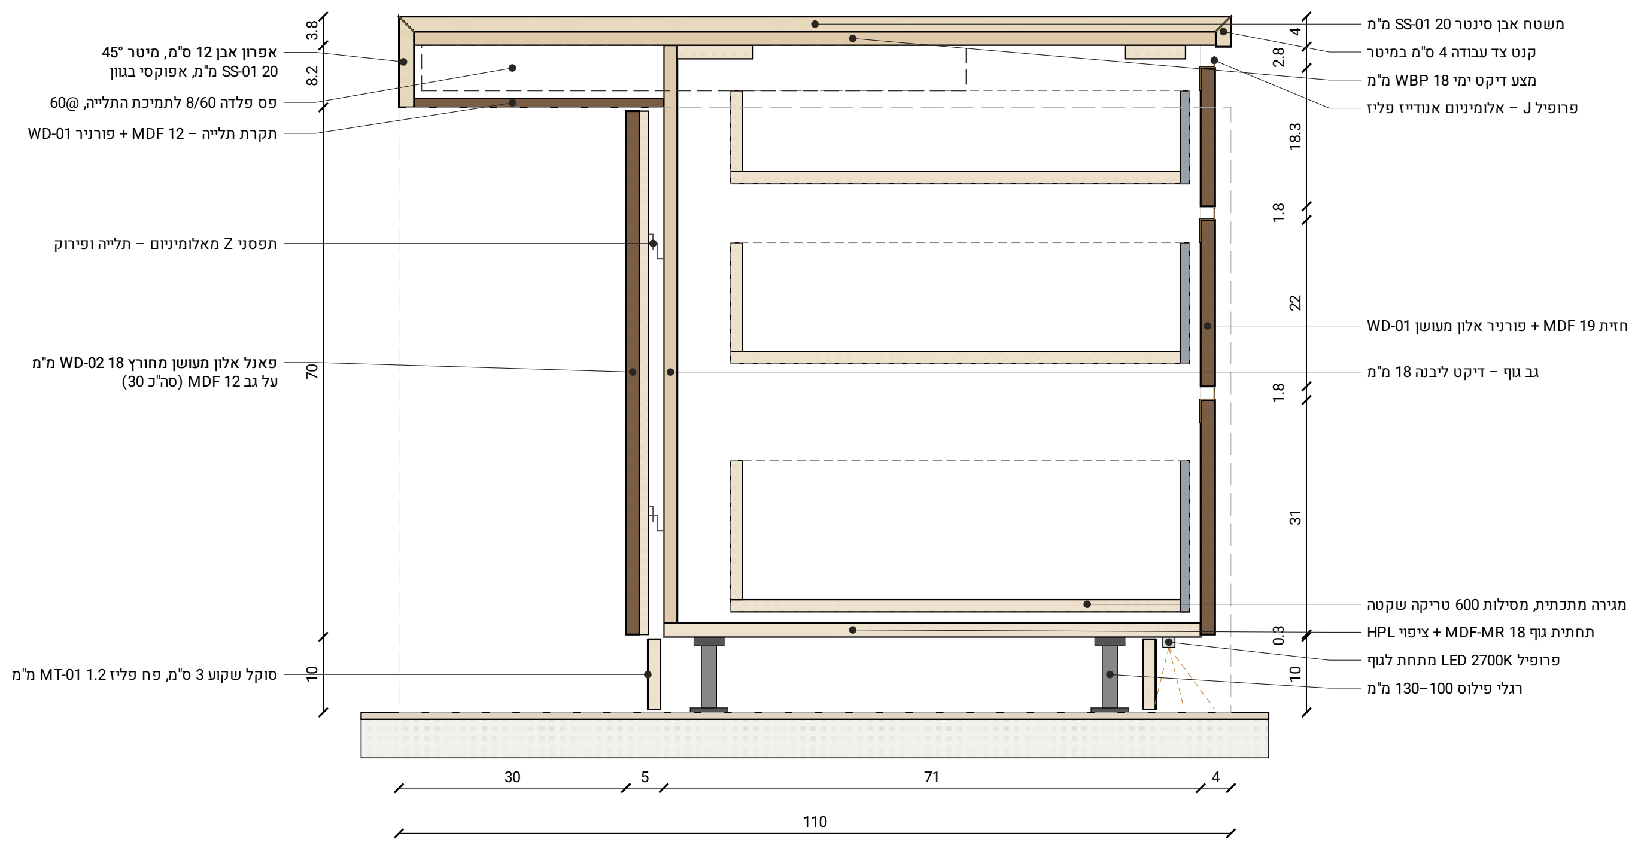
משטח אבן סינטר SS-01 20 מ"מ
קנט צד עבודה 4 ס"מ במיטר
מצע דיקט ימי WBP 18 מ"מ
פרופיל J – אלומיניום אנודייז פליז
חזית MDF 19 + פורניר אלון מעושן WD-01
גב גוף – דיקט ליבנה 18 מ"מ
מגירה מתכתית, מסילות 600 טריקה שקטה
תחתית גוף MDF-MR 18 + ציפוי HPL
פרופיל LED 2700K מתחת לגוף
רגלי פילוס 100–130 מ"מ
אפרון אבן 12 ס"מ, מיטר 45°
SS-01 20 מ"מ, אפוקסי בגוון
פס פלדה 8/60 לתמיכת התלייה, @60
תקרת תלייה – MDF 12 + פורניר WD-01
תפסני Z מאלומיניום – תלייה ופירוק
פאנל אלון מעושן מחורץ WD-02 18 מ"מ
על גב MDF 12 (סה"כ 30)
סוקל שקוע 3 ס"מ, פח פליז 1.2 MT-01 מ"מ
3.8
8.2
70
10
4
2.8
18.3
1.8
22
1.8
31
0.3
10
30
5
71
4
110

מבט איזומטרי – ללא קנ"מ

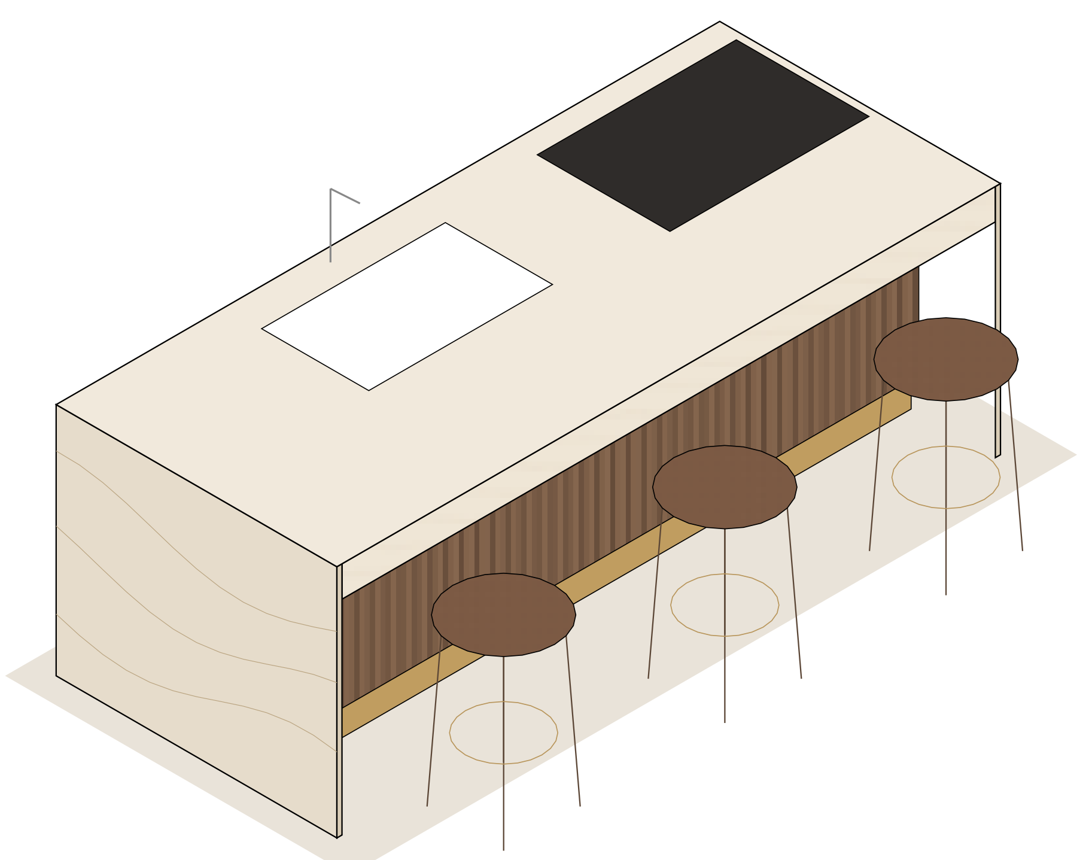

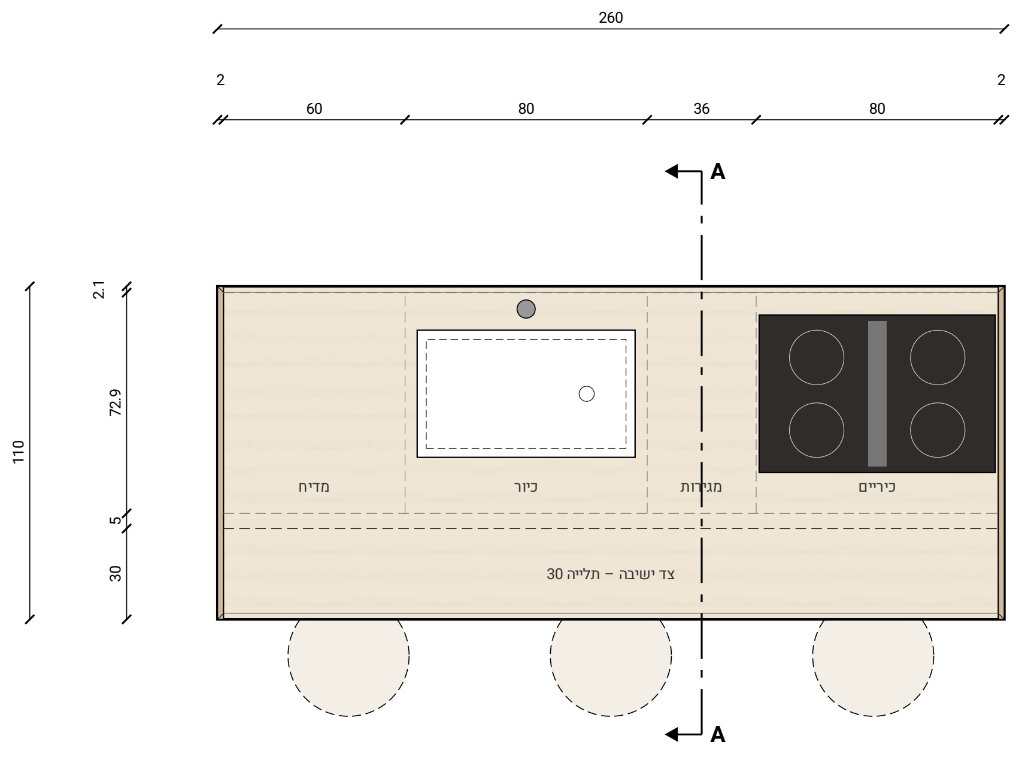

תכנית אי

קנ"מ 1:25

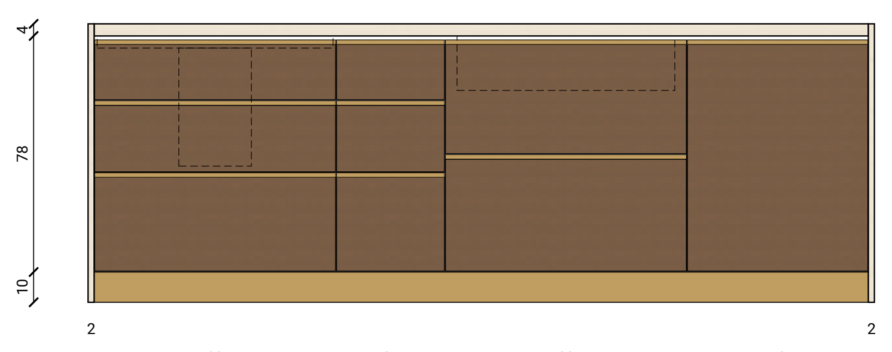

חזית צד עבודה (צפון)

קנ"מ 1:25

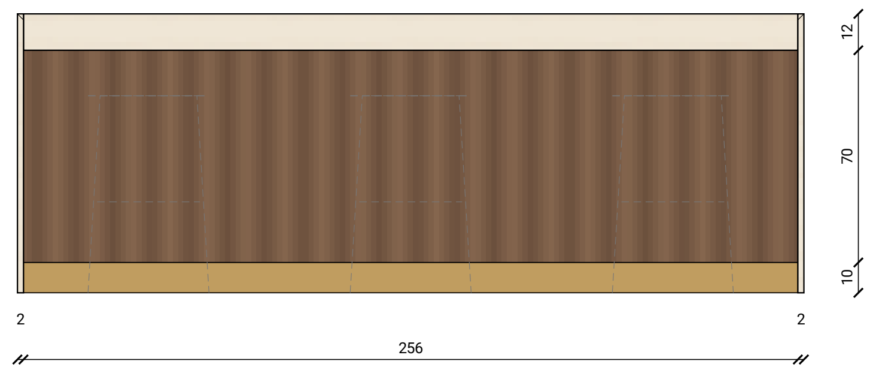

חזית צד ישיבה (דרום)

קנ"מ 1:25

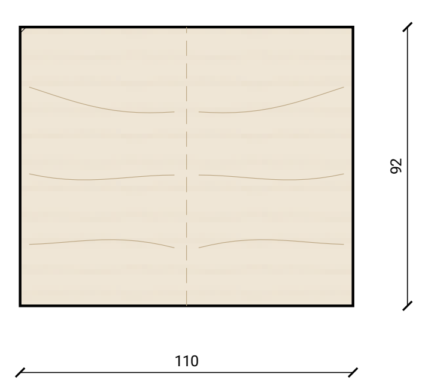

חזית קצה – רגל מפל

קנ"מ 1:25

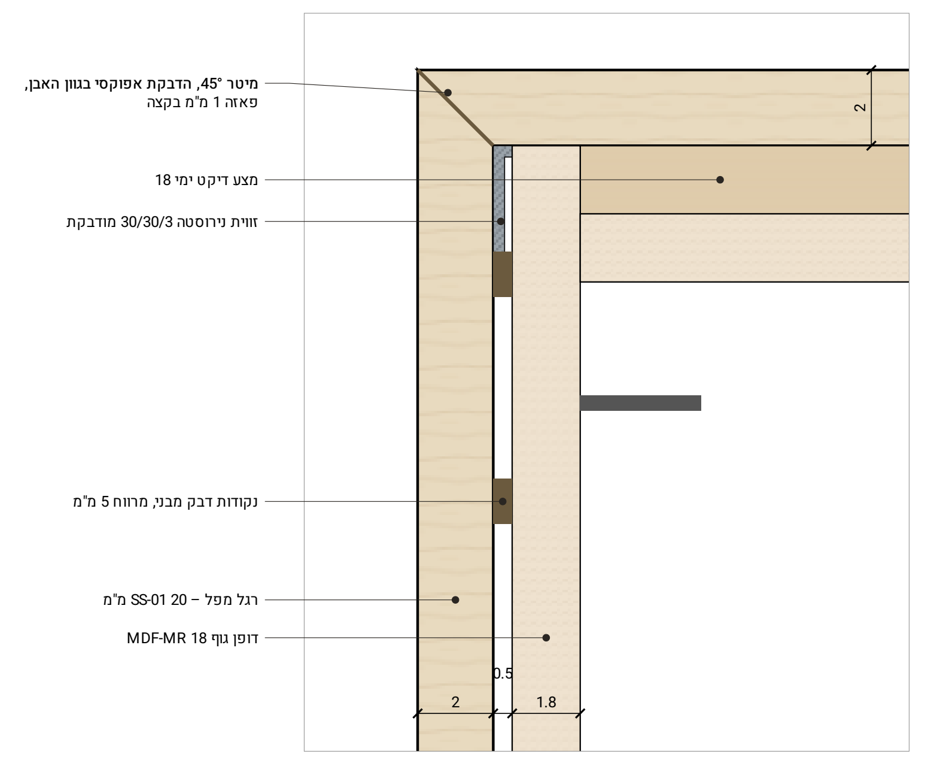
מיטר 45°, הדבקת אפוקסי בגוון האבן,
פאזה 1 מ"מ בקצה
מצע דיקט ימי 18
זווית נירוסטה 30/30/3 מודבקת
נקודות דבק מבני, מרווח 5 מ"מ
רגל מפל – SS-01 20 מ"מ
דופן גוף MDF-MR 18
2
0.5
2
1.8

פרט 1 – מיטר משטח/מפל

קנ"מ 1:2

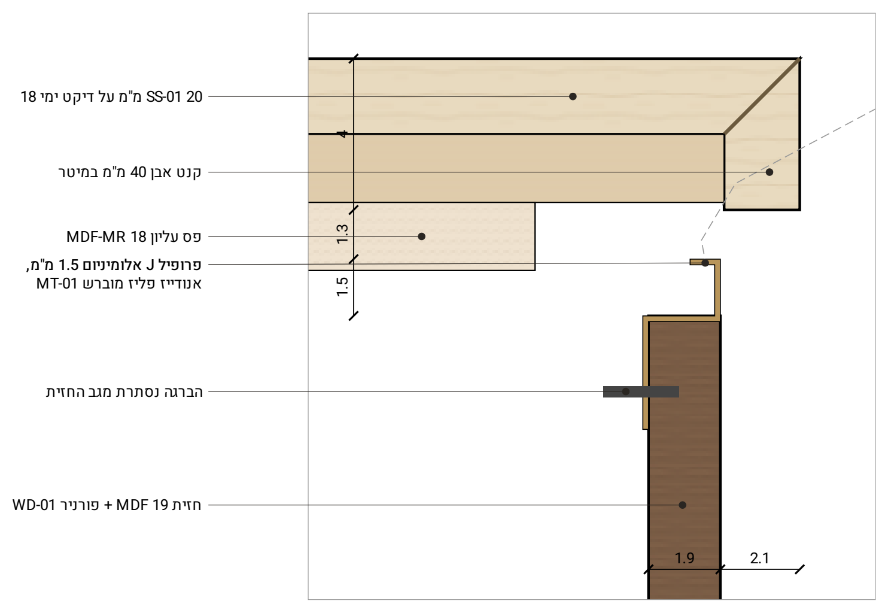

פרט 2 – ידית פרופיל J

קנ"מ 1:2

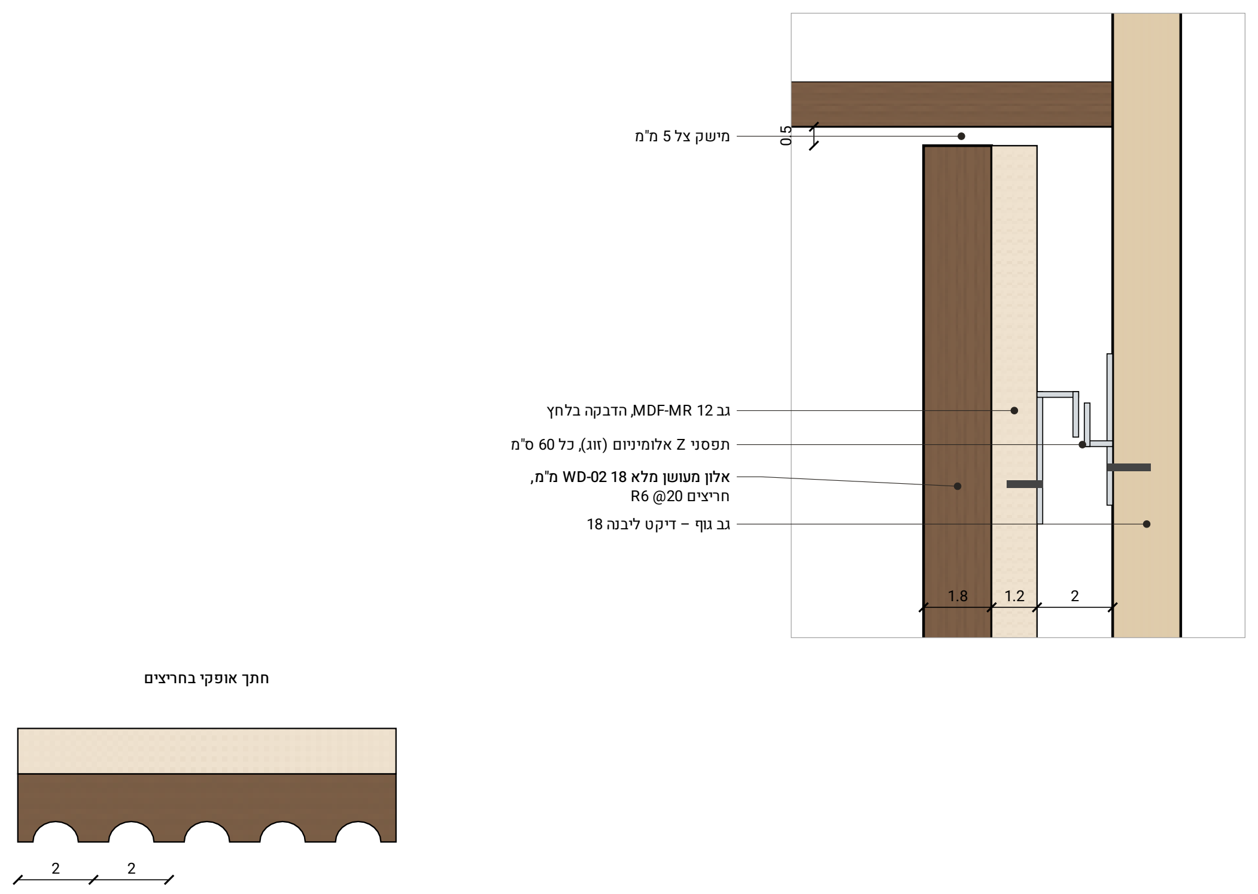

פרט 3 – קיבוע פאנל מחורץ

קנ"מ 1:2

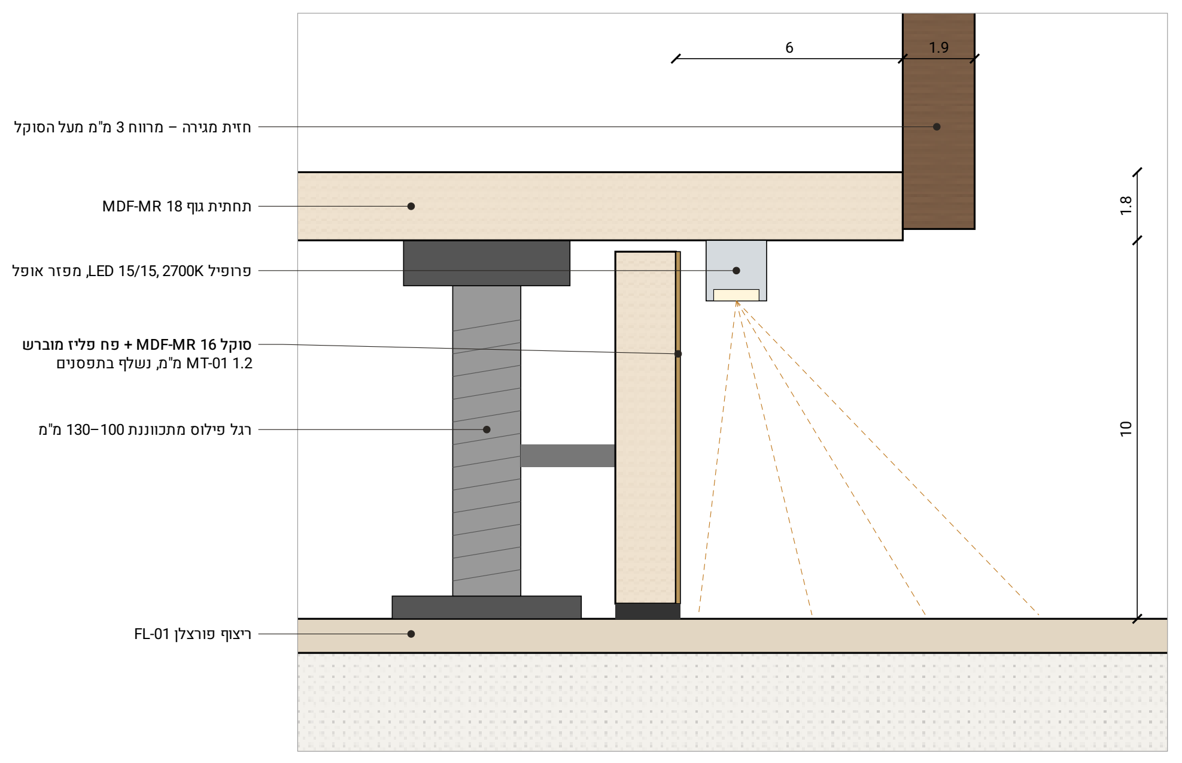
6
1.9
חזית מגירה – מרווח 3 מ"מ מעל הסוקל
תחתית גוף MDF-MR 18
פרופיל LED 15/15, 2700K, מפזר אופל
סוקל MDF-MR 16 + פח פליז מוברש
MT-01 1.2 מ"מ, נשלף בתפסנים
רגל פילוס מתכווננת 100–130 מ"מ
ריצוף פורצלן FL-01
1.8
10

פרט 4 – סוקל, LED ורגלי פילוס

קנ"מ 1:2

רשימת חיתוך וחומרים – אי מטבח

מס'	פריט	חומר	עובי	מידות (מ"מ)	כמות	הערות
1	משטח עליון	אבן סינטר SS-01	20	2600×1100	1	קנטים במיטר 45°, פתחי CNC
2	רגלי מפל (Waterfall)	אבן סינטר SS-01	20	920×1100	2	מיטר 45° לעליון, הדבקת אפוקסי
3	אפרון צד ישיבה	אבן סינטר SS-01	20	2560×100	1	מיטר 45°, המשך ורידים
4	קנט צד עבודה	אבן סינטר SS-01	20	2560×20	1	מיטר 45°
5	מצע למשטח	דיקט ימי WBP	18	2556×1060	1	הדבקה+בורגי ריתום לגוף
6	דפנות גוף	MDF-MR + HPL פנים	18	782×710	4	קנט ABS 1 מ"מ
7	תחתיות גוף	MDF-MR + HPL	18	רוחב מודול×710	3	לפי מודולים
8	גב גוף (צד ישיבה)	דיקט ליבנה	18	1280×782	2	חיבור בשגם במרכז
9	פסי חיזוק עליונים	MDF-MR	18	רוחב מודול×100	6	קדמי + אחורי
10	חזיתות מגירות / מדיח	MDF 19 + פורניר WD-01	19	לפי חזית אחורית	9	מישק 3 מ"מ, שמן-לכה מט
11	פרופיל J	אלומיניום אנודייז פליז	1.5	רוחב חזית×30	9	MT-01, הברגה נסתרת
12	מגירות מתכת	מערכת מגירות, טריקה שקטה	—	600	8	פתיחה מלאה, 70 ק"ג
13	פאנל מחורץ	אלון מעושן מלא WD-02	18	1280×692	2	חריצים R6 @20, שמן מט
14	גב לפאנל המחורץ	MDF-MR	12	1280×692	2	הדבקה בלחץ
15	תקרת תלייה (סופיט)	MDF-MR 12 + פורניר WD-01	12	2560×330	1	נשלף לתחזוקה
16	פסי פלדה לתלייה	פלדה שטוחה מגלוונת	8	60×700	4	@600, מעוגנים בגוף
17	תפסני Z	אלומיניום	2	2460	2	זוג פסים לפאנל
18	סוקל (2 צדדים)	MDF-MR 16 + פליז 1.2 MT-01	16	2560×94	2	תפסני סוקל + רצועת איטום
19	פרופיל LED	אלומיניום + מפזר אופל	—	2460	1	24V/2700K, 6W/מ', ספק 24V
20	רגלי פילוס	PP מחוזק, 100–130	—	—	12	עומס 150 ק"ג/יח'
21	בטנת תא כיור	HPL לבן עמיד מים	0.8	800×700	1	+ מגש איסוף מאלומיניום

מידות כלליות: 260×110×92 ס"מ (לפי המודל). מידות לייצור – לאחר מדידה באתר ואישור דוגמאות.

חומרי האי

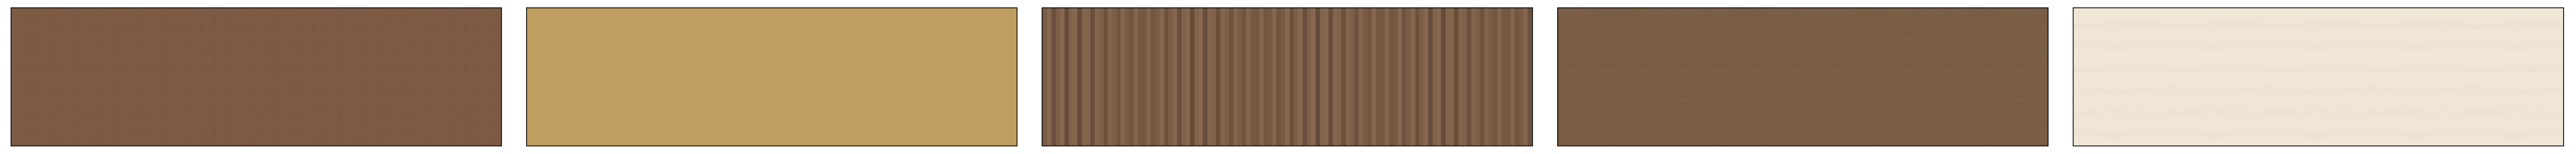

SS-01
אבן סינטר טרוורטין
20 מ"מ, מט

WD-01
אלון מעושן
פורניר, שמן-לכה מט

WD-02
אלון מעושן מחורץ
מלא 22 מ"מ, חריץ 20

MT-01
פליז מוברש
PVD, לכה מגינה

LT-01
עור נאפה מוקה
עובי 1.2 מ"מ

מפרט אביזרים וגמרים

- כיור אינטגרלי תחתון 70/40 נירוסטה, ברז נשלף פליז מוברש
- כיריים אינדוקציה 80 ס"מ + קולט אדים משולב (Downdraft), מנוע בסוקל
- מדיח אינטגרלי 60 ס"מ, פתיחת לחיצה
- 3 כסאות בר עור LT-01, ישיבה 65+
- אבן: אימפרגנציה נגד כתמים
- עץ: שמן-לכה מט 10% (WD-01/02)
- מתכת: פליז מוברש PVD (MT-01)

הערות ייצור

1. כל המידות במ"מ אלא אם צוין.
2. מיטר אבן – חיתוך CNC במפעל, הרכבה באתר ע"י מתקין מוסמך.
3. פאנל מחורץ נשלף (Z) לגישה לצנרת ולחשמל.
4. התאמת ורידים (Book-match) בין רגלי המפל והמשטח.